




Scan Me

Explore the Project Portal
Within the project portal, you will find detailed 3D images, design insights, site specific information, and other relevant data to provide a comprehensive understanding of the design proposal and its associated details. Simply scan this code with your smartphone camera and tap to open the link.

EL10 | Existing South-West-Elevation

Printed Scale Factor | 1mm : 100mm
Scale Valid When Printed At : ISO 216 A1

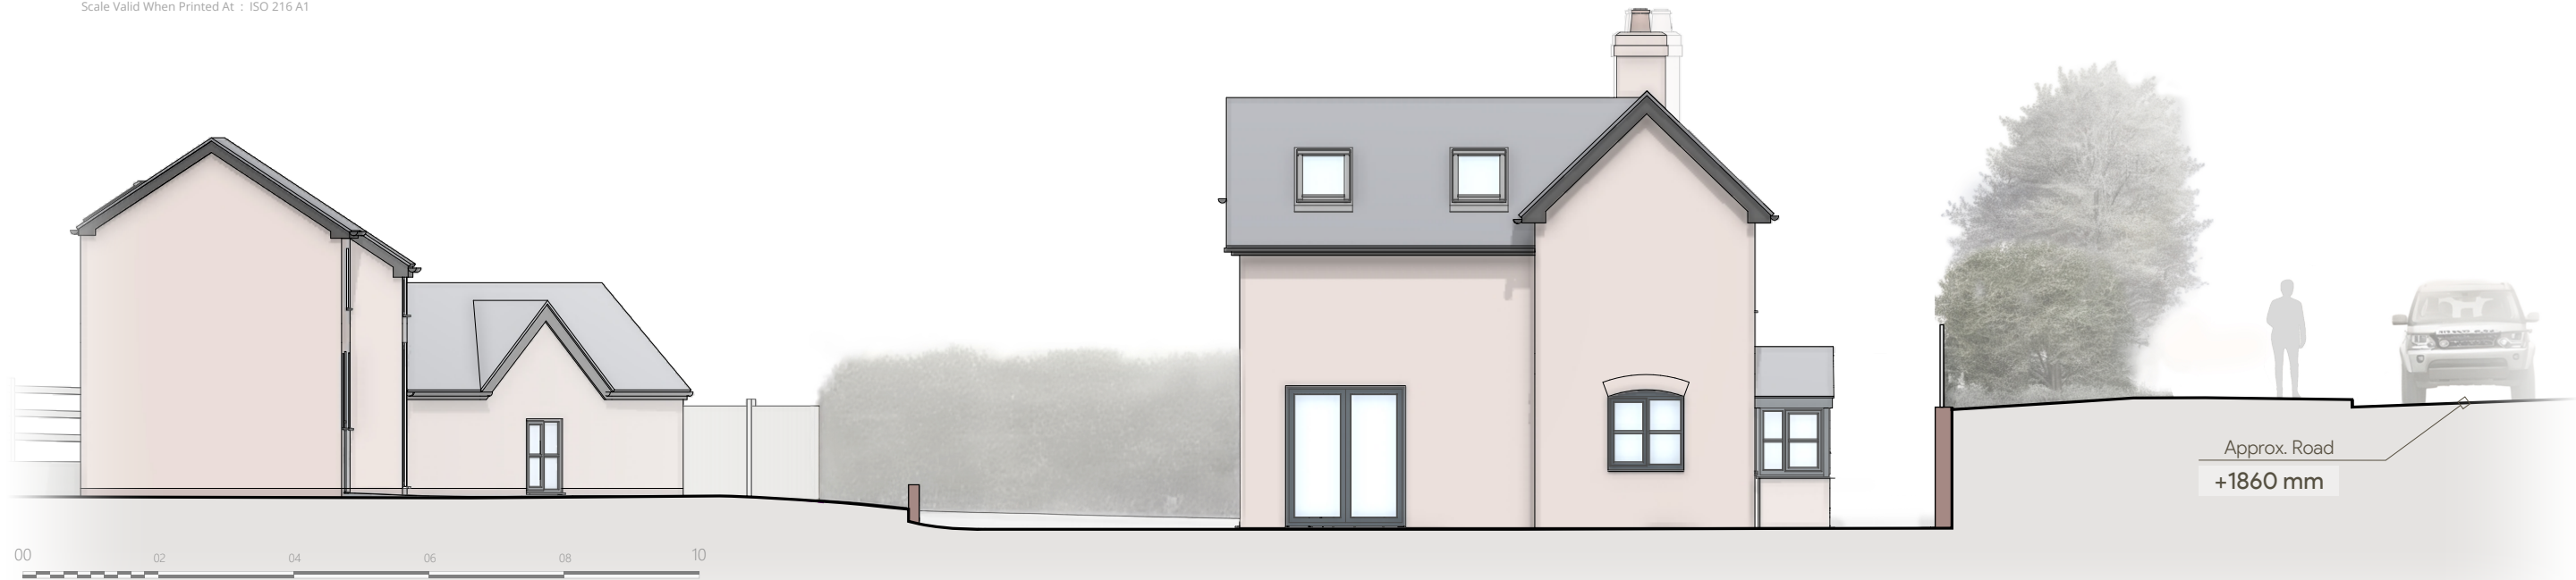

EL12 | Existing North-West Elevation

Printed Scale Factor | 1mm : 100mm
Scale Valid When Printed At : ISO 216 A1

Survey Tolerances

This project was surveyed using a SLAM Lidar Scanner, achieving the RICS survey detail accuracy of band E. Therefore, Noble Architecture can guarantee an accuracy of +/- 25mm.

EL13 | Existing South-East Elevation

Printed Scale Factor | 1mm : 100mm
Scale Valid When Printed At : ISO 216 A1



EL11 | Existing North-East Elevation

Printed Scale Factor | 1mm : 100mm
Scale Valid When Printed At : ISO 216 A1

SC10 | Existing Finishes Schedule

Code	Element	Material	Finish	Details
WT01	Original Walls	Brickwork	Weathered Red	Older parts of the existing structures feature traditional Staffordshire red brickwork with some re-pointing work conducted when the building was last renovated, walls likely solid brick construction;
WT02	Renovation Walls	Brickwork	Weathered Red	Previous alterations to the existing buildings used modern cavity walls closely matching host structures colour, texture, dimensions etc with highly sympathetic matching for reconstructed sections.
RF01	Tiled Roof	Traditional Slate	Grey	Traditional slate tiles with decorative crested ridge tiles.
RF02	Flat Dormer Roof (Guest House)	Felt	Grey	Three-layer felt covering used on the existing study roof.
RG01	Fascia's & Soffits	uPVC	Black	Fascia's & Soffits to both buildings are modern black uPVC
RG02	Rainwater Goods	uPVC	Black	Modern black UPVC Guttering & Downpipes, Aco surface drainage used throughout site.
WD01	Windows (Main Cottage)	uPVC	RAL 7016	Modern uPVC Windows & large picture windows / folding door sets, featuring double glazed units, added during most recent renovation.
WD02	Windows (Guest House)	uPVC	RAL 7016	Modern uPVC Windows with double glazed units, added during most recent renovation.
SP01	Solar Panels	Photovoltaic Glass	Dark Blue / Black	Integrated into south-facing roof slopes for sustainable energy use.

PLANNING OFFICER

Existing Site Context Photographs

Noble Architecture has compiled a comprehensive collection of site survey images, including drone photography, which are available upon request. Should these be of assistance, please reach out to Noble Architecture directly.

CONTRACTOR


Ensuring Material Consistency

The contractor is required to carefully match new materials to the existing structure, ensuring an exact match in colour, material, and texture is achieved.

Existing Conditions


EL20 | Proposed South-West Elevation

Printed Scale Factor | 1mm : 100mm
Scale Valid When Printed At : ISO 216 A1

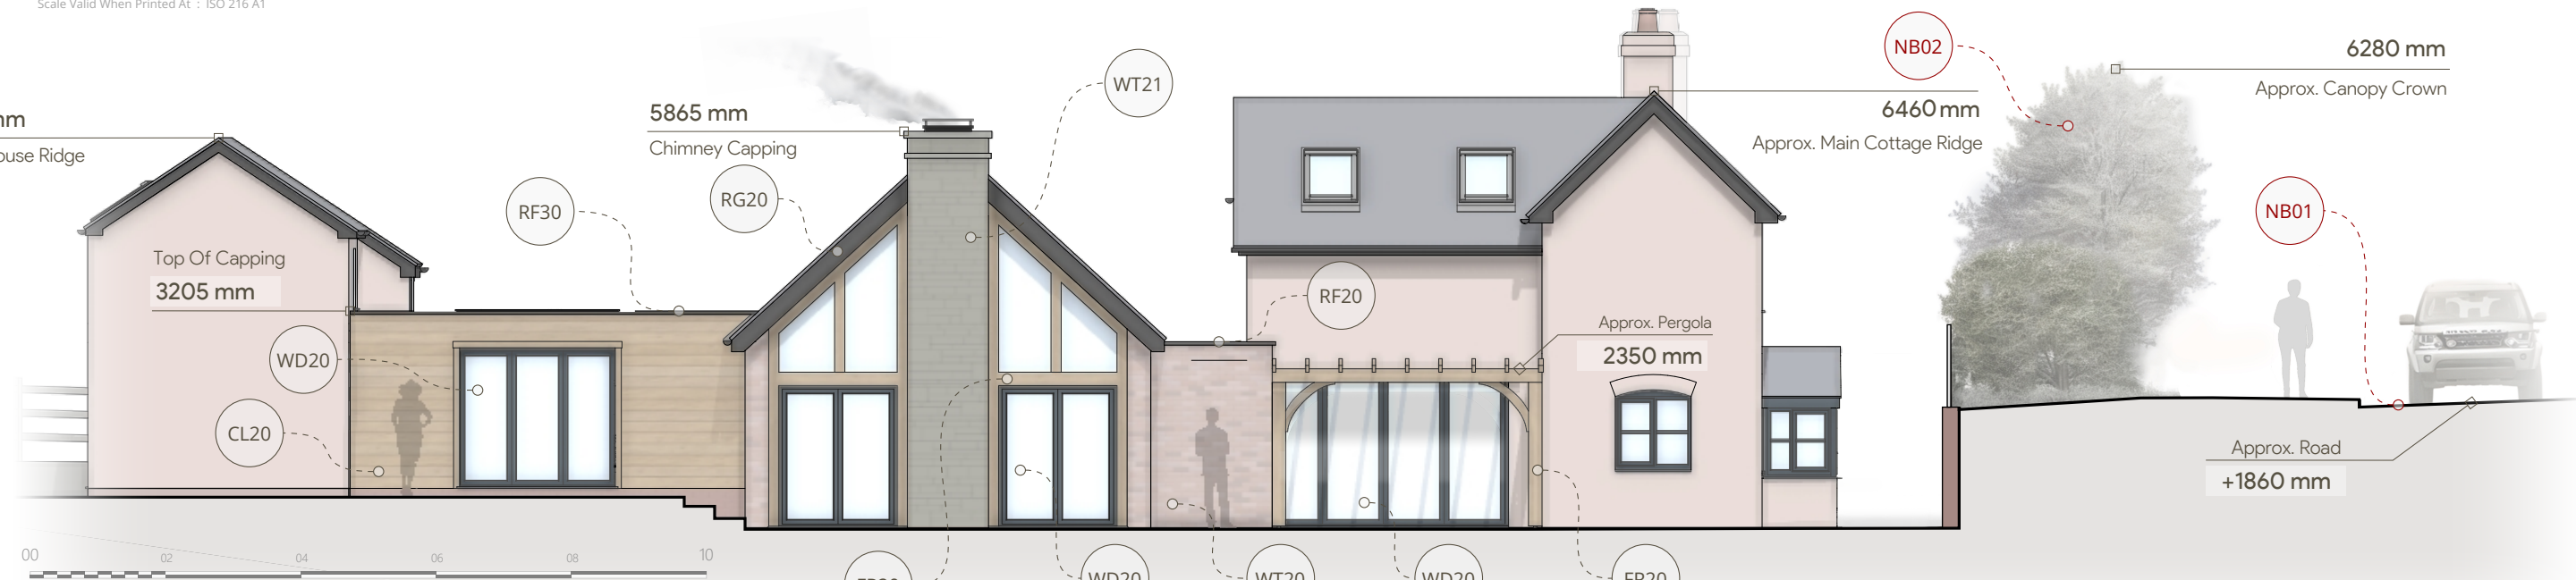

EL22 | Proposed North-West Elevation

Printed Scale Factor | 1mm : 100mm
Scale Valid When Printed At : ISO 216 A1

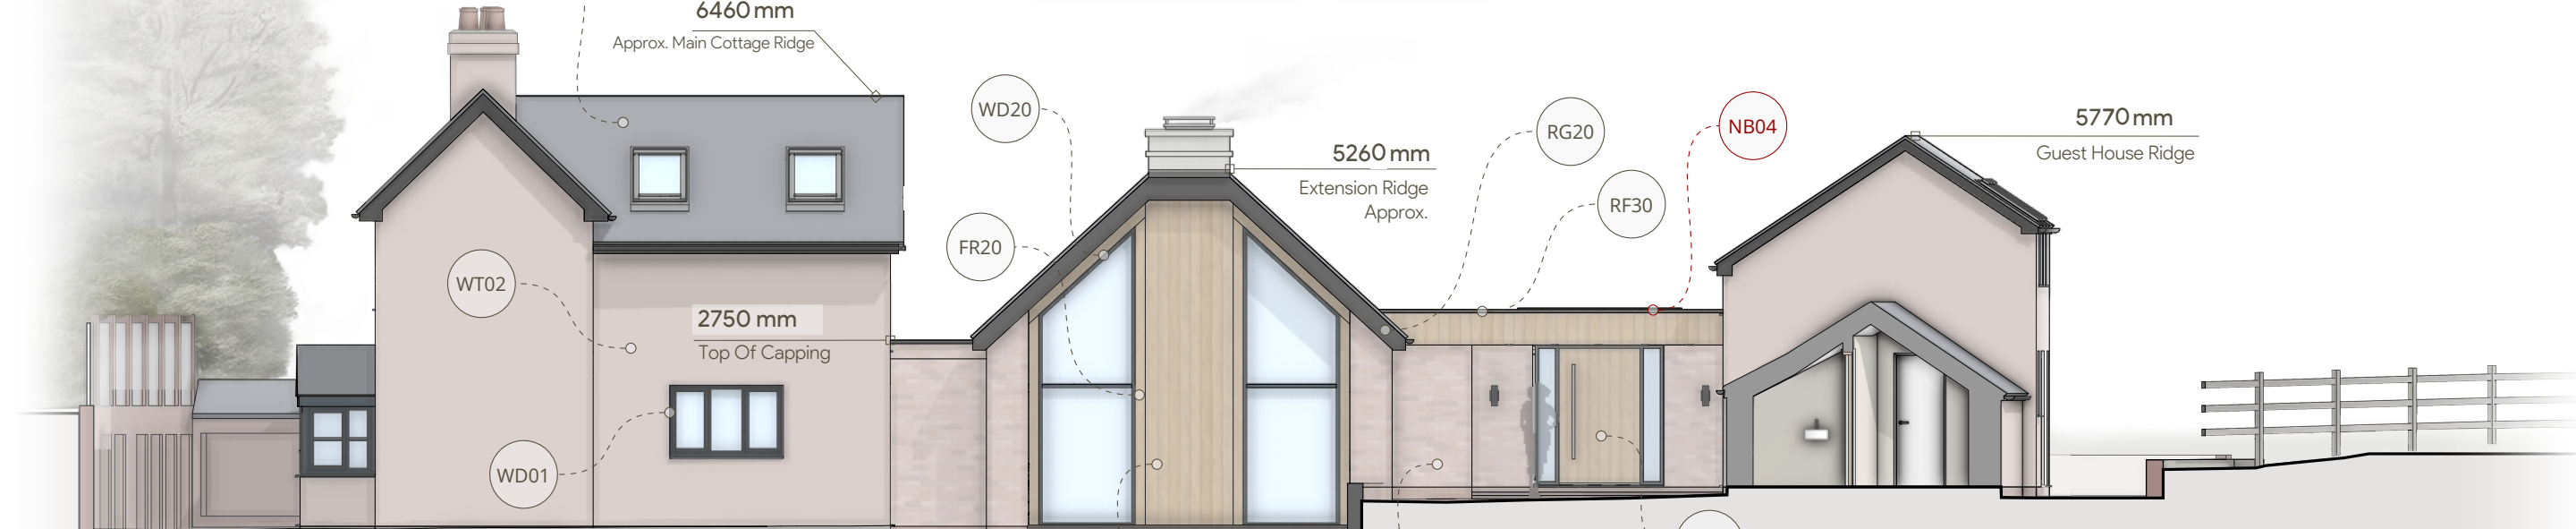

EL23 | Proposed South-East Elevation

Printed Scale Factor | 1mm : 100mm
Scale Valid When Printed At : ISO 216 A1



EL21 | Proposed North-East Elevation

Printed Scale Factor | 1mm : 100mm
Scale Valid When Printed At : ISO 216 A1

Design Proposals



Global Height Benchmark

Datum GCP | Ground Floor Finished Floor Level

All height measurements on this drawing are taken from the existing ground floor finished floor level, which serves as the universal site datum benchmark unless otherwise specified. Heights are set globally based on the primary ground control point established during the survey. If exact coordinates of this ground control point are required, please contact Noble Architecture.

PRELIMINARY DRAWING:

This plan provides a preliminary outline of the proposed scheme and is not intended for construction use. It is designed for planning officials and early stage project tendering only. Before issuing final construction drawings, further design coordination with specialists is required. Using this plan for construction is at the user's risk with no guarantees regarding its accuracy or completeness. Noble Architecture or any affiliated parties are not liable for any errors or discrepancies. By using this document for construction, the user agrees to indemnify all involved parties against claims or damages stemming from its use.

SC20 | Proposed Finishes Schedule

Code	Element	Material	Finish	Details
WT20	Brick Walls	Brickwork	Weathered Red	Match all new brickwork to the existing structure, using modern cavity wall construction. Ensure bricks and mortar match the exact existing building in colour, texture, dimensions, and pointing style.
WT21	Feature Chimney	Natural Stone	Grey/ Dark Grey <i>(TBC)</i>	The chimney is a key focal point on the North West elevation. The exact finish is pending client approval but will feature natural stone with varied sizes, creating an attractive yet harmonious contrast with the elevation.
RF20	Tiled Roof	Traditional Slate	Grey Natural Cut Slates	Use traditional slate tiles, reclaimed where budget permits. Install decorative ridge tiles to match the existing decorative crested roof ridge. Ensure an exact match with the existing roof in colour, texture, tile size, and head laps <i>(subject to manufacturer/supplier instructions)</i> to guarantee seamless visual continuity with the host buildings roofs.
RF30	Green Roof	Planting System	Biodiverse Planting	Install a biodiverse green roof system to the flat roof section, planted with endemic Staffordshire wildflowers, sedums, and grasses. The system must reduce surface water run-off, contribute to flood mitigation, and enhance biodiversity by creating habitats for pollinators and small wildlife. The planting will also soften visual impact and integrate the extension with the surrounding landscape character.
RF40	Flat Roof	EPDM / GRP	Dark Grey Finish	Provide a durable flat roof system using EPDM or GRP membranes. Finish to be a consistent dark grey to ensure visual continuity with adjoining roof surfaces and minimise maintenance requirements.
FR20	Framework	Natural Oak	Traditional Weathered	Solid oak framework, left untreated to weather naturally, complementing the rural setting and typical regional vernacular. Used for both the feature picture window and veranda. Non-opening sections of the picture window should feature direct-glazed, high-performance double or triple glazing.
CL20	Wall Cladding	Natural Oak	Traditional Weathered	Install 200mm natural oak boards in a horizontal array with a minimum 35mm overlap between boards.
WD20	Windows & Doors	Aluminium	RAL 7016 Anthracite Grey	Use high-quality aluminium units where budget permits. UPVC may be used as a lower-cost alternative. Install environmentally friendly low-E argon double or triple glazing to all units & use toughened glass where needed.
ED20	Entrance Door	Oak	Finished Oak Joinery	Use a large secure door with a warranty-backed, on a pivot hinge, insurance-approved multipoint locking system.
RG20	Fascias & Soffits	uPVC	RAL 9005 Jet Black	Fascias & Soffits to match the colour, profile, and sizes used on the host buildings.
RG21	Gutters & Pipework	uPVC	RAL 9005 Jet Black	Gutters & Pipework soffits to match the colour, profile, and sizes used on the host buildings.
PT20	Patio	Stone	Natural Sandstone <i>(TBC)</i>	A new patio will be laid, extending slightly outward from the North West elevation. The exact materials and style are pending client approval and will include new steps to accommodate elevation changes on the site.