


EXISTING LOCATION PLAN 1:5000

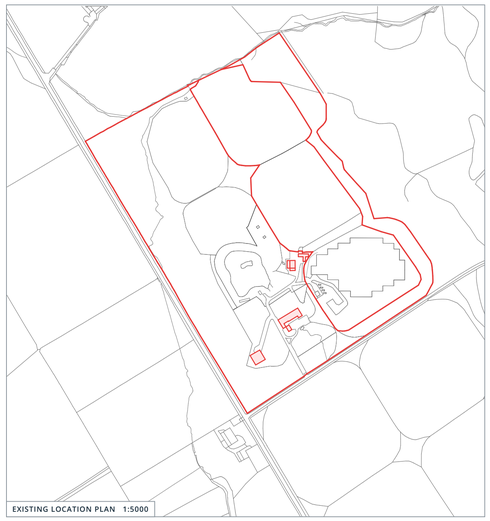

EXISTING SITE - BLOCK PLAN 1:1250

0 25 50 75 100 125 150 175 200 225 250

NOTES

SE01 | Existing dwelling
Existing house occupies the central developed part of the holding. Replacement dwelling proposed in this area; refer to D13 for the proposed layout.

SE02 | Existing hay barn
Steel-framed hay barn with lean-tos to one side and one end; asbestos cement roof sheeting throughout, weathered. Main barn 8,570 x 12,540 mm; 16,440 mm long including the end lean-to. Demolish in full after an asbestos refurbishment and demolition survey; sheeting removed by a specialist asbestos contractor, licensed where required, and disposed of as hazardous waste. Site of the Lake House of SP04.

SE03 | Existing stables shed
Stables shed beside the hay barn of SE02. Demolish in full; site returned to grassland except where the access roadway of SP03 crosses it.

SE04 | Existing helicopter hangar
Detached helicopter hangar at the wooded edge of the developed area. Existing landing strip extends towards the house. Hangar remains shown on the proposed site plan.

SE05 | Existing landing strip
Existing paved helicopter landing strip between the hangar and house. Part retention and revised access arrangement proposed; retained extent to SP05.

SE06 | Existing access roads
Existing internal roads connect the entrance from Deans Lane with the house, hangar, hay barn and stables shed. Refer to D13 for the revised circulation arrangement.

SE07 | Existing lake
Existing lake and island beyond the rear of the house. Lake retained within the proposed landscape setting; distinguish from the smaller front pond of SE10.

SE08 | Existing turbines
Two existing turbine positions identified on the supplied site markup, not a measured location. Positions to be confirmed by the applicant's topographical survey before a full application.

SE09 | Existing internal fences
Existing internal fencing separates the house and lake, including the sports fence identified for removal. Removal limits to SP13.

SE10 | Existing front pond
Small pond, about 22 m², in front of the house, separate from the main lake; a watercourse runs between it and the south-east boundary. Source and direction of flow unknown; applicant's drainage engineer to survey them before any work to the pond. Lies under the proposed forecourt of SP02; fill only once the relocated pond of SP11 is made and planted.

SE11 | Existing tree lines
Existing woodland belts and tree lines enclose the developed site. Refer to D13 for the woodland clearance of SP12 and the local adjustments at SP20; individual tree retention and removal to be established by the applicant's arboriculturist.

SE12 | Existing solar array
Existing ground-mounted solar PV array beyond the hay barn and stables shed, reached from the internal access road. Array remains shown on the proposed site plan.

SE13 | Existing site access
Single vehicular access to the holding from Deans Lane, through a gated entrance; all vehicles enter and leave here. Retained as the original access of SP24.

GN01 | Drawing Scope
Drawings describe the proposed development for planning assessment. They are not construction drawings or a complete Building Regulations specification. Obtain coordinated construction details, structural calculations and Building Control approval before relevant work starts. Refer discrepancies to Noble Architecture before proceeding.

GN02 | Survey And Dimensions
Site information derived from a photogrammetric aerial survey of the holding, with purchased Ordnance Survey data to the site plans. No measured building survey of the existing dwelling has been carried out. Proposed buildings are derived from Noble Architecture's three-dimensional model. Do not scale from these drawings. Verify all dimensions on site.

GN03 | Pre-Application Status
Issued for pre-application advice. Materials, dimensions and levels are indicative at this stage and to be fixed before a planning application.

Mapping Data Credentials
OS License Number: 100053143
© Crown copyright 2026 Ordnance Survey

N

NOBLE ARCHITECTURE

CLIENT	SITE ADDRESS	DRAWING TITLE	DOCUMENT ID	REV	SCALE	DATE	DRAWN BY	STATUS
Mr S. Stoffel	West Beacon Farm, Deans Lane, Woodhouse Eaves, LE12 8TE	Existing Site Plan	RB05_T01_D12	Revision B	1:1250 & 1:5000 @ ISO A1	19 Oct 2026	Noble Architecture	PRELIMINARY

NAVIGATE THIS BUILDING IN 3D
Scan this drawing to enter the 3D model and view the building in full 3D, and to freely navigate and take a tour.