
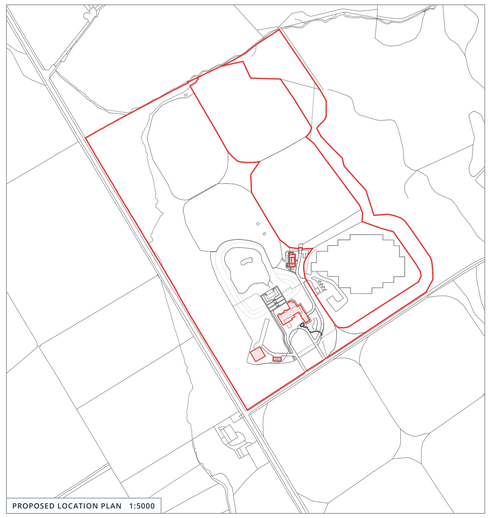


PROPOSED LOCATION PLAN 1:5000

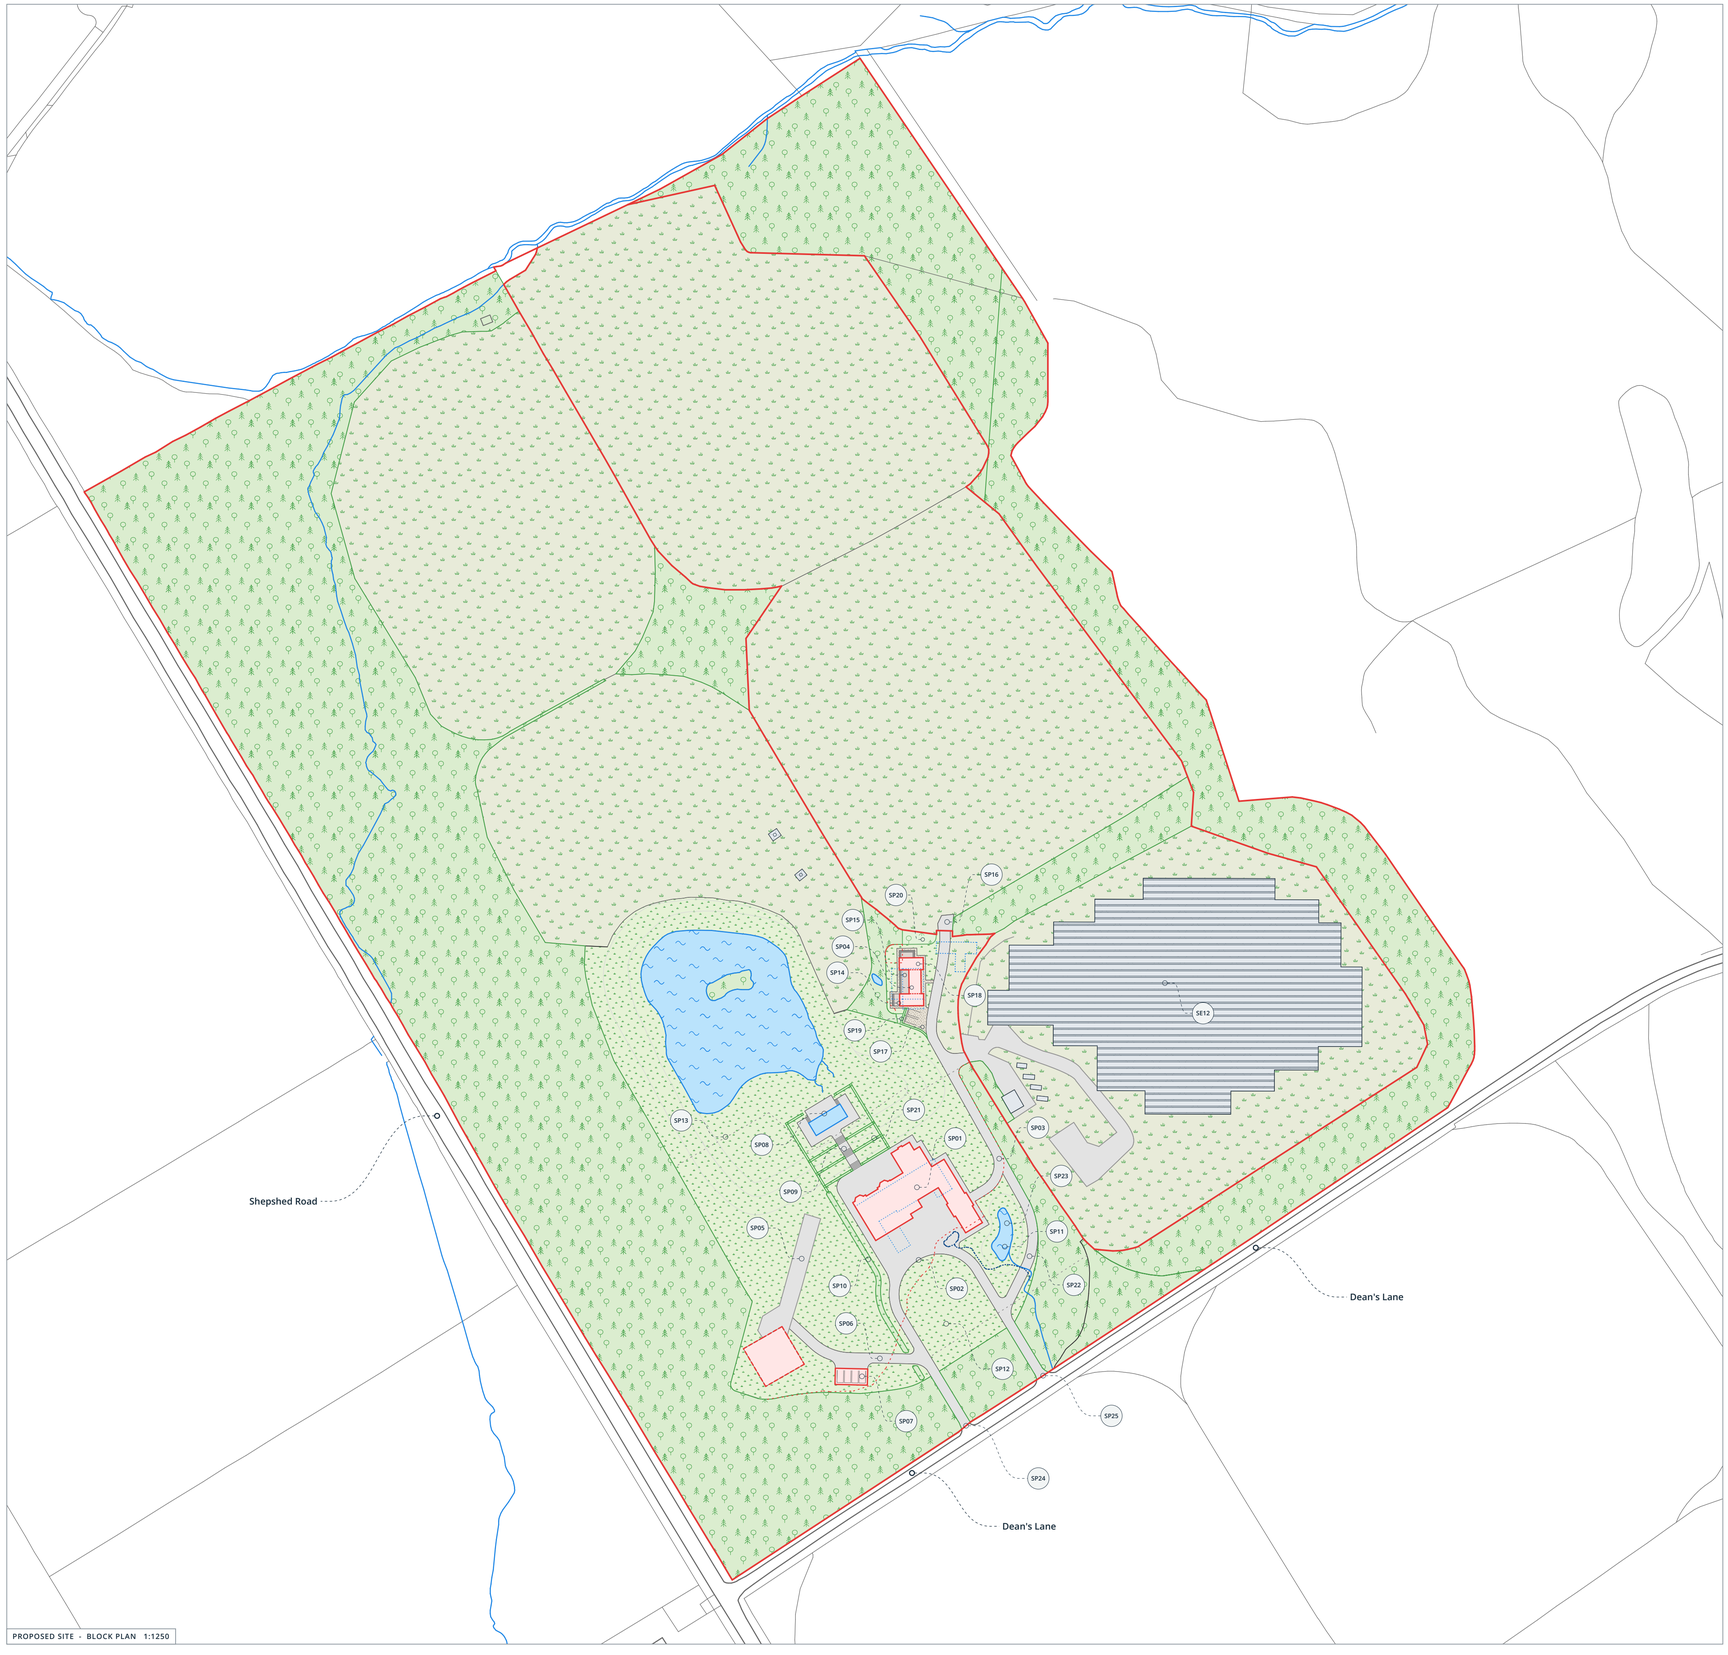

PROPOSED SITE - BLOCK PLAN 1:1250

0 25 50 75 100 125 150 175 200 225 250

NOTES

SE12 | Existing solar array
Existing ground-mounted solar PV array beyond the hay barn and stables shed, reached from the internal access road. Array remains shown on the proposed site plan.

SP01 | Replacement house
Replacement dwelling comprises the main house, linked kitchen building and coach house. Principal entrance faces the horseshoe drive; rear garden faces the proposed pool and existing lake.

SP02 | Horseshoe carriage drive
New horseshoe-shaped drive to the principal entrance, joining Deans Lane at the accesses of SP24 and SP25. Turning circles, radii, splays and arcs shown are illustrative only, not designed vehicle geometry. Applicant to appoint a civil engineer to design alignment, widths, tracking and surfacing before a full application.

SP03 | Lake House access route
New side access roadway through the carriage arch of CE02 to the Lake House of SP04 and the field gate of SP16. Lake House joined to it by a 1,200 mm gravel path from the middle unit; parking of SP17 opens onto it. Service access road of SP22 joins it beyond the arch. Clearances and vehicle movements shown are illustrative; applicant's civil engineer to confirm them, with pedestrian access, before a full application.

SP04 | Lake House outbuildings
Three single-storey Bonni Large+ outbuildings on the hay barn site of SE02. Each 9,800 x 4,900 mm, max. 4,500 mm high overall to the manufacturer's figure; dual-pitched roof ridged along its length. Painted corrugated steel walls and roof. Floor levels and Bonni palette colour to be confirmed before a full application. Arranged as a north-south L the middle unit set to the east, leaving a decked court facing the lake. Use to SP18; foundations to SP14; decking to SP15.

SP05 | Landing strip retention
Retain part of the existing paved landing strip serving the hangar. Reconfigure the connecting road to meet the new driveway; retained and removed surfacing to be measured from the applicant's topographical survey before a full application.

SP06 | Side road to hangar parking
New side road through the tree line between the hangar and the approach from the original access of SP24, serving the parking of SP07. Alignment and turning shown are illustrative; applicant to appoint a civil engineer, and an arboriculturist for tree impacts, before a full application.

SP07 | Parking and potential future carport
Four open parking spaces against the tree line at the end of the side road of SP06: designated parking away from the entrance front, with overspill for guests and hangar visitors. No carport or other structure forms part of this application; the area may be considered for a carport in future. Surfacing and layout to be designed by the applicant's civil engineer before a full application.

SP08 | Infinity-edge pool
Swimming pool, 15,000 x 6,000 mm, on the central axis of the house, in a paved surround on two levels. Infinity edge to the lake-facing north-west side, with a lower paved terrace below it, 12,600 x 5,000 mm, reached by three steps at each end. Applicant to appoint a pool specialist and engineers to design levels, retaining edges, overflow, drainage, pool water discharge, lighting, finishes and plant location before a full application.

SP09 | Central garden steps
Steps 4,000 mm wide on the axis of the house, from the house terrace down through the hedged lawn terraces of SP21 to the pool surround of SP08, in three flights with two paved landings. Levels shown are illustrative; levels, rises, retaining edges and step-free access to be fixed from the applicant's topographical survey before a full application.

SP10 | Hangar privacy hedge
New privacy hedge along the hangar line. Alignment, species, planting size, spacing and maintained height to be set by the applicant's landscape architect before a full application, with the sightlines and retained trees.

SP11 | Relocated pond
New pond, up to about 111 m² at its fullest, five times the old pond of SE10, between the horseshoe drive and the service access road of SP22. Margins and planting designed as habitat. Make and plant it before the old pond is filled; further ponds if the newt survey of SE10 requires them. Levels and bank profiles to the topographical survey before a full application; drainage to SP23.

SP12 | Tree and woodland clearance
Woodland cleared: about 1,070 m² for the service access road of SP22 and the pond of SP11, and about 920 m² within the horseshoe drive, laid to lawn. Local adjustments to the tree lines at the accesses and parking. Applicant to appoint an arboriculturist to assess the trees and identify individual removals, protection and replacement planting before a full application. Retain as many trees as possible, keeping the woodland screen along Deans Lane.

SP13 | Internal fence removal
Remove the internal fences identified within the revised garden layout, including the fences/walling between house and lake. Removal limits shown are indicative, to be confirmed by the applicant before a full application; no external boundary removal proposed.

SP14 | Lake House foundations
Lake House of SP04 on auger piles: Bonni ground screws, number and size set by a soil test. No concrete slab, strip footings or other permanent foundation; the buildings can be lifted away and the screws withdrawn, returning the ground to grass. Screw positions to the design of Bonni and the applicant's structural engineer, set out with the applicant's arboriculturist where they fall within the root protection areas of retained trees.

SP15 | Raised decking
Three raised timber decks to the Lake House of SP04. West court between the units, 3,900 x 9,800 mm, facing the lake. South unit: 3,000 mm projection to the west, facing the lake. North unit: 3,000 mm projection to the north. Each deck with about three steps down to the ground; deck heights and number of steps to suit levels from the applicant's topographical survey before a full application.

SP16 | Field gate access
Existing field gate on the site boundary beyond the Lake House retained, with the track to it. Straight vehicle route to the gate kept clear along the roadway east of the Lake House; no parking in front of it. Reached by SP03; parking to SP17.

SP17 | Lake House parking
Two parking spaces on a gravel pad south of the Lake House, opening onto the access roadway of SP03. Sufficient for the household and the occasional visitor. New hedge along their south and west sides to SP19.

SP18 | Lake House use
Lake House of SP04 used as a home office, home recording studio and home gym by the occupiers of the dwelling; part of its residential use, Use Class C3, and ancillary to it. Not a dwelling: no living or sleeping accommodation. Not business premises; no separate use.

SP19 | Hedge and infill planting
New hedge, about 19.8 m long, along the south and west sides of the parking of SP17. Small area of new tree planting south-west of the parking, linking the hedge to the existing woodland. Species, planting sizes and spacing to be set by the applicant's landscape architect before a full application.

SP20 | Shelter and firebreak planting
New tree planting north of the Lake House of SP04, up to the site boundary, as a shelter belt. Trees held back about 5 m from the north and west walls, with gravel and grass between, as a firebreak. Woodland cut back locally around the group, mostly to grass; individual tree removals to the applicant's arboriculturist. Species, sizes and spacing to be set by the applicant's landscape architect before a full application.

SP21 | Hedged lawn terraces
Three level lawns step down from the house to the pool of SP08, a clipped hedge at each fall. Hedges enclose the garden; 15,000 mm lake-side opening in line with the pool. Clipped blocks at the steps and corners. Levels from the applicant's topographical survey; hedge species, heights and how each fall is formed to be set by the applicant's landscape architect before a full application.

SP22 | Service access road
New road, 4,000 mm wide, from the horseshoe drive's east arm to the Lake House route of SP03 beyond the carriage arch, for occasional deliveries and larger vehicles; the arch of CE02 takes cars and high-roof vans. Cut through woodland; tree removals to SP12. Crossing of the watercourse of SP23: clear span explored first, any culvert the minimum length, subject to the County Council's consent. Alignment, surface and edging to be designed by the applicant's civil engineer before a full application.

SP23 | Pond drainage
Pond of SP11 intended as the drives' low point, taking their surface water through silt control. As drawn, overflow at a controlled rate to the retained lower channel of the existing watercourse, subject to the survey confirming its fall. Any spring or watercourse feeding the pond of SE10 carried to the new pond in an open channel where practicable; a pipe only with the County Council's consent. Applicant to appoint a drainage engineer to design the surface water scheme before a full application.

SP24 | Original site access
Existing gated entrance from Deans Lane of SE13, retained. Serves the horseshoe drive of SP02 and the side road of SP06. With SP25, one of two accesses: separate in and out gates, both automatic and linked to the site security and access control system.

SP25 | New site access
Second vehicular access onto Deans Lane, north-east of the original access of SP24, where the east arm of the horseshoe drive of SP02 meets the lane. Automatic gate linked to the site security and access control system. Visibility splays and access design to be agreed with the local highway authority at full application stage, as advised by the LPA.

GN01 | Drawing Scope
Drawings describe the proposed development for planning assessment. They are not construction drawings or a complete Building Regulations specification. Obtain coordinated construction details, structural calculations and Building Control approval before relevant work starts. Refer discrepancies to Noble Architecture before proceeding.

GN02 | Survey And Dimensions
Site information derived from a photogrammetric aerial survey of the holding, with purchased Ordnance Survey data to the site plans. No measured building survey of the existing dwelling has been carried out. Proposed buildings are derived from Noble Architecture's three-dimensional model. Do not scale from these drawings. Verify all dimensions on site.

GN03 | Pre-Application Status
Issued for pre-application advice. Materials, dimensions and levels are indicative at this stage and to be fixed before a planning application.

Mapping Data Credentials
OS License Number: 100053143
© Crown copyright 2026 Ordnance Survey

N

NOBLE ARCHITECTURE	CLIENT: Mr S. Stoffel	SITE ADDRESS: West Beacon Farm, Deans Lane, Woodhouse Eaves, LE12 8TE	DRAWING TITLE: Proposed Site Plan	DOCUMENT ID: RB05_T01_D13	REV: Revision B	SCALE: 1:1250 & 1:5000 @ ISO A1	DATE: 19 Oct 2026	DRAWN BY: Noble Architecture	STATUS: PRELIMINARY	NAVIGATE THIS BUILDING IN 3D: Scan this drawing to enter the 3D model and view the building in full 3D, and to freely navigate and take a tour.	