





Use your phone or tablet camera

View Project Portal

- Walk Through the 3D Model
- Saved Scenes and Viewpoints
- Measuring Tools
- Live Drawings Online

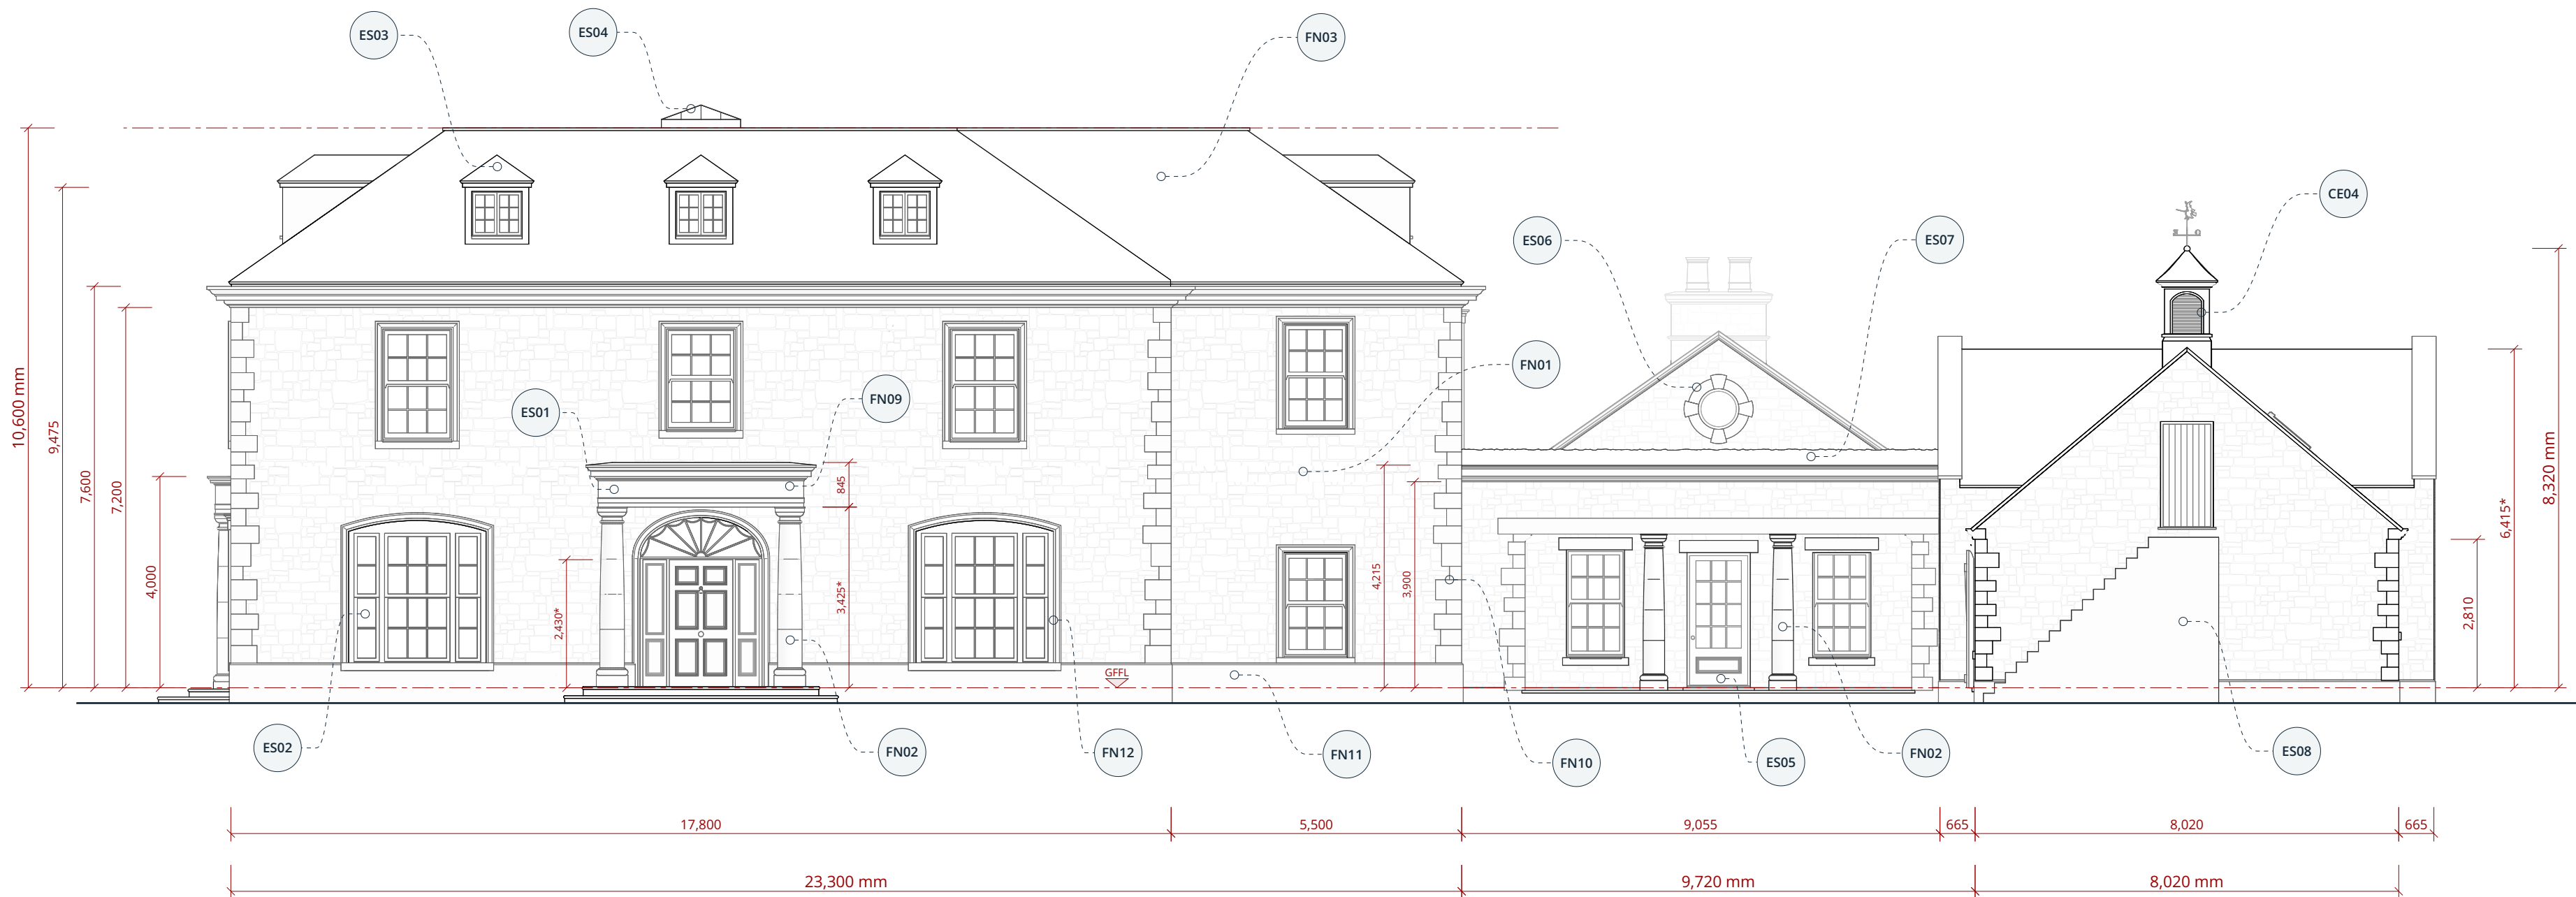

PROPOSED SOUTH EAST ELEVATION - HOUSE FRONT FASCADE

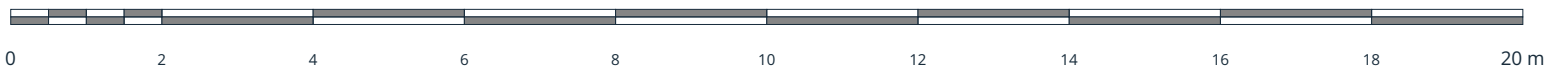

NOTES

ES01 | Entrance Porch
Central entrance: a pair of Tuscan columns on plinth blocks carry a full entablature with a projecting moulded cornice. Beneath it a six-panel painted timber door with a semicircular radial fanlight, dressed in cut ashlar and approached over stone steps. The porch projects slightly from the wall plane.

ES02 | Window Hierarchy
Tripartite ground floor windows flank the entrance beneath cambered heads with moulded ashlar surrounds, and are the tallest openings on the building. First floor sashes are shorter and set in plainer surrounds.

ES03 | Roof And Dormers
Hipped roof with three hipped dormers lighting the second floor. Dormer cheek and roof finish to be confirmed before a full application.

ES04 | Ridge Lantern
Low hipped glazed lantern set astride the main ridge at the centre of the house. Frame material and finish to be confirmed before a full application.

ES05 | Colonnade Entrance
Single-storey colonnade entrance to the right of the main block: Tuscan columns flanking a glazed painted timber door, with flat ashlar lintels over the windows either side, beneath a flat roof with a moulded cornice. Leads through to the kitchen building and the coach house.

ES06 | Kitchen Building Gable
Kitchen building gable above the colonnade entrance: moulded raking cornice, with a circular opening set in cut ashlar with four projecting keyblocks. Stone chimney stack rises behind.

ES07 | Colonnade Balcony
Balcony over the colonnade entrance, reached down steps from the master bedroom suite. Parapet set back from the face below, with planting beds to the edges in place of a balustrade. The set-back keeps the balcony reading as the colonnade roof from ground level. Refer to the three-dimensional model on the project portal.

ES08 | Coach House External Stair
Indicative external staircase to the accommodation over the coach house, shown to establish the access only. Form, construction and finish to be confirmed before a full application.

FN01 | Walling Stone
Coursed squared natural stone walling to the external walls of the house, the kitchen building and the coach house. Rough faced and laid to courses, with the dressed elements in cut ashlar of the same stone as FN10, FN11 and FN12. Stone type and source to be confirmed before a full application.

FN02 | Classical Order
All columns and pilasters are of the Tuscan order in cut ashlar: the entrance porch, the loggia arcade and the colonnade entrance.

FN03 | Roof Covering
Natural stone slate laid to diminishing courses to all pitched roofs. Stone slate type, and whether new or reclaimed, to be confirmed before a full application.

FN09 | Classical Entablatures
Full Tuscan entablature to the entrance porch, the loggia arcade and the colonnade entrance: plain architrave, unornamented frieze and projecting moulded cornice. Order as FN02. Profiles and proportions to be confirmed before a full application.

FN10 | Ashlar Quoins
Cut ashlar quoins of the same stone as the walling to every external angle of the house, the kitchen building and the coach house. Laid in alternating long and short courses. Finely dressed to contrast with the coursed walling of FN01. Coursing module and margin widths to be confirmed before a full application.

FN11 | Ashlar Plinth
Cut ashlar plinth of the same stone as the walling running continuously around the base of the house, the kitchen building and the coach house, returned at all projections and terminated against the external ground level. Height, projection and weathering detail to be confirmed before a full application.

FN12 | Cut Ashlar Dressings
Cut ashlar dressings of the same stone as the walling to the window and door surrounds, eaves cornice, canted bays, the two entrance compositions and the carriage arch. Finely dressed and moulded where shown. Profiles to be confirmed before a full application.

CE04 | Cupola
Cupola on the ridge above the gable: square base with an arched louvred opening and a moulded cornice, pyramidal roof, ball finial and weathervane. Material and finish to be confirmed before a full application.

GN01 | Drawing Scope
Drawings describe the proposed development for planning assessment. They are not construction drawings or a complete Building Regulations specification. Obtain coordinated construction details, structural calculations and Building Control approval before relevant work starts. Refer discrepancies to Noble Architecture before proceeding.

GN02 | Survey And Dimensions
Site information derived from a photogrammetric aerial survey of the holding, with purchased Ordnance Survey data to the site plans. No measured building survey of the existing dwelling has been carried out. Proposed buildings are derived from Noble Architecture's three-dimensional model. Do not scale from these drawings. Verify all dimensions on site.

GN03 | Pre-Application Status
Issued for pre-application advice. Materials, dimensions and levels are indicative at this stage and to be fixed before a planning application.