




Scan Me

Use your phone or tablet camera

View Project Portal

- Walk Through the 3D Model
- Saved Scenes and Viewpoints
- Measuring Tools
- Live Drawings Online

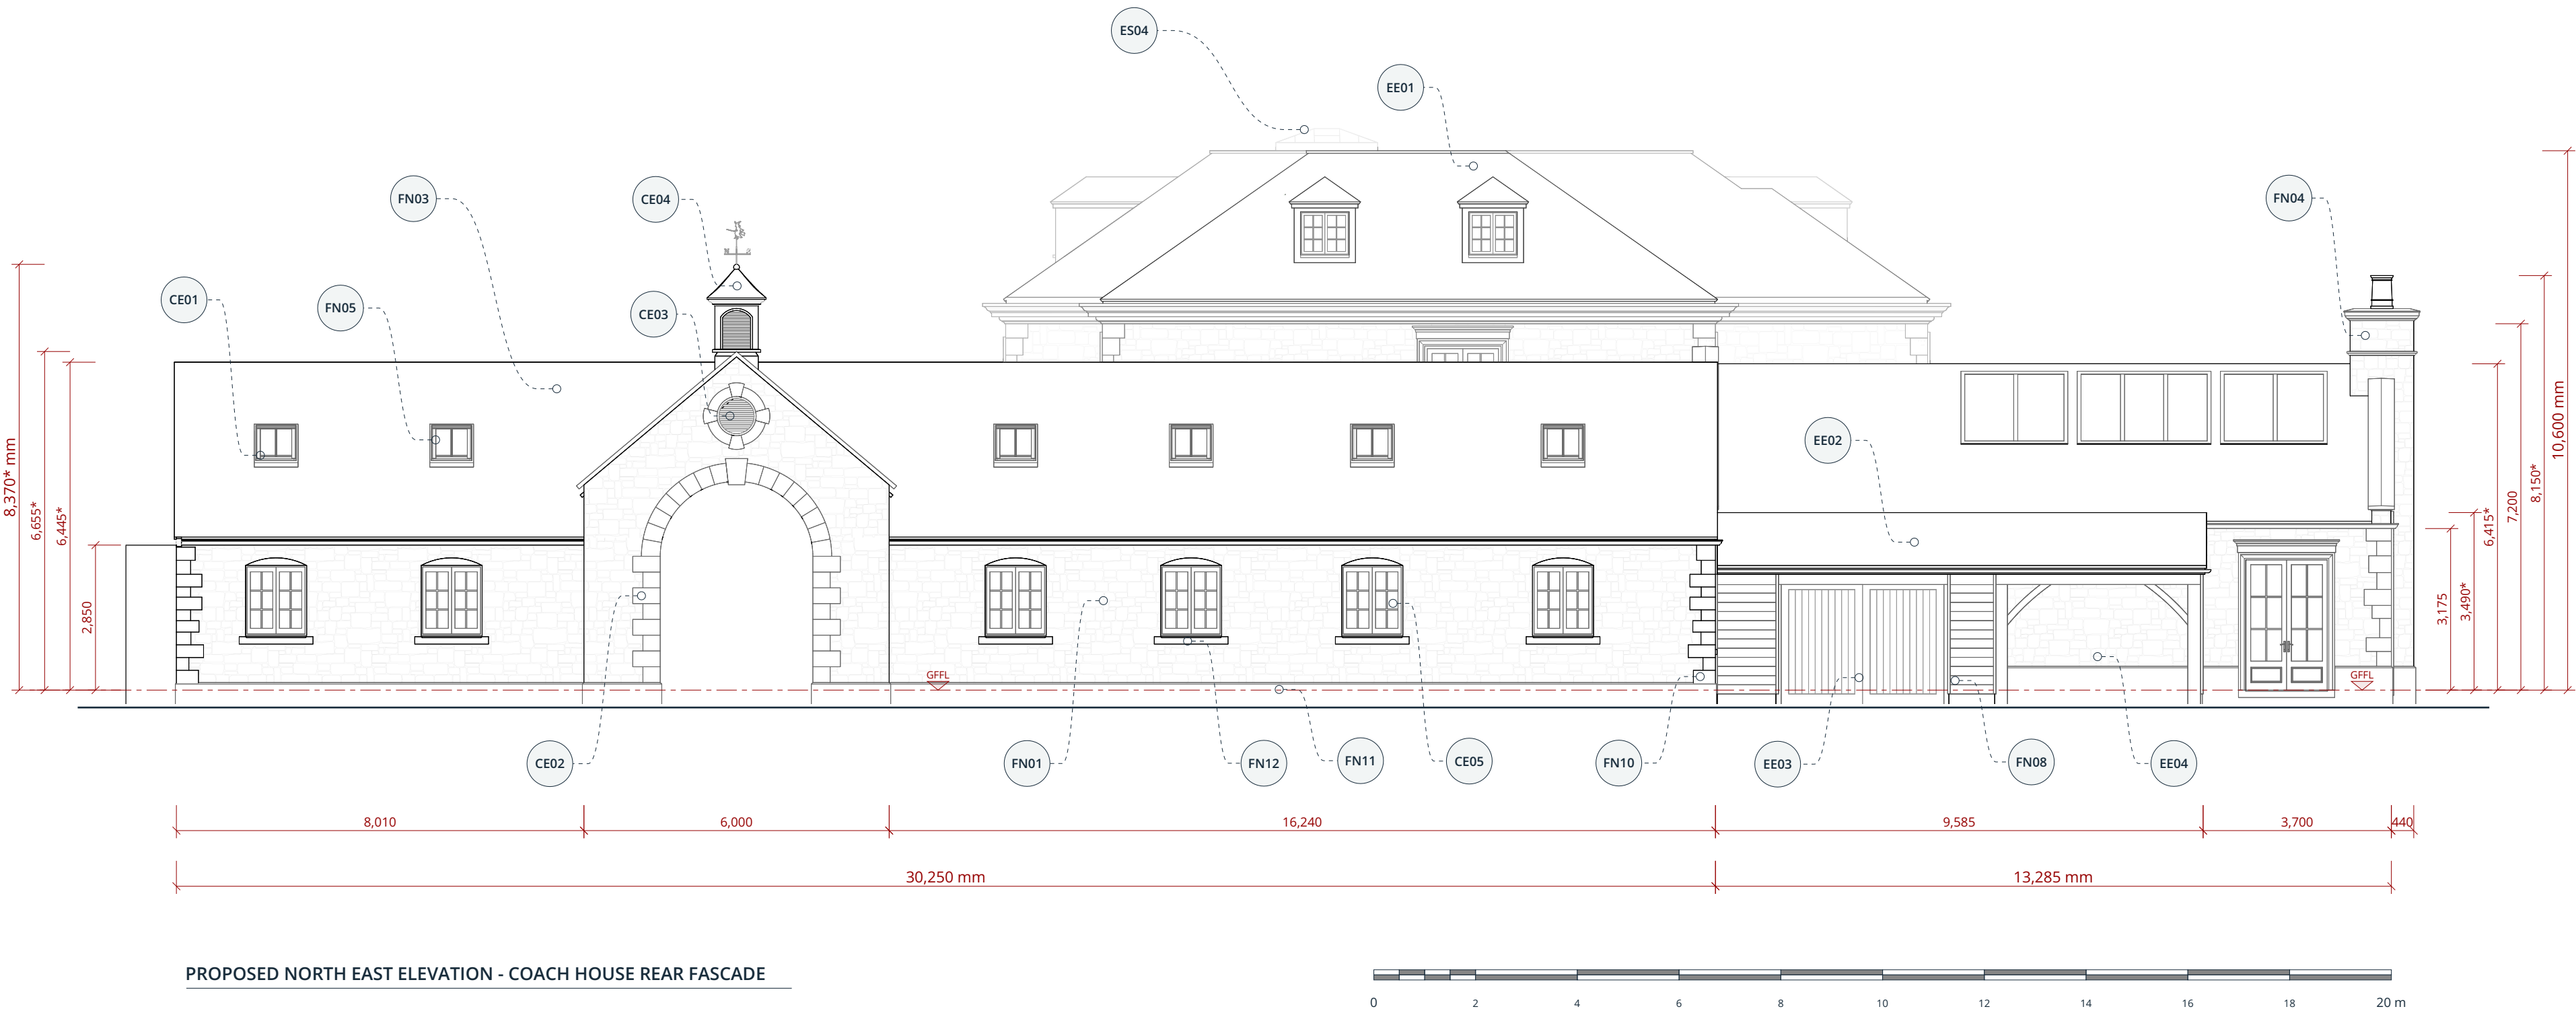

NOTES

- ES04 | Ridge Lantern**
Low hipped glazed lantern set astride the main ridge at the centre of the house. Frame material and finish to be confirmed before a full application.
- EE01 | House Roof Beyond**
The house is seen above the coach house range on this elevation: hipped roof with two hipped dormers and the moulded eaves cornice returning on this side.
- EE02 | Lean-To Store**
Single-storey lean-to store against the kitchen building, under a mono-pitch roof with eaves set below those of the kitchen building. Horizontal timber weatherboarding to the walls. Ancillary storage for garden furniture and pool equipment. Roof covering to be confirmed before a full application.
- EE03 | Lean-To Openings**
Enclosed bay fitted with a pair of vertically boarded timber doors. Adjoining bay left open to the front on timber posts with curved braces, against the stone wall of the kitchen building behind.
- EE04 | Lean-To Character**
Timber boarding, a low mono-pitch roof and an open bay set the store apart from the dressed stone of the house and carry the agricultural character of this end of the group. The store steps the eaves down between the kitchen building and the coach house.
- FN01 | Walling Stone**
Coursed squared natural stone walling to the external walls of the house, the kitchen building and the coach house. Rough faced and laid to courses, with the dressed elements in cut ashlar of the same stone as FN10, FN11 and FN12. Stone type and source to be confirmed before a full application.
- FN03 | Roof Covering**
Natural stone slate laid to diminishing courses to all pitched roofs. Stone slate type, and whether new or reclaimed, to be confirmed before a full application.
- FN04 | Chimney Stack**
Natural stone chimney stacks with moulded caps to the house, the kitchen building and the coach house.
- FN05 | Rooflights**
Conservation pattern rooflights set flush within the roof plane to the coach house. Kitchen building apex rooflights as FN06. Product to be confirmed before a full application.
- FN08 | Oak Weatherboard Cladding**
Weathered oak shiplap cladding to the lean-to store, laid horizontally, with vertically boarded and strapped doors. Left untreated to silver naturally. Board profile, lap and fixings to be confirmed before a full application.
- FN10 | Ashlar Quoins**
Cut ashlar quoins of the same stone as the walling to every external angle of the house, the kitchen building and the coach house. Laid in alternating long and short courses. Finely dressed to contrast with the coursed walling of FN01. Coursing module and margin widths to be confirmed before a full application.
- FN11 | Ashlar Plinth**
Cut ashlar plinth of the same stone as the walling running continuously around the base of the house, the kitchen building and the coach house, returned at all projections and terminated against the external ground level. Height, projection and weathering detail to be confirmed before a full application.
- FN12 | Cut Ashlar Dressings**
Cut ashlar dressings of the same stone as the walling to the window and door surrounds, cills, eaves cornice, cantled bays, the two entrance compositions and the carriage arch. Finely dressed and moulded where shown. Profiles to be confirmed before a full application.
- CE01 | Coach House Range**
Long single-storey range under a continuous pitched roof, with accommodation lit from within the roof slope.
- CE02 | Carriage Arch**
Central gabled bay carries a semicircular carriage arch turned in voussours with a projecting keystone, on cut ashlar impostes with quoined jambs. The arch carries the pedestrian and service route through from the courtyard.
- CE03 | Gable Oculus**
Circular louvred oculus in the gable above the arch, set in a cut ashlar surround with four projecting keyblocks.
- CE04 | Cupola**
Cupola on the ridge above the gable: square base with an arched louvred opening and a moulded cornice, pyramidal roof, ball finial and weathervane. Material and finish to be confirmed before a full application.
- CE05 | Range Windows**
Segmentally headed two-light painted timber windows with cut ashlar cills to the range.
- GN01 | Drawing Scope**
Drawings describe the proposed development for planning assessment. They are not construction drawings or a complete Building Regulations specification. Obtain coordinated construction details, structural calculations and Building Control approval before relevant work starts. Refer discrepancies to Noble Architecture before proceeding.
- GN02 | Survey And Dimensions**
Site information derived from a photogrammetric aerial survey of the holding, with purchased Ordnance Survey data to the site plans. No measured building survey of the existing dwelling has been carried out. Proposed buildings are derived from Noble Architecture's three-dimensional model. Do not scale from these drawings. Verify all dimensions on site.
- GN03 | Pre-Application Status**
Issued for pre-application advice. Materials, dimensions and levels are indicative at this stage and to be fixed before a planning application.