




Use your phone or tablet camera

View Project Portal

- Walk Through the 3D Model
- Saved Scenes and Viewpoints
- Measuring Tools
- Live Drawings Online



PROPOSED GROUND FLOOR PLAN

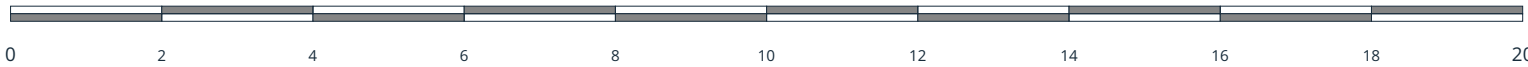

NOTES

GF02 | Principal Staircase
Principal staircase to the Grand Atrium is indicative. Its run, width, curvature and the floor area it occupies to be finalised once the flight is reset to the revised floor to ceiling heights.

GF03 | Room Names And Areas
Room names describe intended use at this stage. Floor areas are gross internal areas measured from the three-dimensional model, to be confirmed against the detailed drawings.

GF04 | Fitted Furniture And Fittings
Kitchen units, fitted furniture and sanitaryware are indicative and are not part of this design phase.

GN01 | Drawing Scope
Drawings describe the proposed development for planning assessment. They are not construction drawings or a complete Building Regulations specification. Obtain coordinated construction details, structural calculations and Building Control approval before relevant work starts. Refer discrepancies to Noble Architecture before proceeding.

GN02 | Survey And Dimensions
Site information derived from a photogrammetric aerial survey of the holding, with purchased Ordnance Survey data to the site plans. No measured building survey of the existing dwelling has been carried out. Proposed buildings are derived from Noble Architecture's three-dimensional model. Do not scale from these drawings. Verify all dimensions on site.

GN03 | Pre-Application Status
Issued for pre-application advice. Materials, dimensions and levels are indicative at this stage and to be fixed before a planning application.

Floor Areas

Room	Area
Ground Floor	549.86 m ²
Kids Lounge	39.50 m ²
Grand Atrium	35.40 m ²
Library	25.43 m ²
West Atrium	43.56 m ²
Executive Study	28.18 m ²
Grand Gallery	70.82 m ²
Formal Lounge	32.38 m ²
Bar Lounge	26.27 m ²
Formal Dining Room	41.79 m ²
Garden Room	25.81 m ²
Pantry	7.12 m ²
East Atrium	42.02 m ²
W/C	6.46 m ²
Family Lounge	41.49 m ²
Firewood Store	9.88 m ²
Shed	11.07 m ²
Kitchen	62.68 m ²
Total	549.86 m ²

Floor Areas

Room	Area
Ground Floor	5,919 ft ²
Kids Lounge	425 ft ²
Grand Atrium	381 ft ²
Library	274 ft ²
West Atrium	469 ft ²
Executive Study	303 ft ²
Grand Gallery	762 ft ²
Formal Lounge	349 ft ²
Bar Lounge	283 ft ²
Formal Dining Room	450 ft ²
Garden Room	278 ft ²
Pantry	77 ft ²
East Atrium	452 ft ²
W/C	70 ft ²
Family Lounge	447 ft ²
Firewood Store	106 ft ²
Shed	119 ft ²
Kitchen	675 ft ²
Total	5,919 ft ²



CLIENT
Mr S. Stoffel

SITE ADDRESS
West Beacon Farm, Deans Lane, Woodhouse Eaves, LE12 8TE

DRAWING TITLE
Ground Floor Plan

DOCUMENT ID
RB05_T01_D06

REV
Revision A

SCALE
1:100 @ ISO A2

DATE
23 Sep 2026

DRAWN BY
Noble Architecture

STATUS
PRELIMINARY

NAVIGATE THIS BUILDING IN 3D
Scan this drawing to enter the 3D model and view the building in full 3D, and to freely navigate and take a tour.

