




Scan Me

Use your phone or tablet camera

View Project Portal

- Walk Through the 3D Model
- Saved Scenes and Viewpoints
- Measuring Tools
- Live Drawings Online

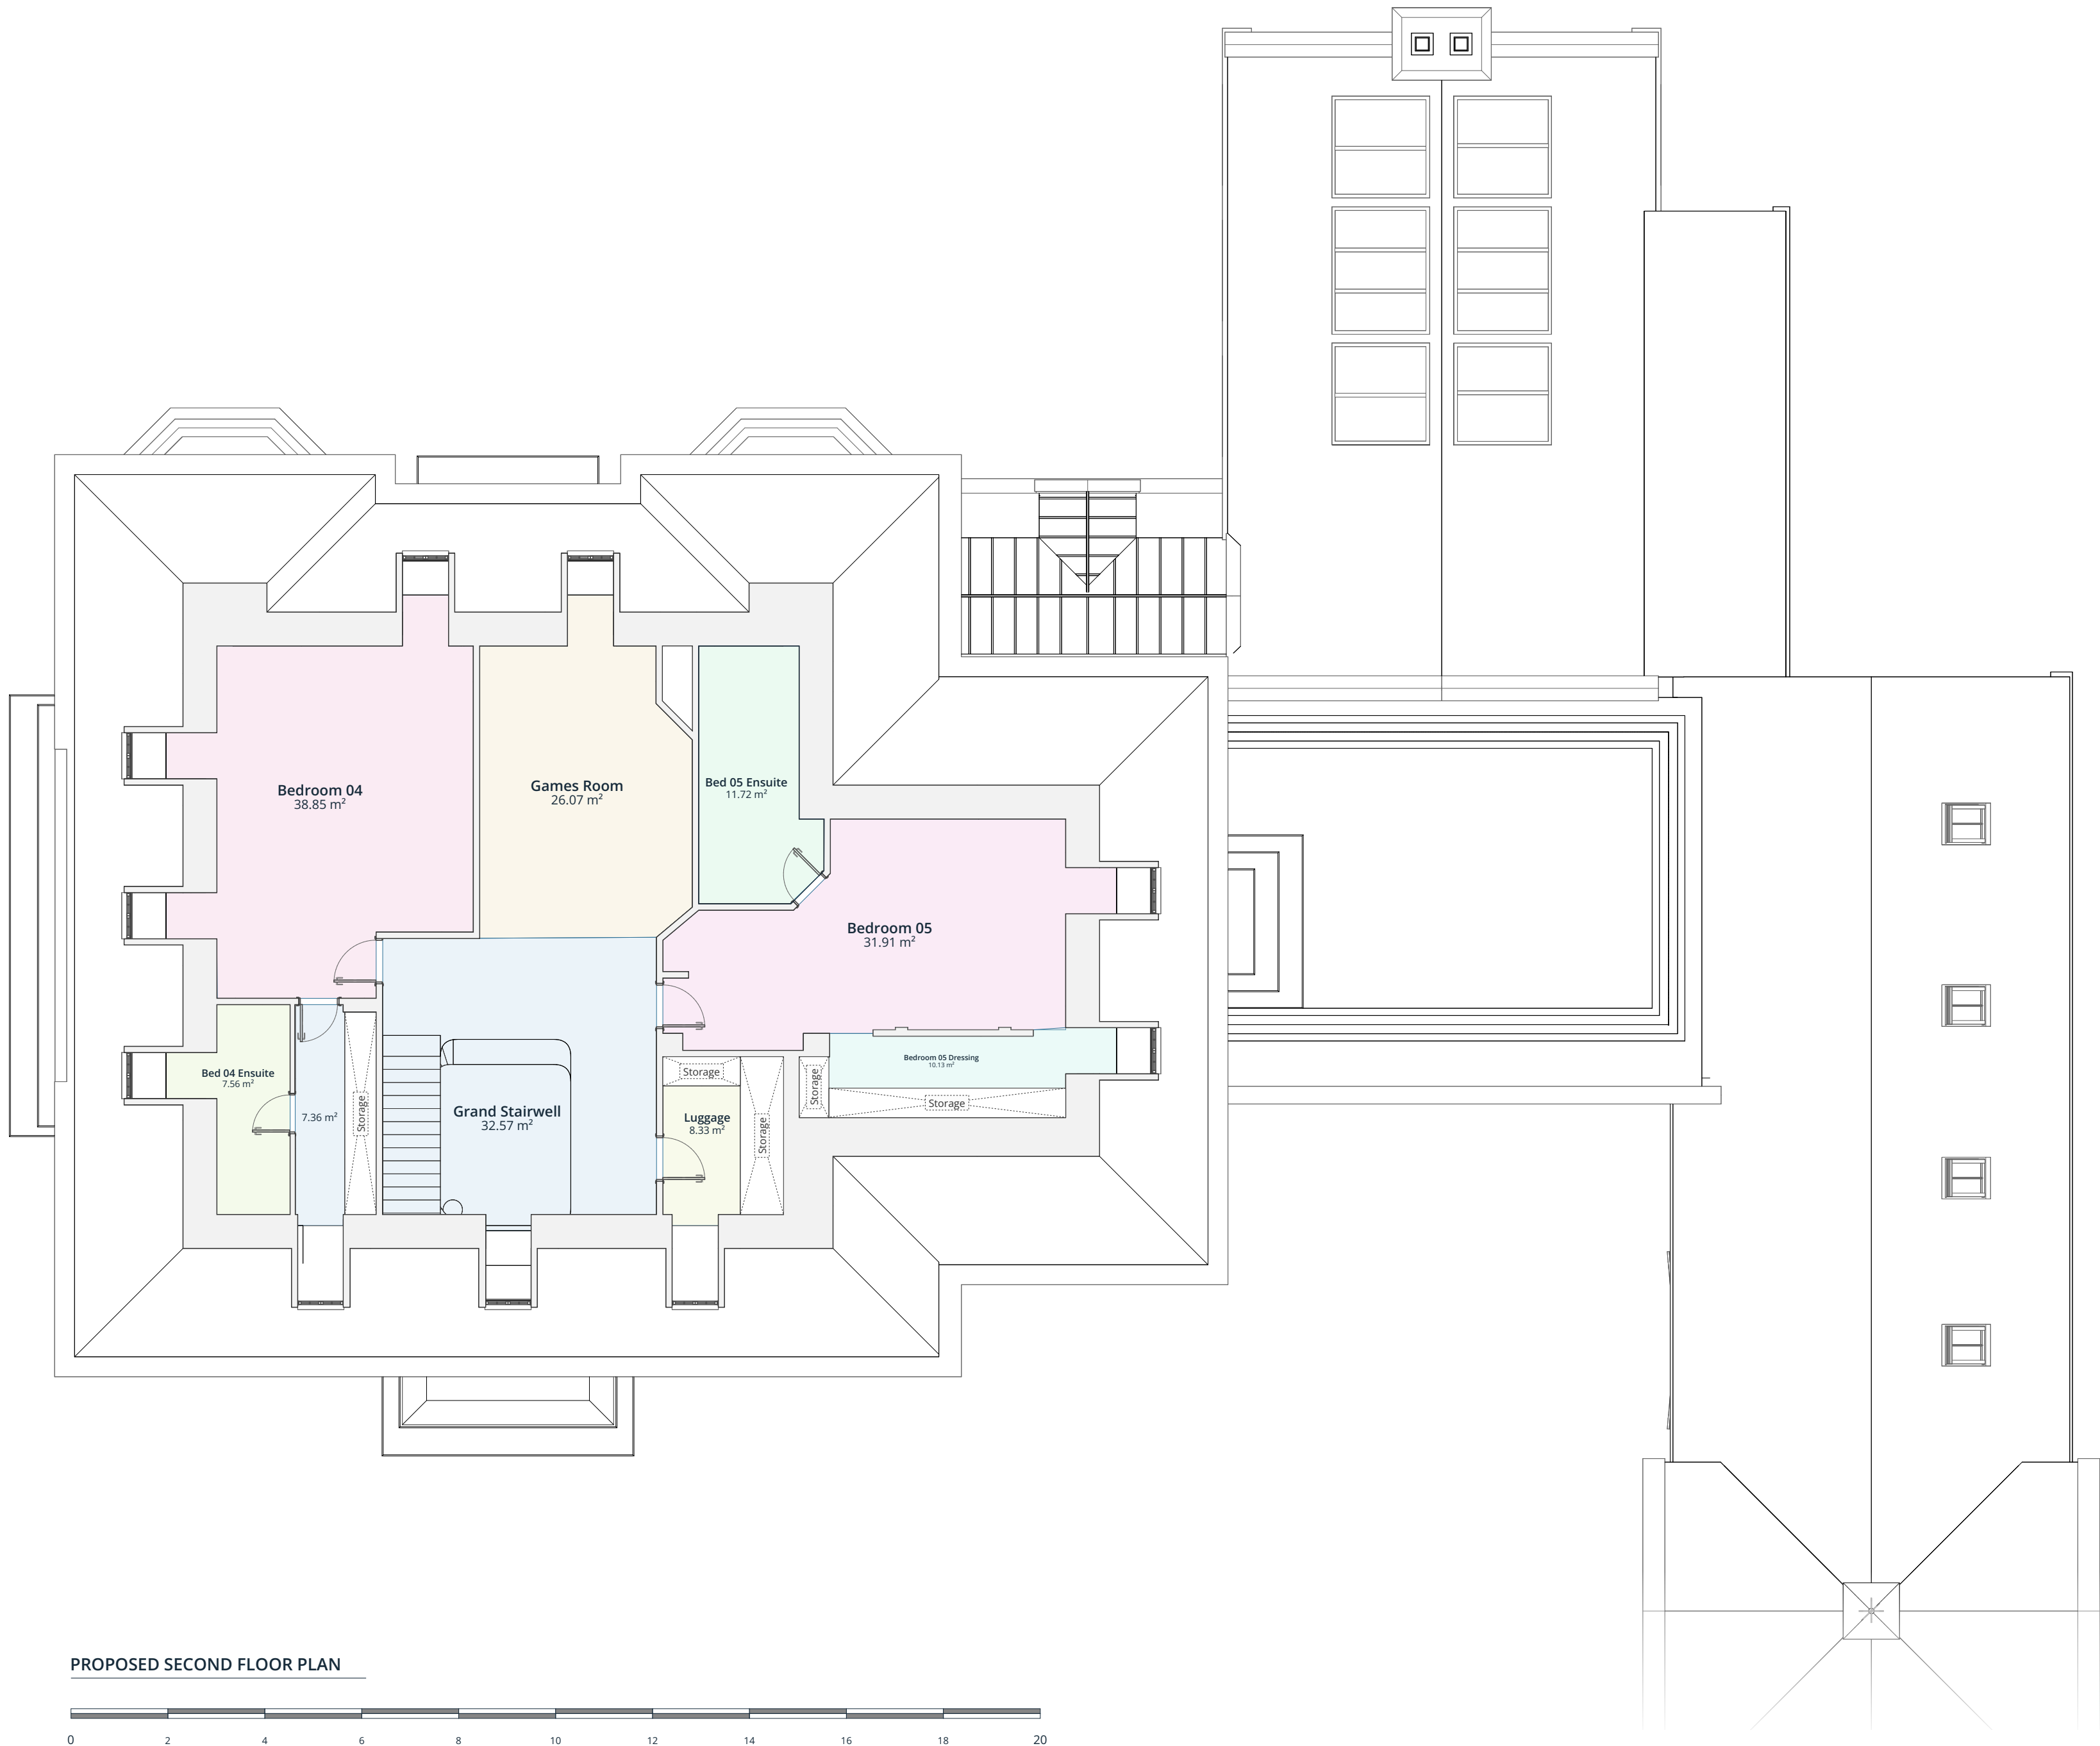

PROPOSED SECOND FLOOR PLAN

NOTES

GN01 | Drawing Scope
Drawings describe the proposed development for planning assessment. They are not construction drawings or a complete Building Regulations specification. Obtain coordinated construction details, structural calculations and Building Control approval before relevant work starts. Refer discrepancies to Noble Architecture before proceeding.

GN02 | Survey And Dimensions
Site information derived from a photogrammetric aerial survey of the holding, with purchased Ordnance Survey data to the site plans. No measured building survey of the existing dwelling has been carried out. Proposed buildings are derived from Noble Architecture's three-dimensional model. Do not scale from these drawings. Verify all dimensions on site.

GN03 | Pre-Application Status
Issued for pre-application advice. Materials, dimensions and levels are indicative at this stage and to be fixed before a planning application.

Floor Areas - Ground Floor

Room	Area
Second Floor - Main House	174.48 m²
Luggage	8.33 m²
Grand Stairwell	32.57 m²
Games Room	26.07 m²
Bed 05 Ensuite	11.72 m²
Bedroom 04	38.85 m²
Bedroom-04 Wardrobe	7.36 m²
Bed 04 Ensuite	7.56 m²
Bedroom 05	31.91 m²
Bedroom 05 Dressing	10.13 m²
Total	174.48 m²

Room	Area
Second Floor - Main House	1,878 ft²
Luggage	90 ft²
Grand Stairwell	351 ft²
Games Room	281 ft²
Bed 05 Ensuite	126 ft²
Bedroom 04	418 ft²
Bedroom-04 Wardrobe	79 ft²
Bed 04 Ensuite	81 ft²
Bedroom 05	343 ft²
Bedroom 05 Dressing	109 ft²
Total	1,878 ft²