



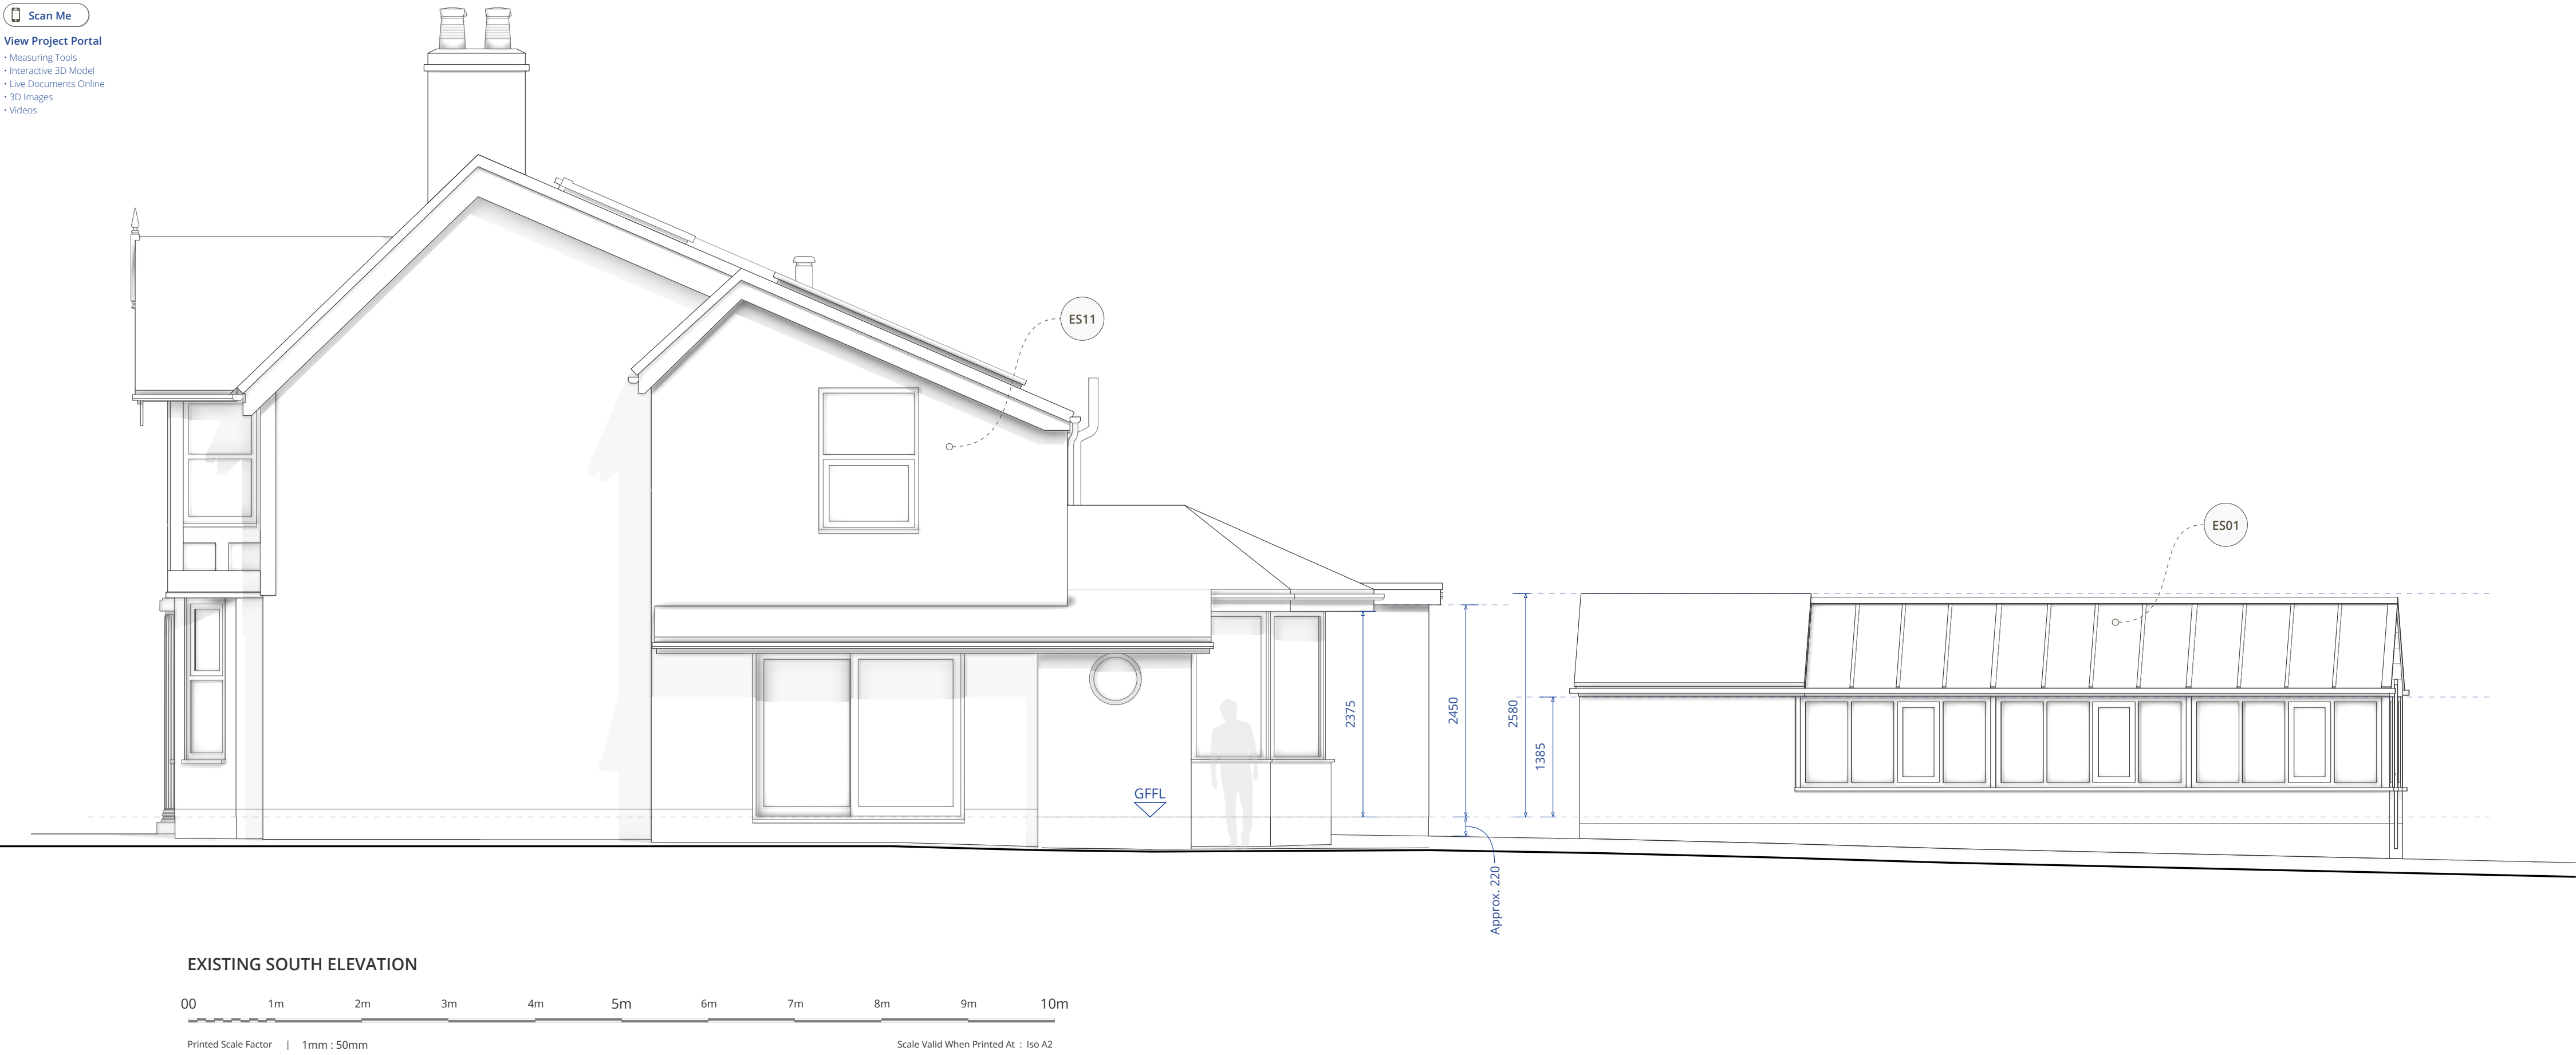

EXISTING CONDITIONS

PROPOSED SCHEME

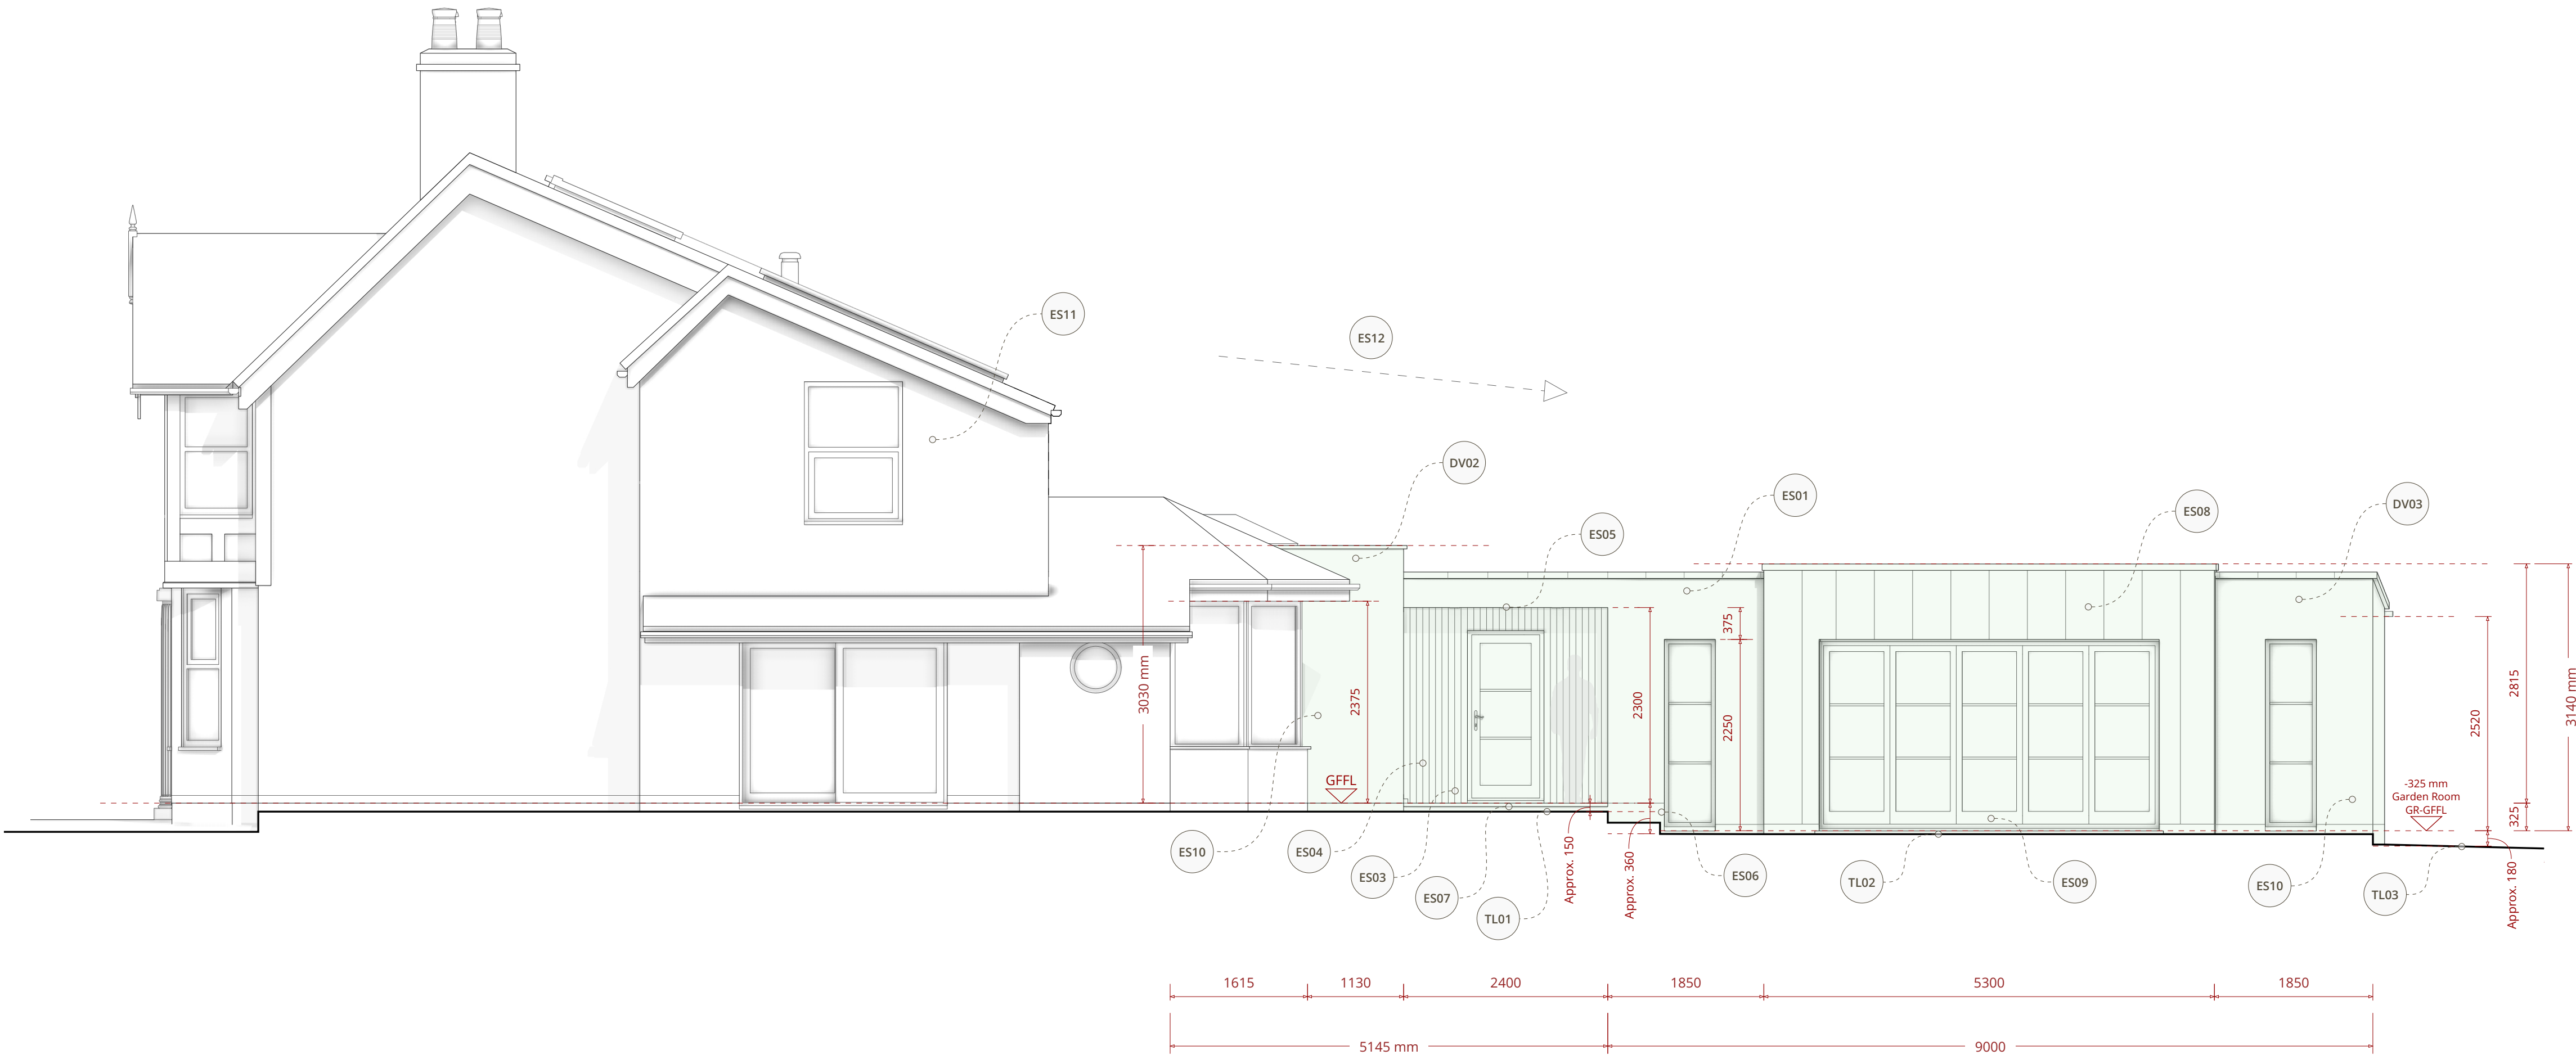

Southern Elevation Design Notes

The south elevation faces the private Paddock Access drive along the southern boundary, with the neighbouring properties of Ashbrook and Lynwood beyond, and it presents the scheme's stepped sequence from the two-storey host dwelling down to the garden room.

ES01 | Replacement Of The Redundant Greenhouse With The Garden Room

The transformative move on this elevation is the replacement of the existing greenhouse. The existing structure is a substantial but derelict single-glazed greenhouse that long ago ceased to serve its horticultural purpose and now functions only as an ineffective store, as set out at Section 1.0 of the Design and Access Statement. It is demolished in its entirety and the new garden room (mass DV03) is constructed on materially the same base, so no previously undeveloped ground is taken. The comparison between the existing and proposed south elevations records the exchange directly: a tired, fully glazed utility structure is replaced by a considered, low and purposeful garden building whose composition is described at note ES02. This re-use of an existing developed footprint is central to the Green Belt case at Section 10.0 of the Design and Access Statement.

ES02 | Garden Room South Composition And Materials

The garden room presents a calm tripartite composition to the south. Its central section is finished in dark, almost black, standing seam metal and contains a large glazed screen; the flanking sections are finished in through-coloured monocouche render, each carrying a single slim window. All frames are black in accordance with the contemporary rear palette tabled at Section 5.2.2 of the Design and Access Statement. The parapet-concealed roof steps with the composition, and the whole structure is set down from the main floor level with reduced eaves and door heights, following the falling ground, so that it reads as the lowest and most deferential mass of the scheme. Every opening on this face is single-storey and at ground level behind the established southern boundary treatment, so no privacy issue arises, as set out at Section 7.0 of the Design and Access Statement.

ES03 | Sunken Inset Porch And Secondary Entrance

The new secondary entrance sits within a sunken inset porch recessed between the rear extension and the garden room. The recess gives the doorway genuine shelter and presence within the composition, and the porch takes everyday comings and goings away from the formal principal entrance on the front elevation, linking logically down to the parking area. The individual components of the porch are recorded at notes ES04 to ES07.

ES04 | Vertical Timber Slatted Porch Lining

The porch recess is lined in vertical washed light oak slatted panelling. The timber lining gives the entrance warmth and texture against the surrounding render and standing seam metal, and it marks the doorway clearly within the elevation without recourse to any competing architectural feature.

ES05 | Concealed Soffit Lighting To The Porch

The recessed soffit of the porch carries concealed overhead lighting, so that after dark the entrance reads as a softly glowing timber-lined threshold rather than a dark void. Fitting positions are to be finalised at fit-out and all electrical work must be designed and installed in full compliance with current Building Regulations.

ES06 | Step Up Through The Porch

The step up through the porch into the house forms part of the deliberate freeboard sequence in which each external rise adds protection between external ground level and the internal floor level, as described at Section 9.3 of the Design and Access Statement and recorded at notes DR03 and TL01.

ES07 | Threshold Channel Drain To The Porch

A co-slot channel drain runs across the porch threshold, intercepting surface water before it can pond against the doorway and conveying it to the buried lateral soakaway network beneath the planting beds, in accordance with notes DR01 and DR02.

ES08 | Dark Standing Seam Metal Cladding

The central section of the garden room is finished in dark, almost black, standing seam metal carried across both its walls and its roof. The material has been deliberately selected to detach the garden room visually from the white rendered house and rear extension, so that it reads as its own quiet structure within the garden in the manner of the outbuildings that characterise the local grain (note DV03 and Section 4.4 of the Design and Access Statement). The vertical seams lend the surface a fine, consistent rhythm with entirely concealed fixings, and the system is a high quality, durable and low maintenance finish appropriate to a garden building of this standing.

ES09 | Black Framed Glazed Folding Doors

The garden room opens through a wide set of glazed folding doors framed in black aluminium, carrying the same horizontal glazing bar rhythm used consistently across the rear facing elevations. The doors connect the entertaining space directly to the terraces, and their black frames tie the garden room to the wider rear palette of black-framed windows and doors tabled at Section 5.2.2 of the Design and Access Statement. The opening is carried on beam BM04 in accordance with note ST04.

ES10 | Monocouche Render To The New Walls

Read from the south the proposal presents its full stepped silhouette in a single view: the two-storey host dwelling stands tallest, the parapet of the single-storey rear extension and its link sits well below it; the timber-lined porch recesses further, and the garden room, set down with the falling ground, finishes lowest of all. Each successive mass is lower and quieter than the last, so the composition tapers gently into the garden rather than presenting any abrupt or competing bulk. This is the massing hierarchy of Section 6.0 of the Design and Access Statement seen in elevation, and it ensures the scheme reads as subordinate, layered evolution from every southern viewpoint.

ES11 | Retained Host Dwelling And Unchanged Southern Outlook

No alterations are made to the south-facing fabric of the host dwelling itself. The existing gables, the first-floor window, the ground-floor openings including the distinctive circular porthole window, and the flank of the retained bay all remain exactly as existing. Crucially, no new first-floor side-facing windows are introduced anywhere on this elevation. That option was actively considered during the design process and was rejected on the advice of both the architect and the planning consultant, so the outlook towards the neighbouring properties to the south is entirely unchanged, as set out in full at Section 7.0 of the Design and Access Statement.

ES12 | The Stepped Silhouette Read From The South

Read from the south the proposal presents its full stepped silhouette in a single view: the two-storey host dwelling stands tallest; the parapet of the single-storey rear extension and its link sits well below it; the timber-lined porch recesses further; and the garden room, set down with the falling ground, finishes lowest of all. Each successive mass is lower and quieter than the last, so the composition tapers gently into the garden rather than presenting any abrupt or competing bulk. This is the massing hierarchy of Section 6.0 of the Design and Access Statement seen in elevation, and it ensures the scheme reads as subordinate, layered evolution from every southern viewpoint.

General Note | Planning Purpose Only

This document and the associated drawing pack have been prepared explicitly and exclusively for the purpose of a statutory householder planning application. To ensure absolute clarity for the local planning authority assessing the scheme the document pack is intentionally lightweight. It deliberately omits detailed technical specifications including structural arrangements wall compositions thermal insulation details and floor or roof build ups. Consequently these documents are strictly not fit for construction purposes procurement or Building Regulations approval. Comprehensive technical design and structural engineering plans must be commissioned and approved at a subsequent stage prior to the commencement of any physical works.