




13000
Existing Dwelling Building Width

Existing East Elevation – Dwelling Frontage

00 02 04 06 08 10

Printed Scale Factor | 1mm : 100mm | Scale Valid When Printed At : ISO 216 A2

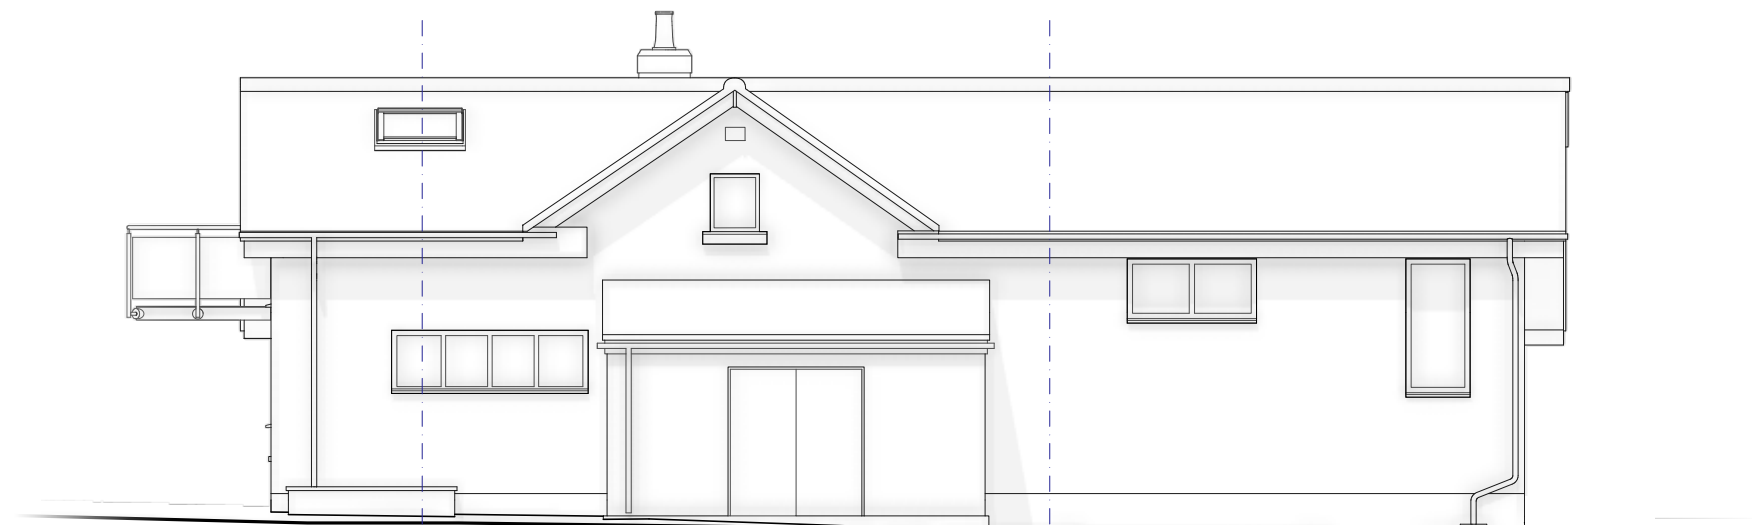


8300
Existing Dwelling Building Depth

Existing North Elevation – Side Of Dwelling

00 02 04 06 08 10

Printed Scale Factor | 1mm : 100mm | Scale Valid When Printed At : ISO 216 A2

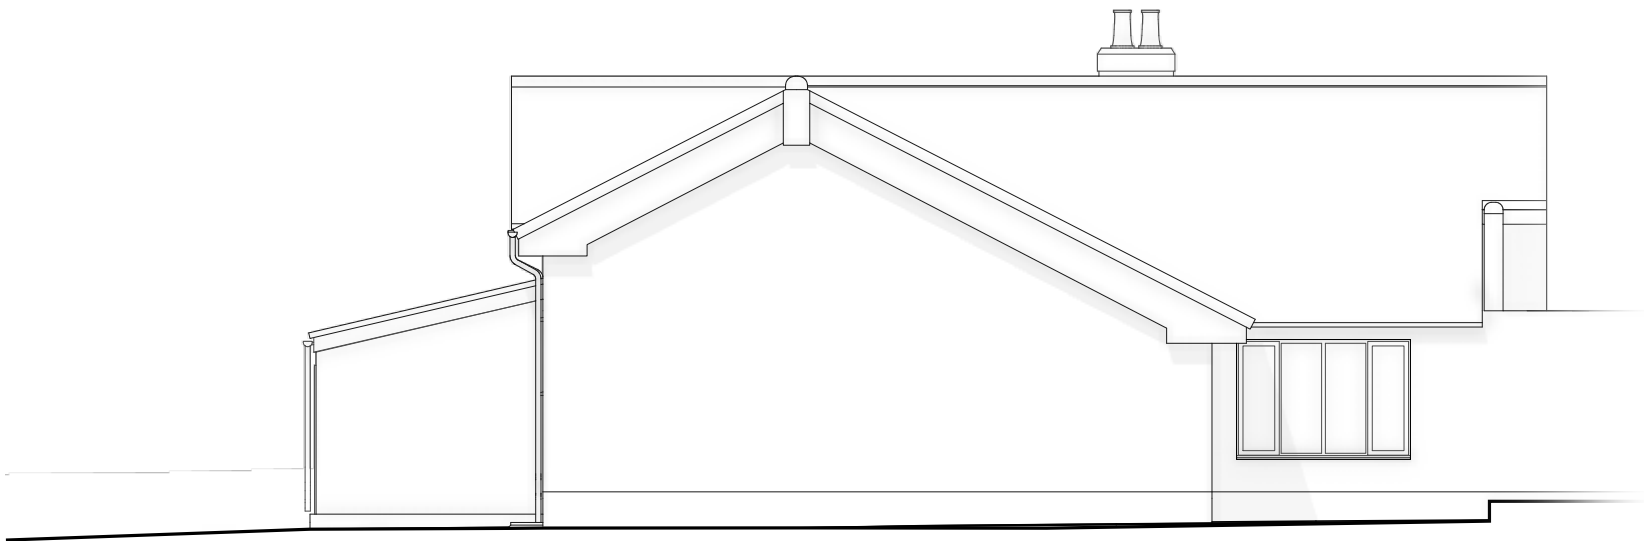

Existing West Elevation – Rear Of Dwelling

00 02 04 06 08 10

Printed Scale Factor | 1mm : 100mm | Scale Valid When Printed At : ISO 216 A2

PRELIMINARY DRAWING:

This plan provides a preliminary outline of the proposed scheme and is not intended for construction use. It is designed for planning officials and early stage project tendering only. Before issuing final construction drawings, further design coordination with specialists is required. Using this plan for construction is at the user's risk with no guarantees regarding its accuracy or completeness. Noble Architecture or any affiliated parties are not liable for any errors or discrepancies. By using this document for construction, the user agrees to indemnify all involved parties against claims or damages stemming from its use.

PLANNING DEPARTMENT

Existing Site Context Photographs

Noble Architecture has compiled a comprehensive collection of site survey images, including drone photography, which are available upon request. Should these be of assistance, please reach out to Noble Architecture directly.




13000 Existing Dwelling Building Width
6500 Extension Proposal Width
3000 Extension Brickwork To Match Host Dwelling

Proposed East Elevation – Dwelling Frontage & Front Of Extension

00 02 04 06 08 10

Printed Scale Factor | 1mm : 100mm | Scale Valid When Printed At : ISO 216 A2

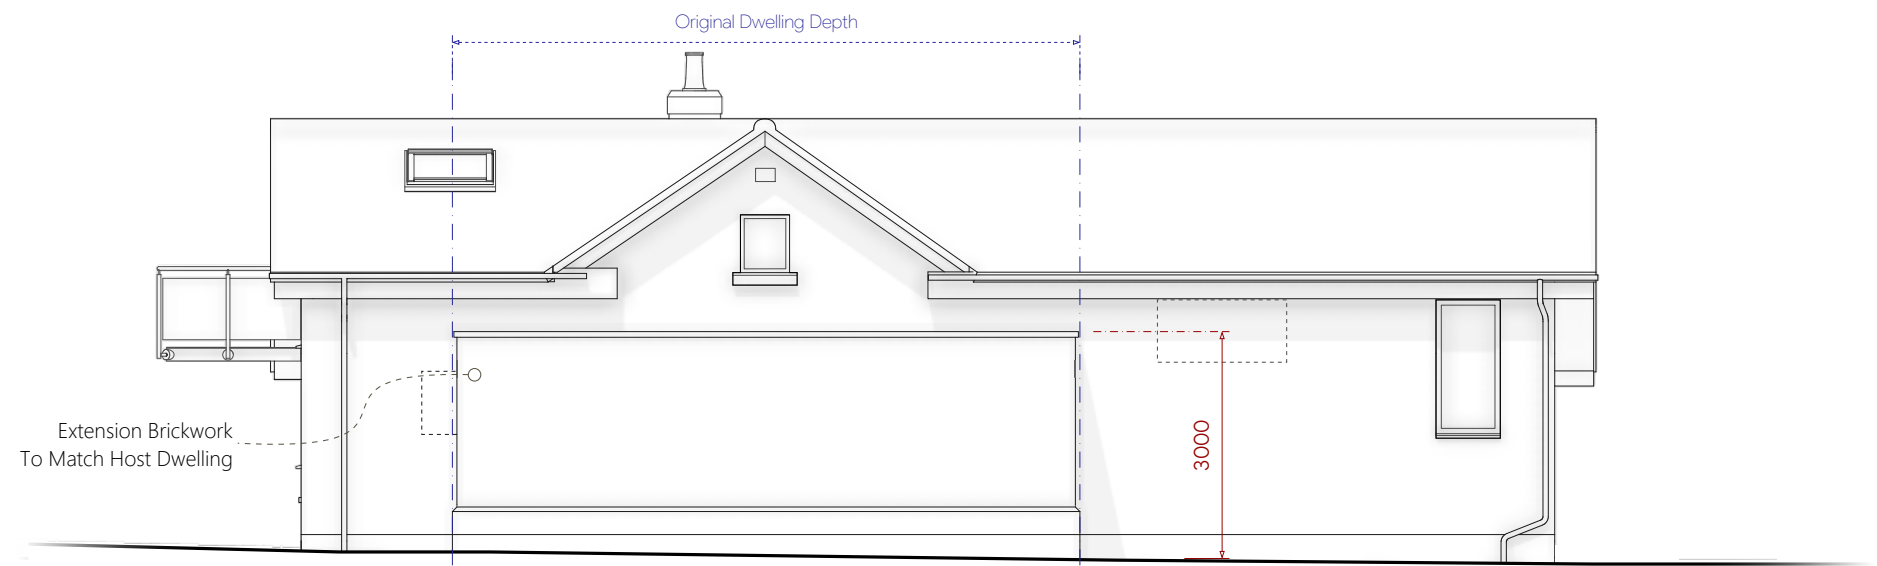


1980 8300 6300
Extension Proposal Depth

Proposed North Elevation – Side View Of Dwelling & Extension

00 02 04 06 08 10

Printed Scale Factor | 1mm : 100mm | Scale Valid When Printed At : ISO 216 A2

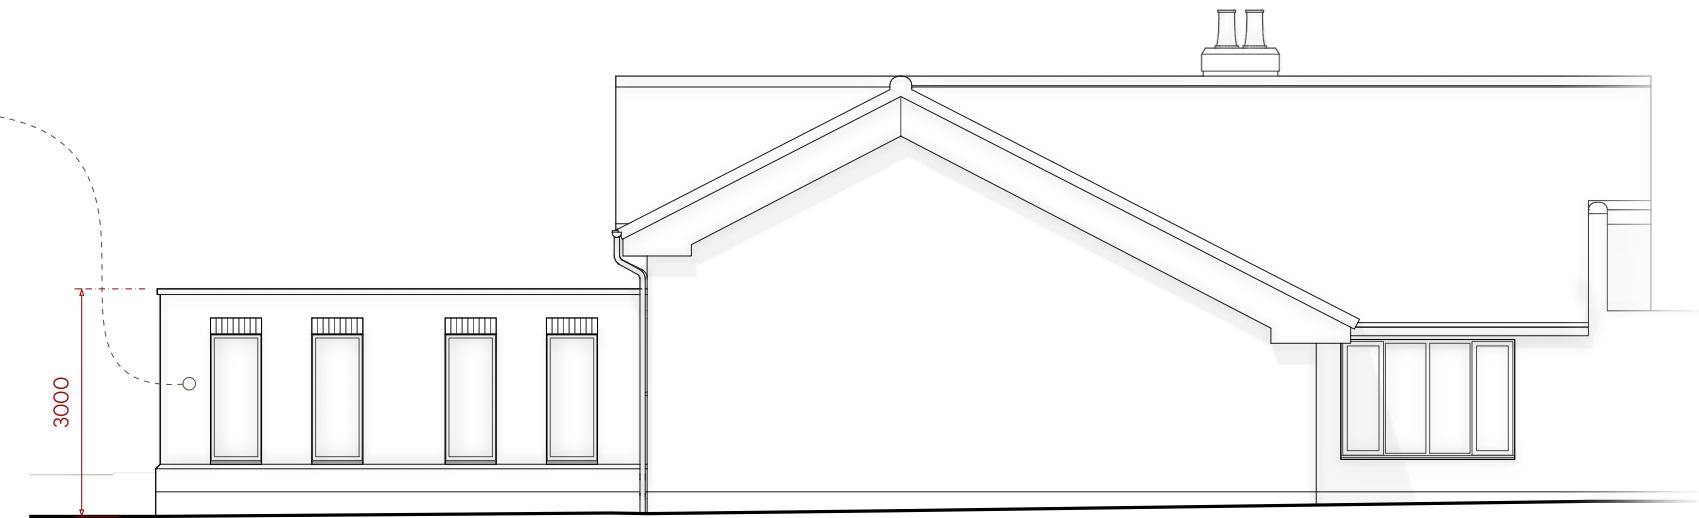

6500
Extension Proposal Width

Proposed West Elevation – Rear View Of Dwelling & Extension

00 02 04 06 08 10

Printed Scale Factor | 1mm : 100mm | Scale Valid When Printed At : ISO 216 A2

CONTRACTOR

Ensuring Material Consistency

The contractor is required to carefully match new materials to the existing structure, ensuring an exact match in colour, material, and texture is achieved.