





Scan Me

View Project Portal

- Measuring Tools
- Interactive 3D Model
- Live Documents Online
- 3D Images
- Videos



EXISTING NORTH ELEVATION

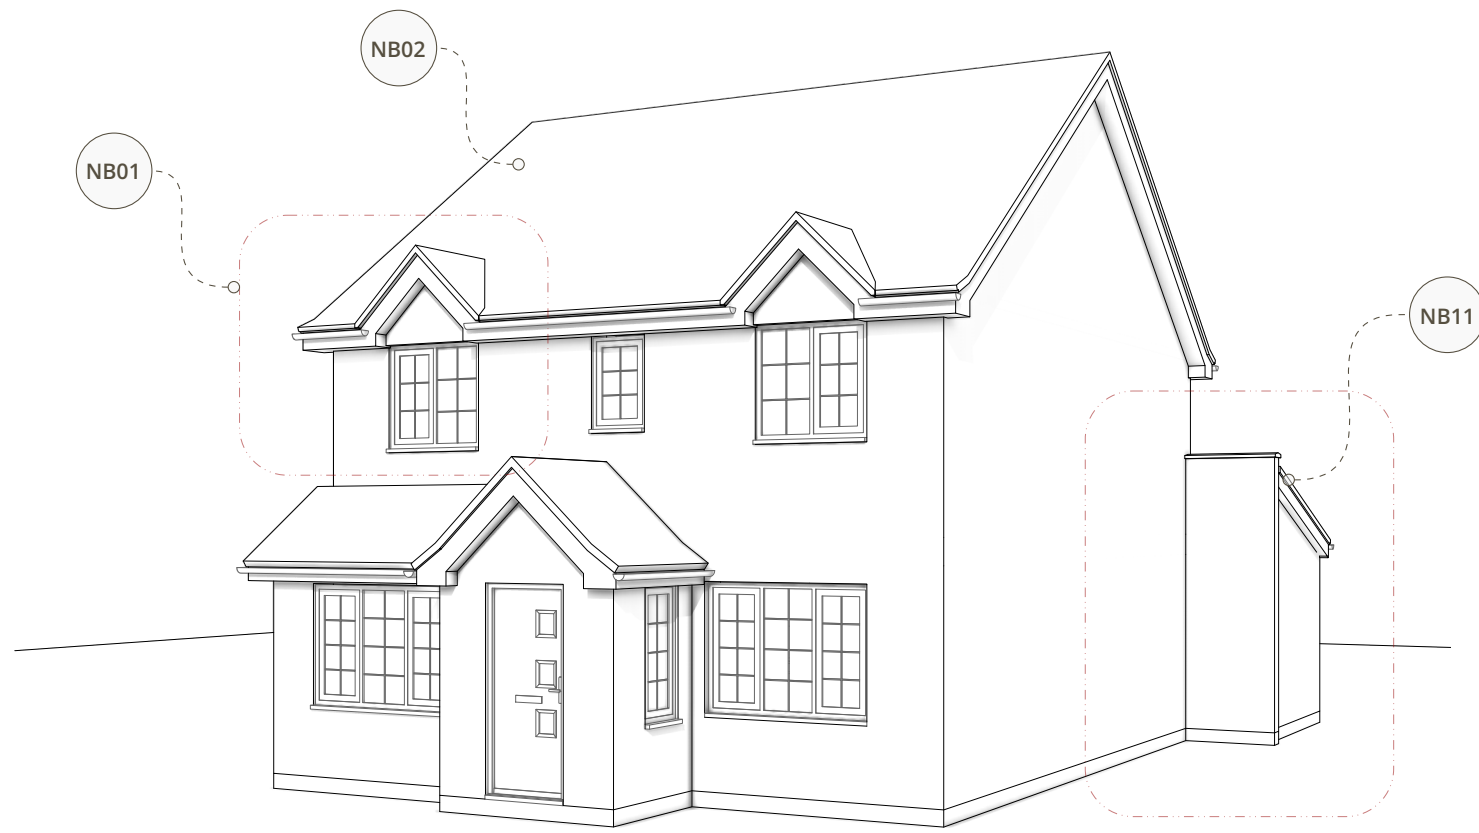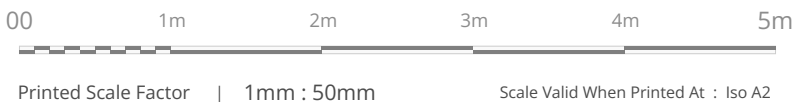


EXISTING NORTHERN FACING FACADE

EXISTING CONDITIONS



PROPOSED NORTH ELEVATION

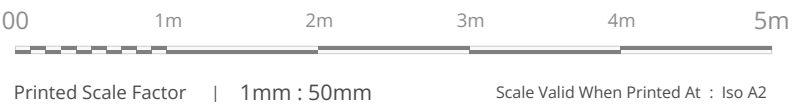

PROPOSED NORTHERN FACING FACADE

NB01 | Front Facing Dormer Windows

Careful attention has been paid to the front elevation to ensure the proposed loft conversion seamlessly integrates with the established character of the property and the wider estate. The original front elevation is characterised by distinct front-facing eaves gables, a defining architectural motif that is prevalent on properties throughout the surrounding estate. To respect and reflect this local vernacular, the proposed pitched-roof dormers have been specifically designed to echo the scale, roof pitch, and visual language of these original gablet features. Furthermore, the new dormer windows utilise the exact same cottage bar style glazing present on the existing dwelling. This ensures strict visual consistency, remaining faithful to both the original house and the established aesthetic of the wider estate. By successfully translating these defining characteristics to the new roof level, the proposed dormers harmonise directly with the host dwelling and maintain the cohesive rhythm of the street scene, ensuring the loft conversion reads as a natural, sympathetic evolution of the original architecture.

NB02 | Roof Replacement

To secure the necessary internal head height and usable floor area for the loft conversion, the proposal features a new crown roof. The current roof structure utilises restrictive fink-style trusses, meaning a complete roof replacement is fundamentally required. A traditional apex roof was discounted as it would raise the ridge to an unacceptable height. As evidenced by the drone imagery in the Design and Access Statement, the neighbouring property at No. 9 occupies an elevated topographical position with a significantly steeper, taller roof structure, establishing a clear precedent for a higher permissible ridge line on Ashness Close. Despite this precedent, the applicant consciously opted to cap the proposed ridge height by flattening the apex into a crown design. While a more financially intensive structural solution, this approach successfully mimics a traditional pitched roof from the principal front and rear elevations, remaining faithful to the original roof pitch and rigorously protecting the established character of the street scene.

The contractor is responsible for all technical roof design and coordinating the scheme with an attic truss manufacturer (e.g., Trusstec or similar). All insulation, vapour control, and structural elements must be designed and specified in full compliance with current Building Regulations

General Notes | Planning Purpose Only Package

This document and the associated drawing pack have been prepared explicitly and exclusively for the purpose of a statutory householder planning application. To ensure absolute clarity for the local planning authority assessing the scheme the document pack is intentionally lightweight. It deliberately omits detailed technical specifications including structural arrangements wall compositions thermal insulation details and floor or roof build ups. Consequently these documents are strictly not fit for construction purposes procurement or Building Regulations approval. Comprehensive technical design and structural engineering plans must be commissioned and approved at a subsequent stage prior to the commencement of any physical works.

Contractor Responsibilities & Verification

The appointed building contractor is solely responsible for verifying all dimensions site levels and existing boundary conditions prior to the commencement of any fabrication ordering of materials or construction works. Any discrepancies found between these preliminary planning drawings and the physical site must be reported immediately to Noble Architecture and the client. The contractor must not scale directly from these drawings for construction purposes. The appointed principal contractor assumes full responsibility for ensuring all executed works comply strictly with current Building Regulations local authority requirements and all relevant health and safety legislation.

Limitation Of Liability And Indemnity

Noble Architecture shall not be held liable for any direct indirect or consequential loss injury or damage arising from the unauthorised use of these drawings for any purpose other than obtaining town and country planning permission. The client and any subsequently appointed contractors fully indemnify Noble Architecture against any claims financial costs or legal liabilities resulting from the misuse of these drawings for construction pricing structural implementation or Building Control submissions. By proceeding with the project beyond the planning phase the client formally acknowledges the necessity of engaging appropriate technical professionals for the detailed construction phase.

Copyright And Intellectual Property

All designs architectural drawings written specifications and intellectual property contained within this document remain the exclusive statutory property of Noble Architecture. These documents may not be reproduced altered or distributed to third parties for any purpose other than the specific planning application at the application site without the express written consent from Noble Architecture.