



Scan Me

View Project Portal


- Measuring Tools
- Interactive 3D Model
- Live Documents Online
- 3D Images
- Videos



EXISTING SOUTH ELEVATION


00 1m 2m 3m 4m 5m

Printed Scale Factor | 1mm : 50mm Scale Valid When Printed At : Iso A2

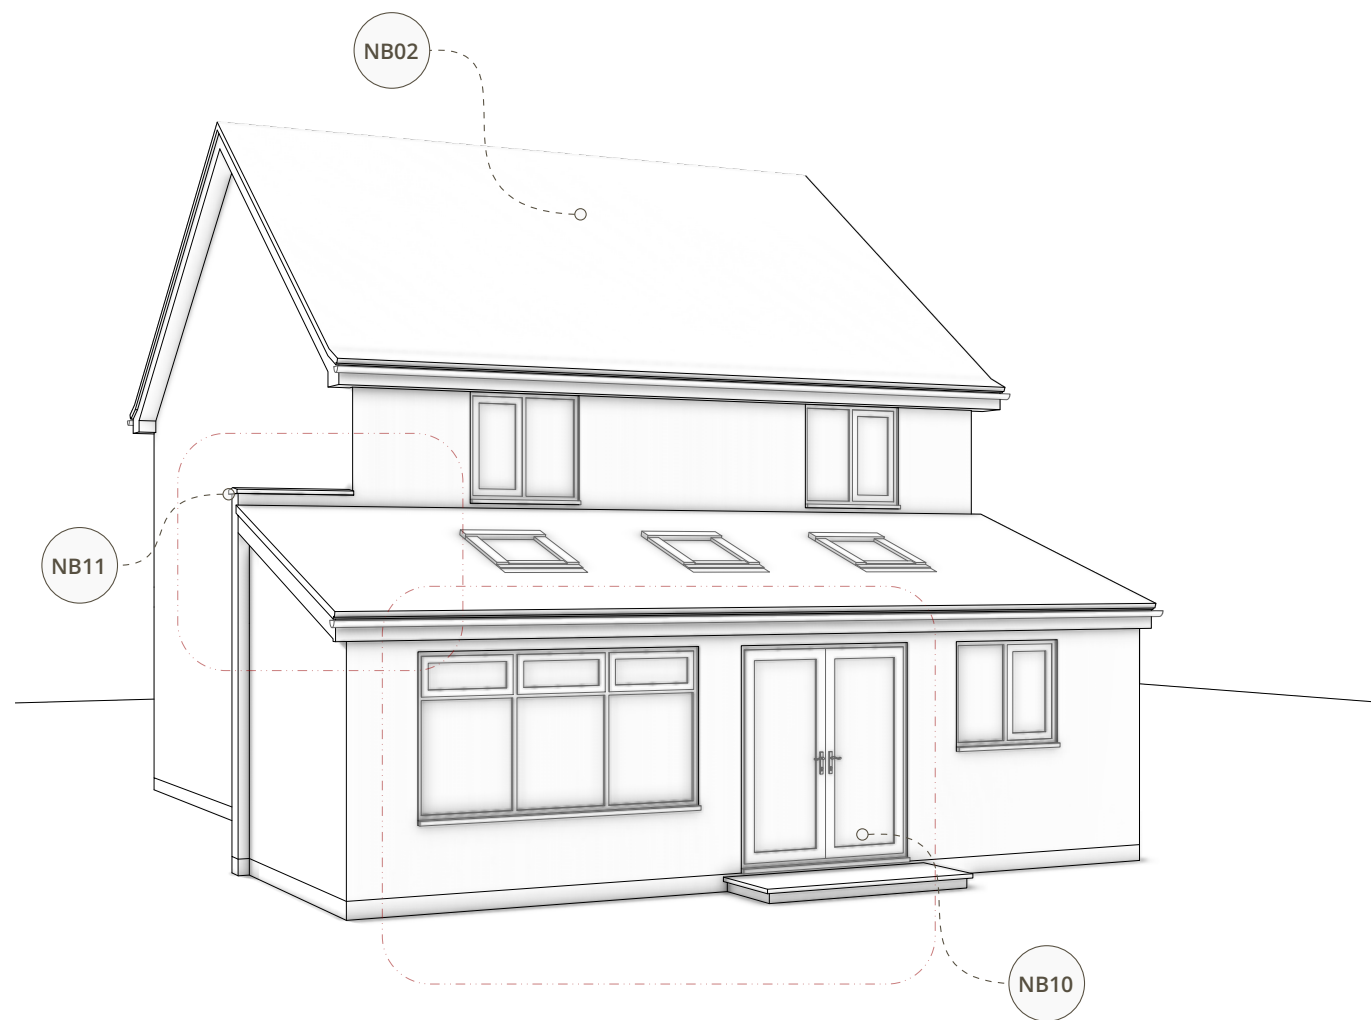

EXISTING SOUTHERN FACING FACADE


PROPOSED SCHEME

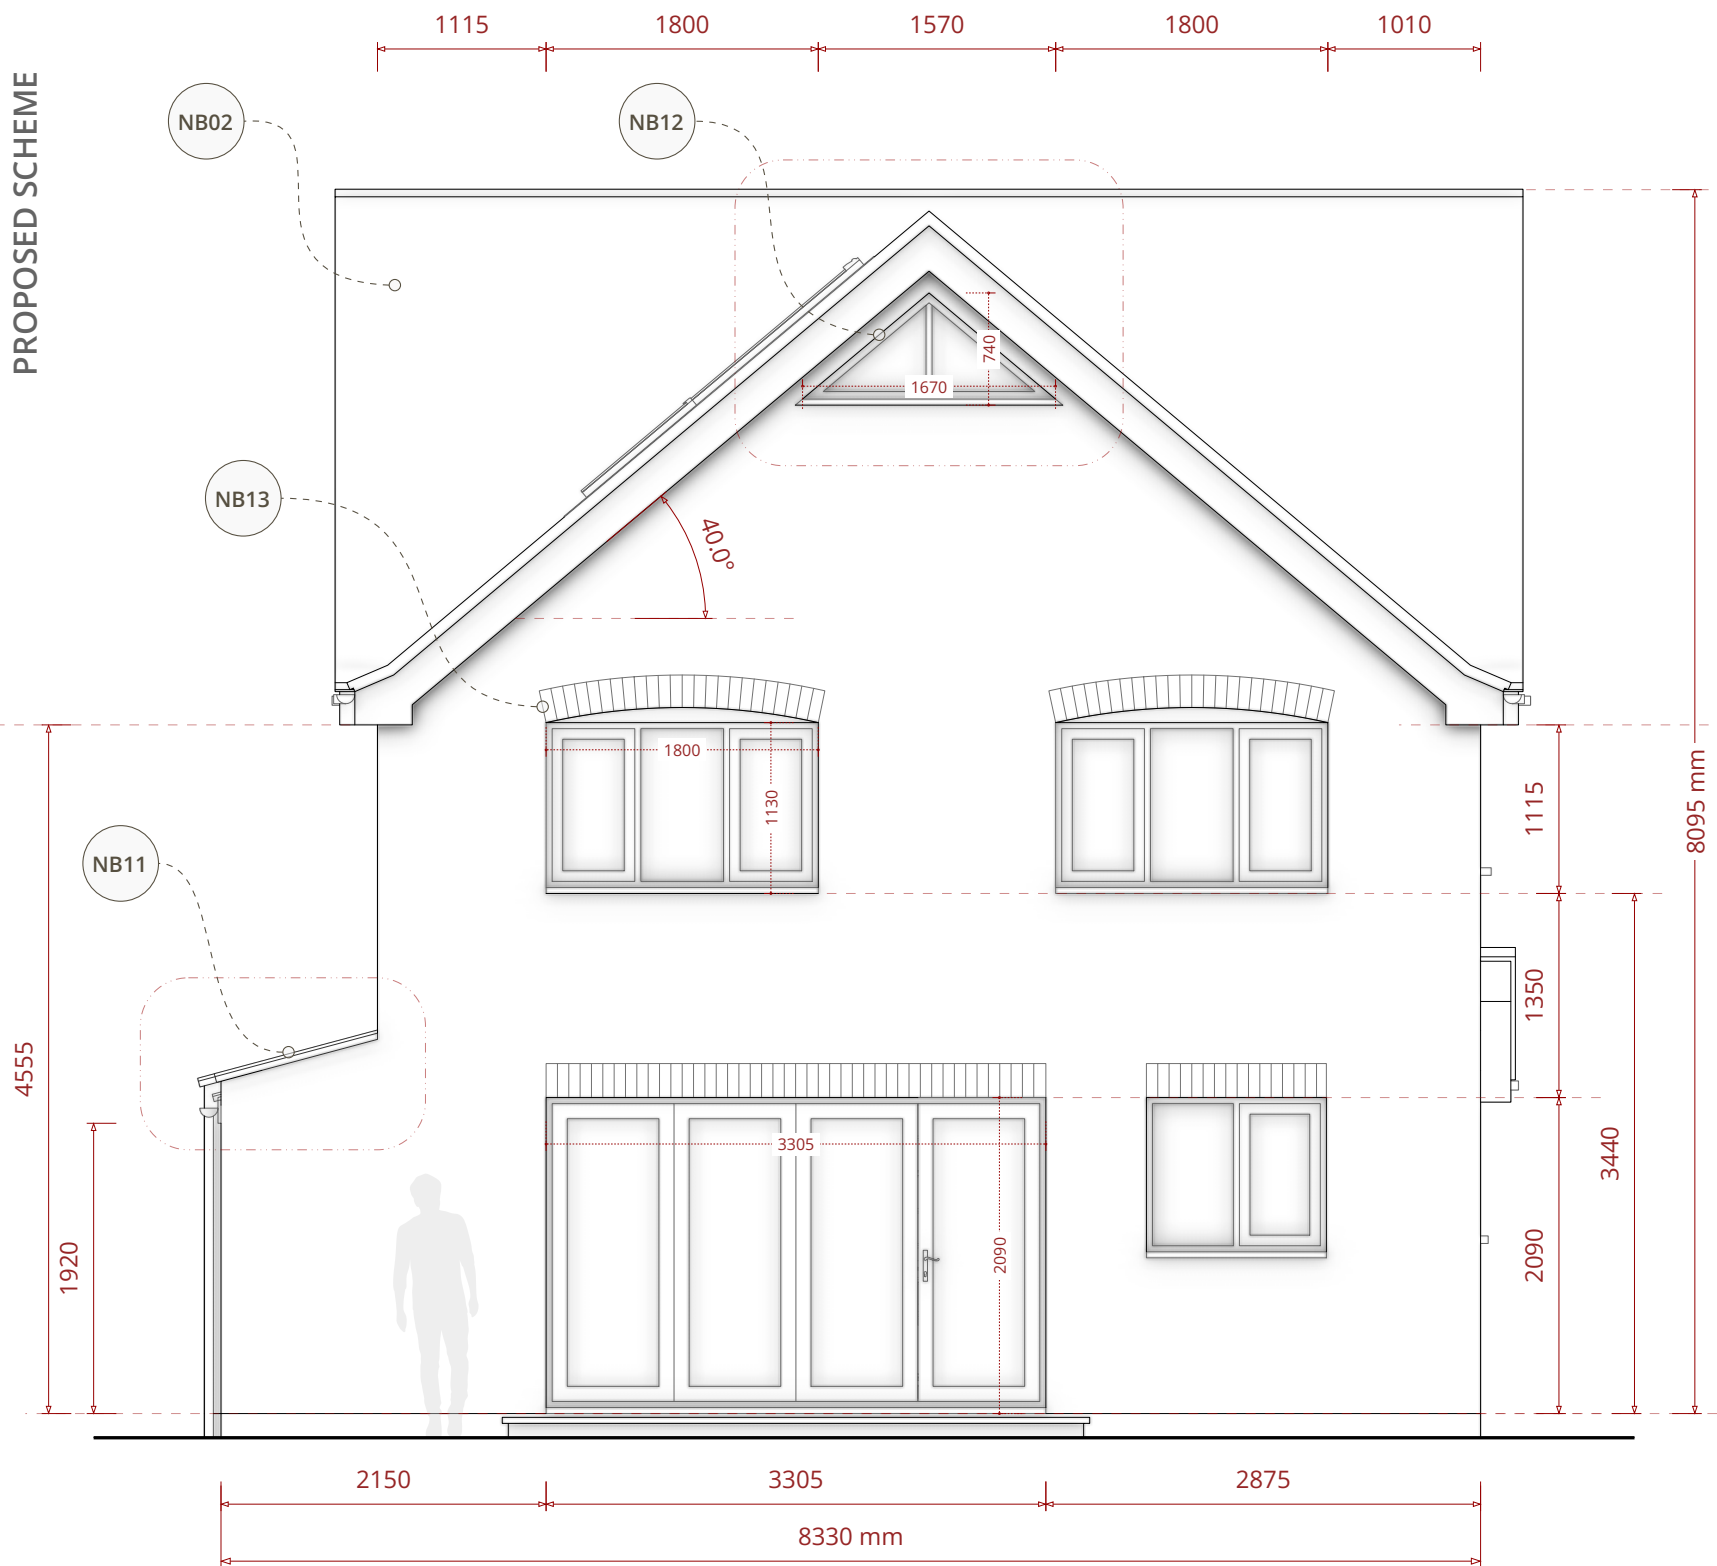

PROPOSED SOUTH ELEVATION

00 1m 2m 3m 4m 5m

Printed Scale Factor | 1mm : 50mm Scale Valid When Printed At : Iso A2

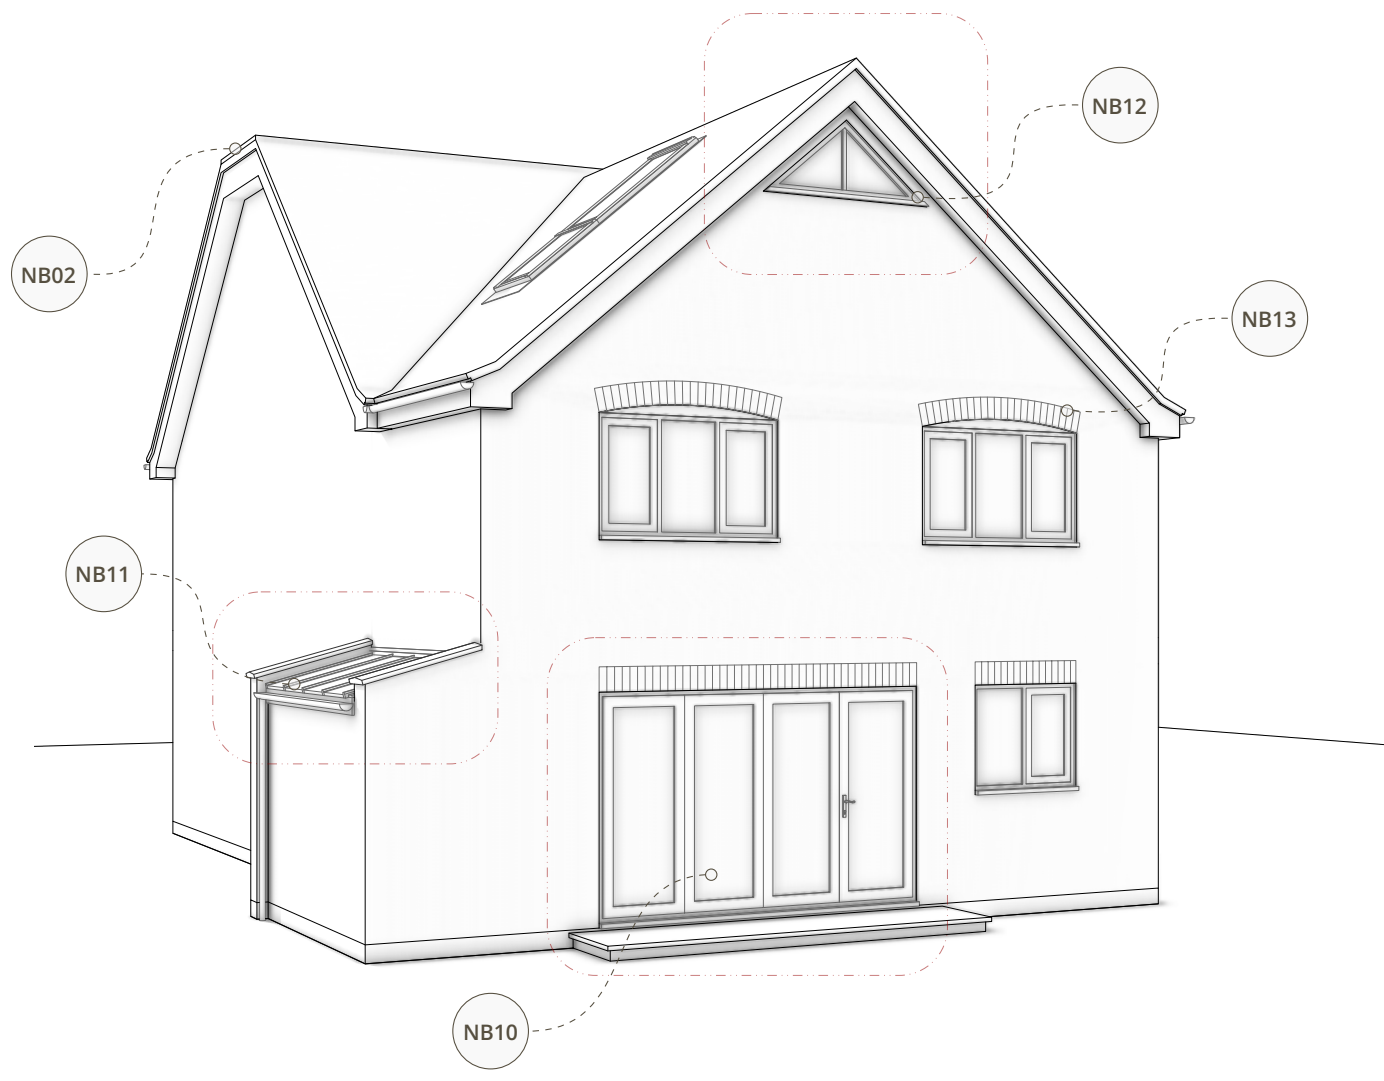

PROPOSED SOUTHERN FACING FACADE

NB10 | Rear Door Opening Alterations

The proposal removes the existing large window, wall nib, and rear patio doors to form a single, enlarged structural opening. The aim is to better align the window reveals, rectifying the previous extension where openings were added ad hoc without thought for rhythm. A new four-panel folding door system will be installed, featuring a master door for routine garden access and three folding panels to create a seamless transition between the kitchen and garden when required. The new structural opening requires a steel beam; load-bearing specifications must be certified by a qualified structural engineer and comply with all required Building Regulations prior to construction.

NB11 | Roof Replacement and New Glazed Roof Section

The addition of the first-floor extension over the main body of the existing rear extension leaves a narrow, residual section of the ground-floor footprint. Retaining the existing roof arrangement here would result in an awkward and visually unresolved slender mono-pitched element. The existing structure currently relies on a disproportionately large and visually intrusive parapet wall on the side elevation which is an unsympathetic historical addition that relates poorly to the original character of the host dwelling.

To resolve these architectural issues, the proposal includes replacing this residual roof section with a newly configured pitched glazed roof. By reorienting the roof pitch to span the shorter dimension, the proposal facilitates a dramatic reduction in the height and massing of the bulky parapet wall. This crucial alteration removes a visually jarring element, returning the side elevation to a much more subservient and sympathetic appearance.

Crucially, introducing this new glazed roof section allows us to entirely reorganise the rear elevation. The original rear facade is visually disjointed and poorly composed, featuring mismatched window and door sizes that fail to align with one another. By utilising the new roof glazing to harvest abundant natural light, we gained the design freedom to reposition the existing ground-floor doors and windows. This rearrangement results in a substantially more balanced and aesthetically pleasing rear elevation, where the south facing doors & windows now align cohesively.

NB12 | Rear Facing Obscured Glass Window

To protect the privacy amenity of neighbouring properties, a conscious and strategic design decision was made regarding the glazing position and extent on the south-facing rear elevation of the new loft space. Rather than introducing a large, clear-glazed window that could facilitate unacceptable overlooking, our proposal incorporates a single, high-level window situated within the gable apex to serve the new en-suite bathroom.

This window will be fitted with obscure glazing and positioned with a sill height exceeding 1.7 meters above the internal floor level, strictly adhering to established planning guidance for privacy protection. This considerate approach ensures the en-suite benefits from essential natural daylight while entirely mitigating any perceived or actual risk of overlooking and loss of privacy for adjacent occupiers.

NB13 | Decorative Brick Embellishment

The proposed rear elevation features segmented brick arches above the new first floor window openings and brick soldier courses over the ground floor openings. These specific architectural details have been deliberately introduced to provide necessary ornamentation to what would otherwise be a plain and drab facade. These motifs are entirely in keeping with the established architectural style prevalent throughout the surrounding estate.

General Note | Planning Purpose Only

This document and the associated drawing pack have been prepared explicitly and exclusively for the purpose of a statutory householder planning application. To ensure absolute clarity for the local planning authority assessing the scheme the document pack is intentionally lightweight. It deliberately omits detailed technical specifications including structural arrangements wall compositions thermal insulation details and floor or roof build ups. Consequently these documents are strictly not fit for construction purposes procurement or Building Regulations approval. Comprehensive technical design and structural engineering plans must be commissioned and approved at a subsequent stage prior to the commencement of any physical works.