





Scan Me


- View Project Portal
- Measuring Tools
 - Interactive 3D Model
 - Live Documents Online
 - 3D Images
 - Videos

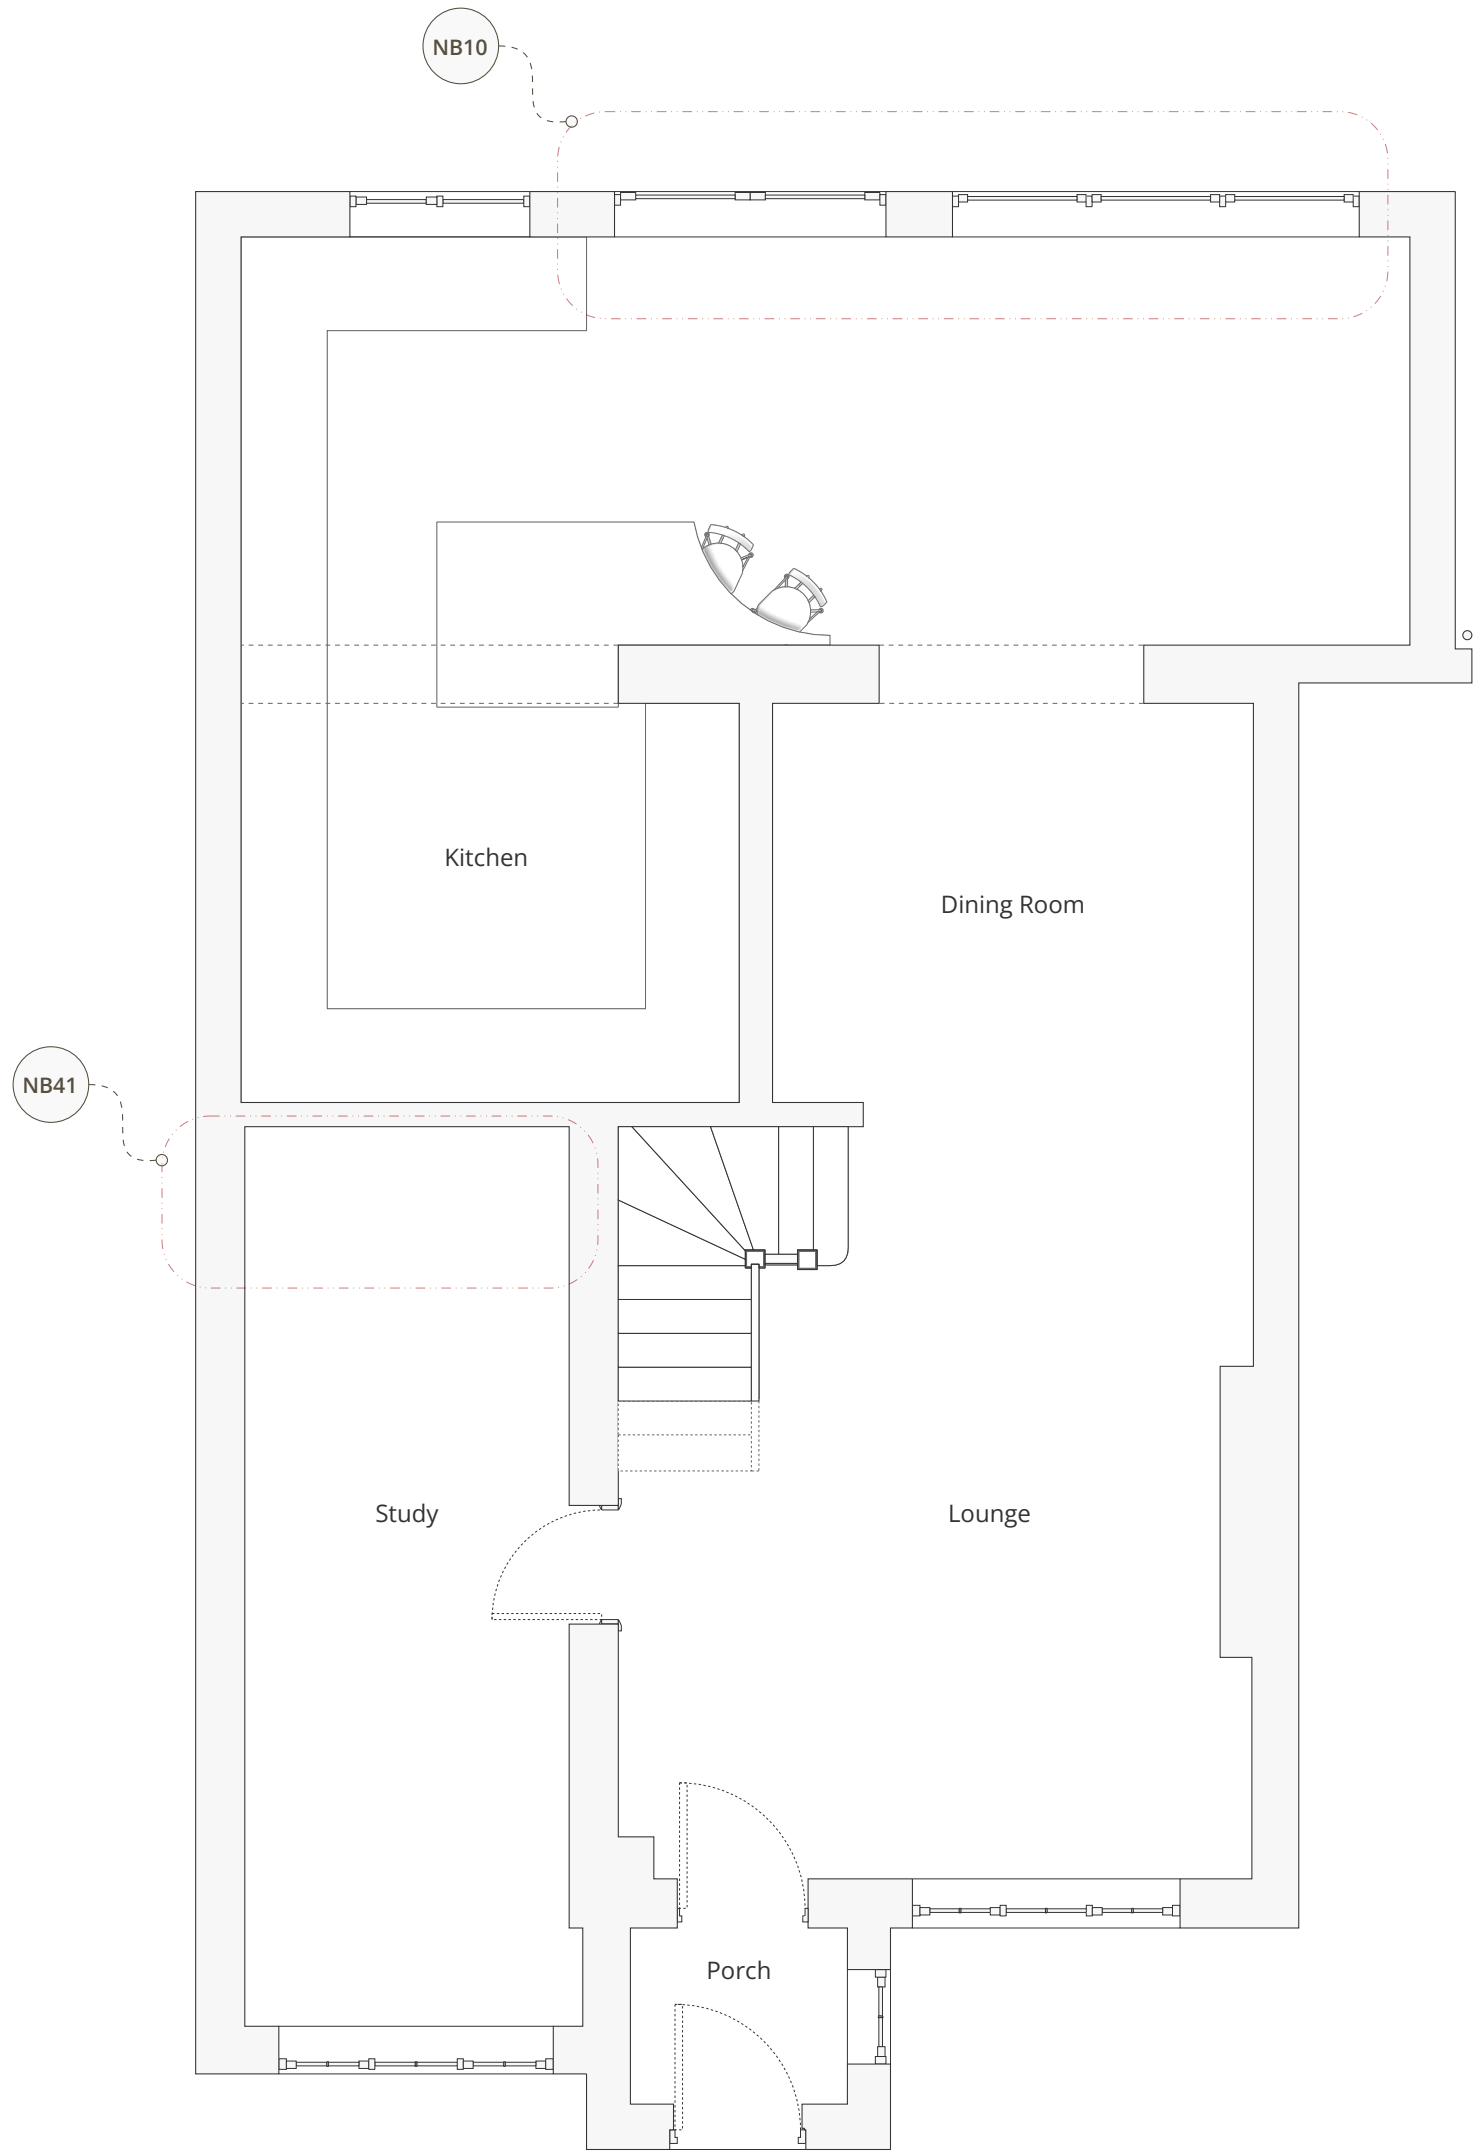


EXISTING GROUND FLOOR PLAN

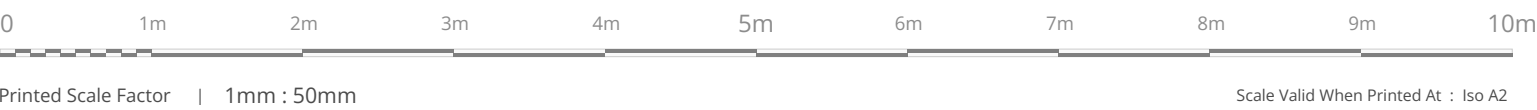

PROPOSED SCHEME

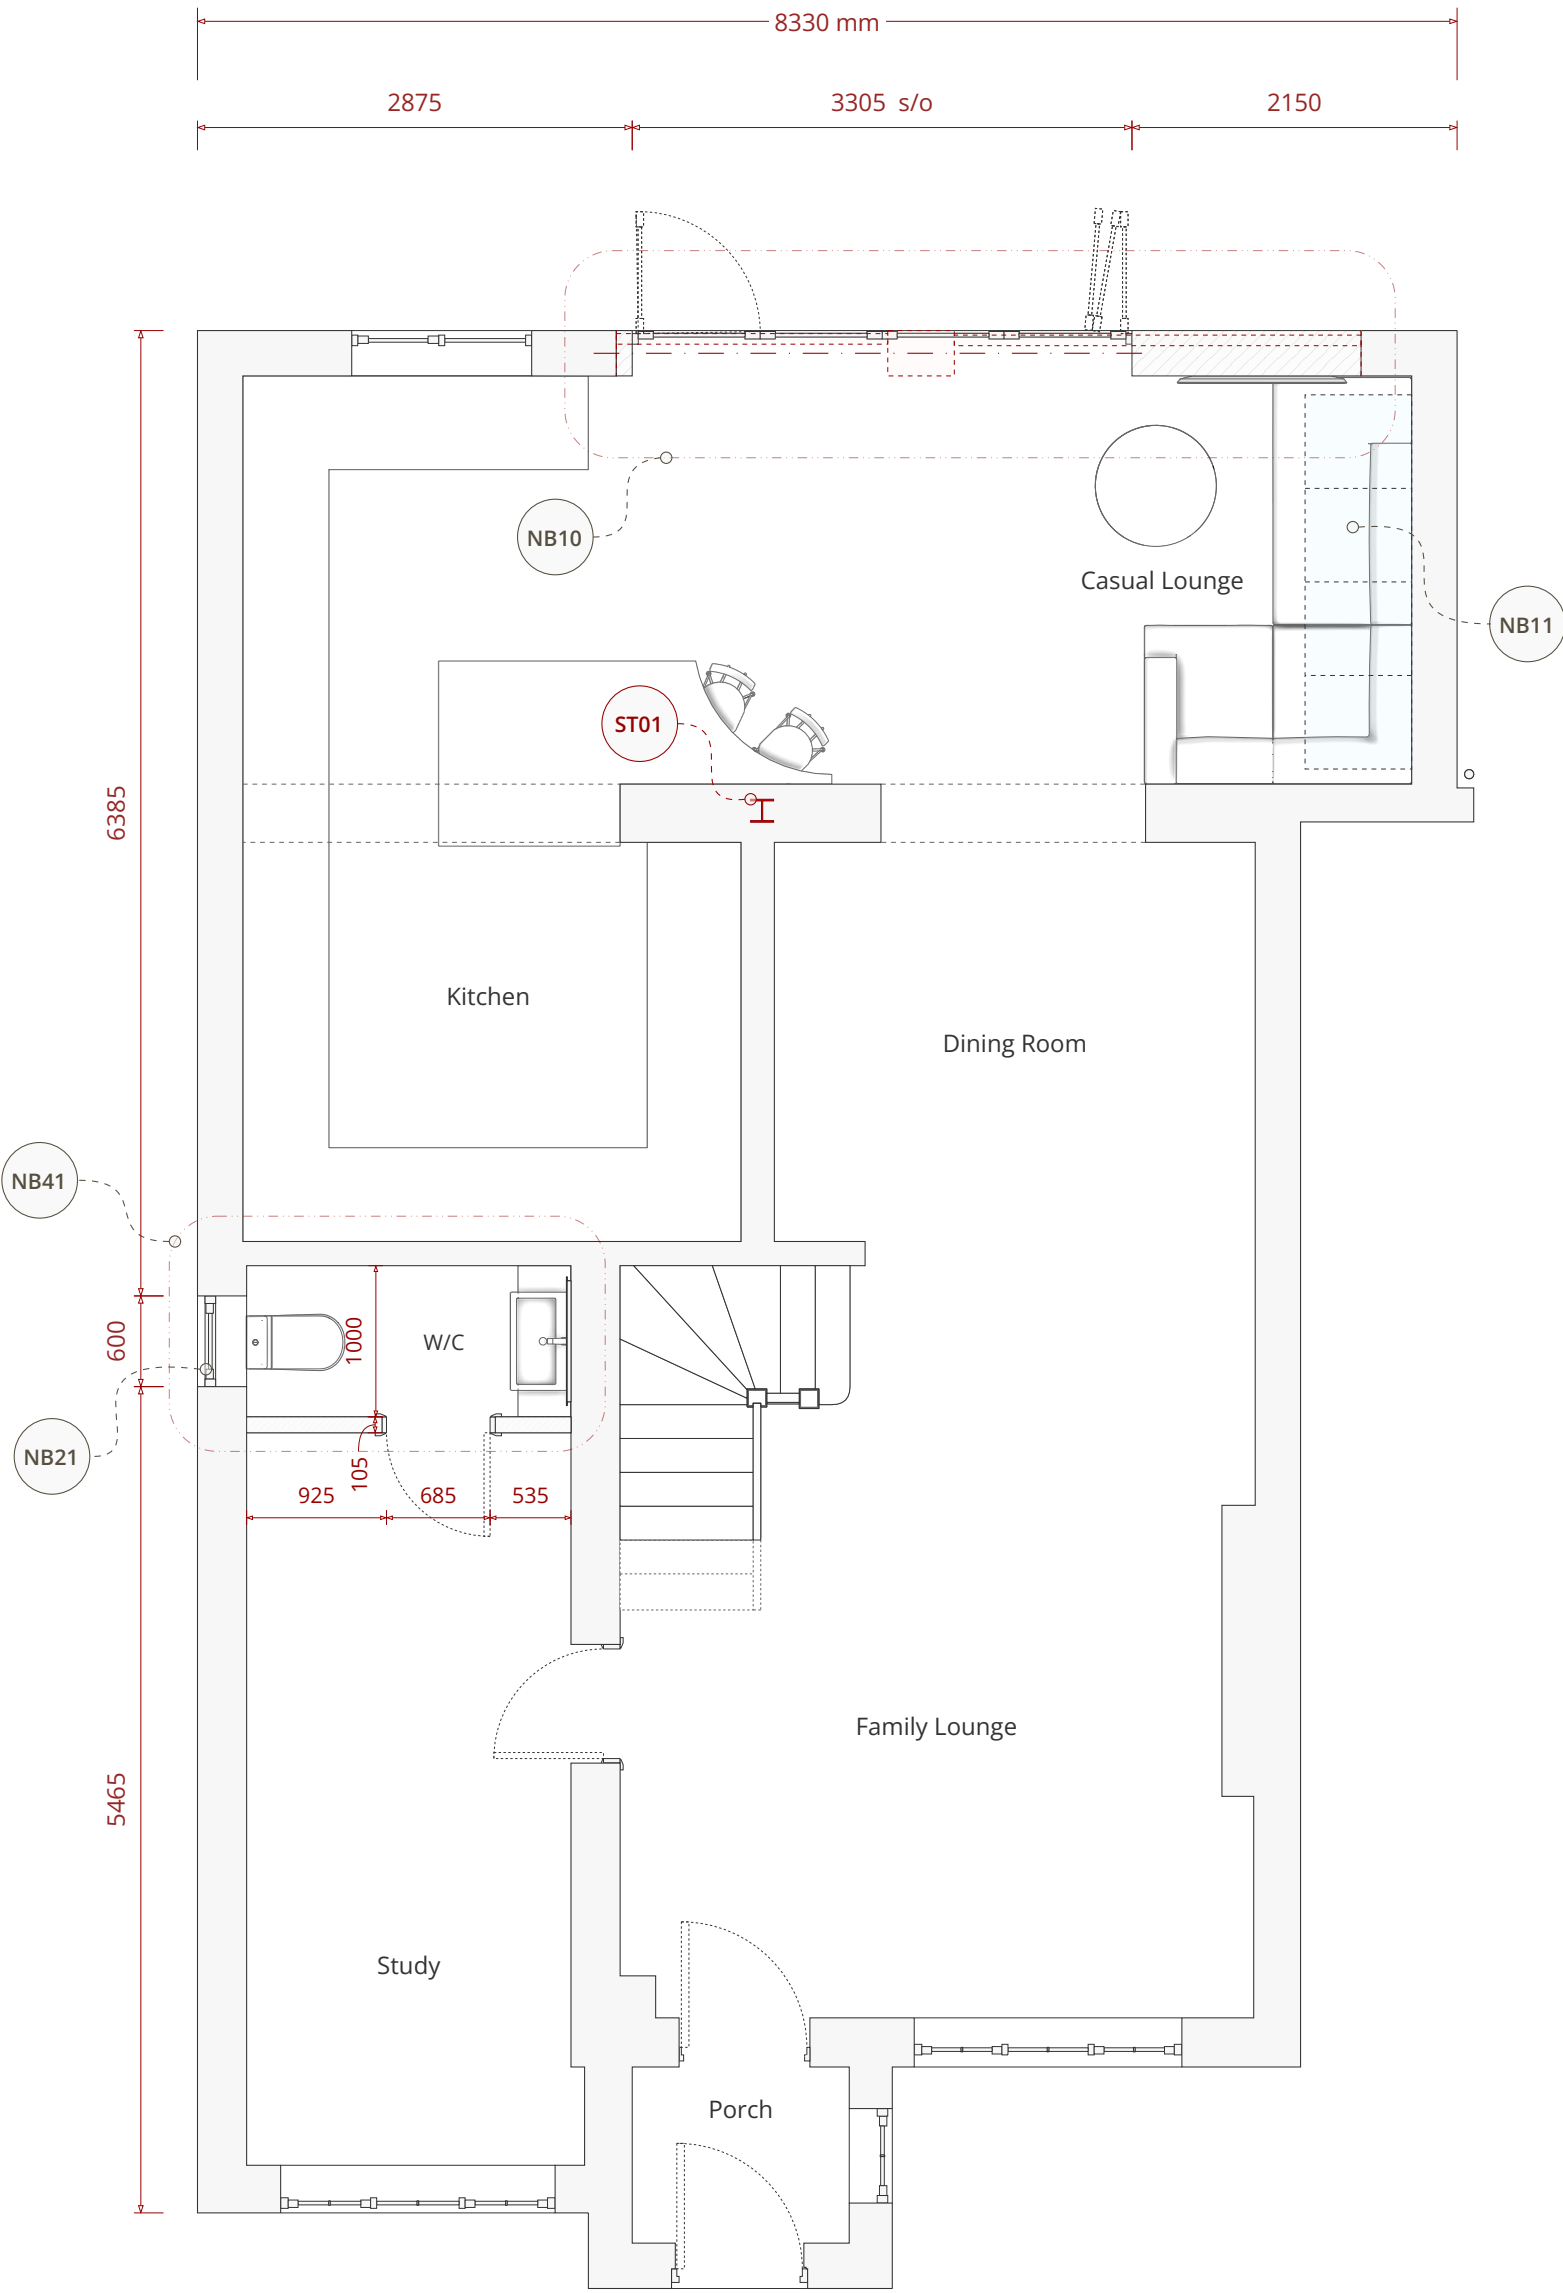

PROPOSED GROUND FLOOR PLAN

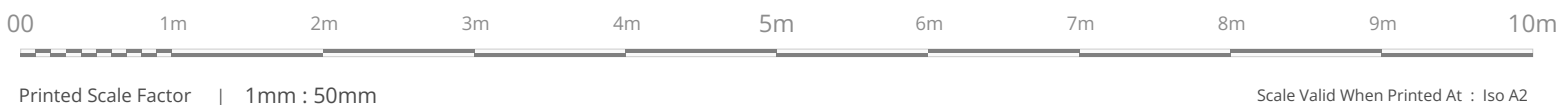

EXISTING CONDITIONS

NB41 | New Ground Floor WC

The proposal introduces a new ground-floor WC, formed by internally partitioning a section of the existing study. This space features a newly formed window on the eastern side elevation to provide natural light and ventilation. The contractor is responsible for all associated pipework, drainage, and mechanical ventilation, which must be designed and installed in full compliance with current Building Regulations.

NB10 | Rear Door Opening Alterations

The proposal removes the existing large window, wall nib, and rear patio doors to form a single, enlarged structural opening. The aim is to better align the window reveals, rectifying the previous extension where openings were added ad hoc without thought for rhythm. A new four-panel folding door system will be installed, featuring a master door for routine garden access and three folding panels to create a seamless transition between the kitchen and garden when required. The new structural opening requires a steel beam; load-bearing specifications must be certified by a qualified structural engineer and comply with all required Building Regulations prior to construction.

NB11 | Roof Replacement and New Glazed Roof Section

The addition of the first-floor extension over the main body of the existing rear extension leaves a narrow, residual section of the ground-floor footprint. Retaining the existing roof arrangement here would result in an awkward and visually unresolved slender mono-pitched element. The existing structure currently relies on a disproportionately large and visually intrusive parapet wall on the side elevation which is an unsympathetic historical addition that relates poorly to the original character of the host dwelling.

To resolve these architectural issues, the proposal includes replacing this residual roof section with a newly configured pitched glazed roof. By reorienting the roof pitch to span the shorter dimension, the proposal facilitates a dramatic reduction in the height and massing of the bulky parapet wall. This crucial alteration removes a visually jarring element, returning the side elevation to a much more subservient and sympathetic appearance.

Crucially, introducing this new glazed roof section allows us to entirely reorganise the rear elevation. The original rear facade is visually disjointed and poorly composed, featuring mismatched window and door sizes that fail to align with one another. By utilising the new roof glazing to harvest abundant natural light, we gained the design freedom to reposition the existing ground-floor doors and windows. This rearrangement results in a substantially more balanced and aesthetically pleasing rear elevation, where the south facing doors & windows now align cohesively.

ST01 | Potential Structural Column

Noble Architecture has identified the probable need for a structural column in the position indicated "ST01" on the proposed plans. This is due to the substantial span across the rear elevation, it is anticipated that mid-point support will be necessary to safely accommodate the required structural loads. While there remains a possibility that the attic truss manufacturer could engineer a solution utilising structural girders in lieu of a traditional steel beam(s) and column arrangement, this must be formally evaluated. This element is highlighted purely as a provisional point of discussion and is merely a flag. The definitive structural strategy, including all final load-bearing calculations and specifications, falls outside the scope of this appointment and must be independently confirmed and detailed by a qualified structural engineer during the subsequent Building Regulations stage.

General Note | Planning Purpose Only

This document and the associated drawing pack have been prepared explicitly and exclusively for the purpose of a statutory householder planning application. To ensure absolute clarity for the local planning authority assessing the scheme the document pack is intentionally lightweight. It deliberately omits detailed technical specifications including structural arrangements wall compositions thermal insulation details and floor or roof build ups. Consequently these documents are strictly not fit for construction purposes procurement or Building Regulations approval. Comprehensive technical design and structural engineering plans must be commissioned and approved at a subsequent stage prior to the commencement of any physical works.