



Scan Me

View Project Portal

SD02 - Structural Dimension Guide

- Example*
- Dimensions annotated in red text with diamond terminators indicate measurements to unfinished masonry faces.
- Example*
- Dimensions annotated with circular terminators denote centre-to-centre measurements between structural grid lines or structural member centrelines.

It is the strict responsibility of the Principal Contractor to verify all site measurements against both the architectural and structural engineer's drawings prior to the commencement of any off-site fabrication or on-site construction works. All tolerances etc must be allowed for by the contractor and steelwork fabricator.

JH03_T03_D32

EV02

SD01 - Structural Layout And Coordination Disclaimer


Under no circumstances is this drawing to be interpreted as the detailed structural design, fabrication schedule, or manufacturing instruction. This document is provided solely to assist the Principal Contractor in coordinating the spatial layout of structural members within the broader architectural scheme detailed by Noble Architecture. All specific member sizes, material grades, connection details, and load-bearing specifications must be sourced directly from the appointed Structural Engineer's approved plans, calculations, and reports. This drawing indicates setting out and architectural integration only; the Structural Engineer's documentation takes absolute precedence for all structural integrity and technical detailing matters.

THIRD PARTY



Scan Me

Structural Calculations
Compilation Board

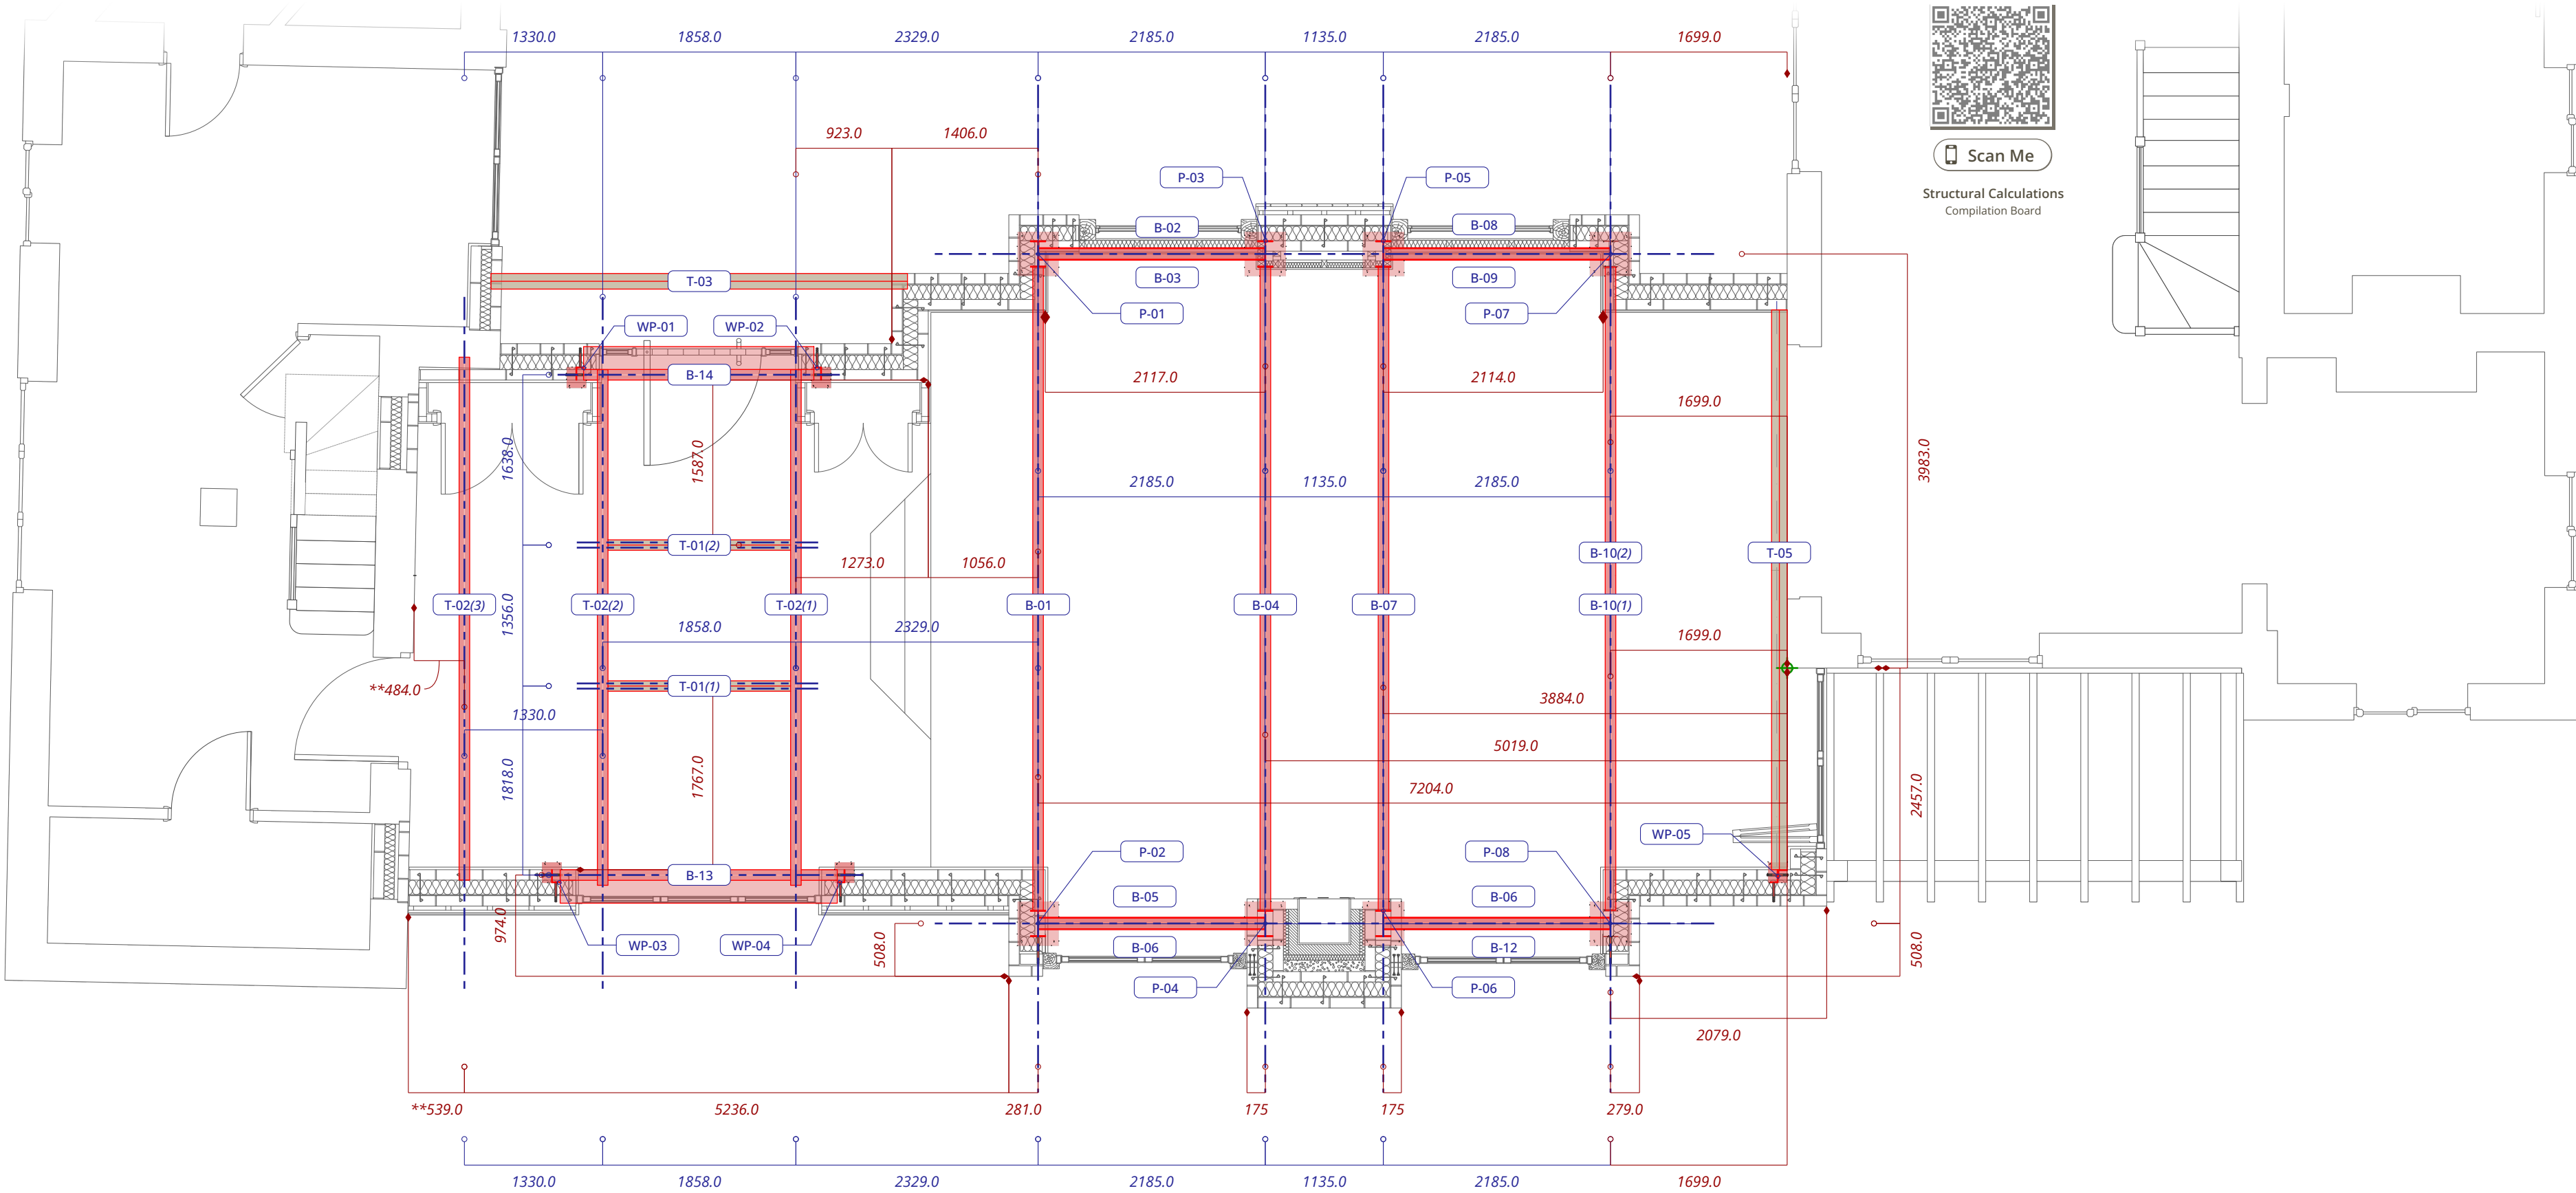

SD20 - Provisional Steel Beam Added

Box Gutter Support Ref: T-02(03)

This steel member has been introduced by Noble Architecture solely as a schematic solution to accommodate the box gutter detail below the first-floor window. It must be clearly understood that this inclusion is a spatial exercise only and is based on unverified assumptions; absolutely no structural calculations exist for this member at this stage. The sizing indicated is arbitrary and must not be used for construction. The Client is to confirm acceptance of the resulting bulkhead detail or alternatively consider removing the first-floor window, which may negate the requirement for this complex steel arrangement. Upon confirmation of the design intent, the Structural Engineer must be strictly instructed to perform all necessary calculations to determine the actual member size, suitability, padstone, & connection details required for structural integrity.

Structural Member Setting Out Plan



EV01

JH03_T03_D31

SD21 - Provisional Sructural Design Change

Dual Steel Beam Arrangement Ref: B-10(01) & B-10(02)

This steel member has been introduced by Noble Architecture solely as a schematic solution to accommodate the box gutter detail below the first-floor window. It must be clearly understood that this inclusion is a spatial exercise only and is based on unverified assumptions; absolutely no structural calculations exist for this member at this stage. The sizing indicated is arbitrary and must not be used for construction. The Client is to confirm acceptance of the resulting bulkhead detail or alternatively consider removing the first-floor window, which may negate the requirement for this complex steel arrangement. Upon confirmation of the design intent, the Structural Engineer must be strictly instructed to perform all necessary calculations to determine the actual member size, suitability, padstone, & connection details required for structural integrity.