





Scan Me


- View Project Portal
- Measuring Tools
 - Interactive 3D Model
 - Live Documents Online
 - 3D Images
 - Videos

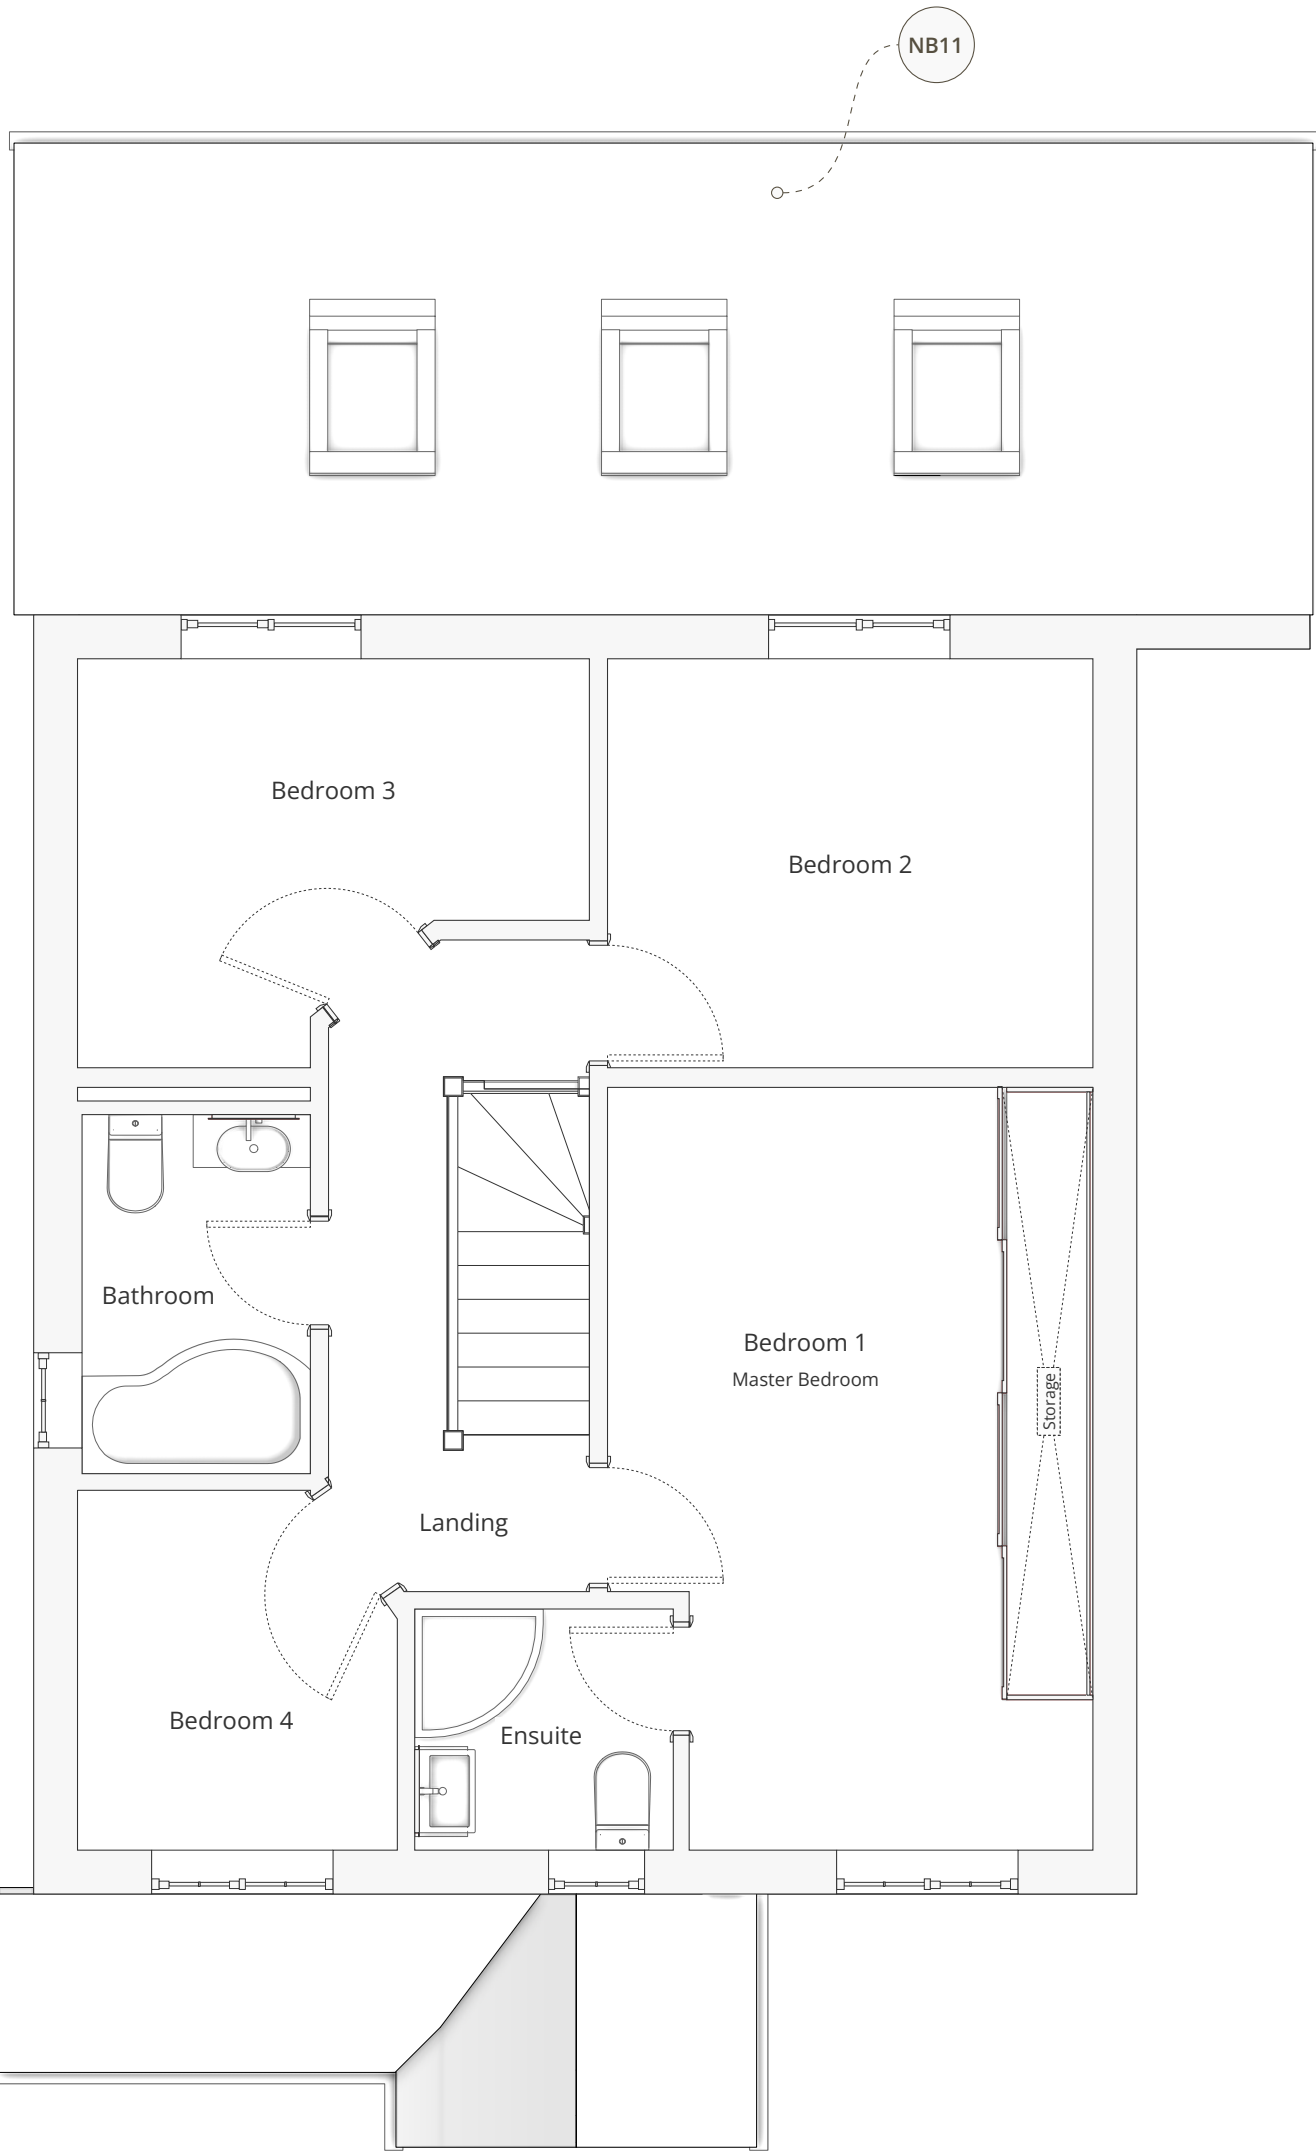

EXISTING FIRST FLOOR PLAN

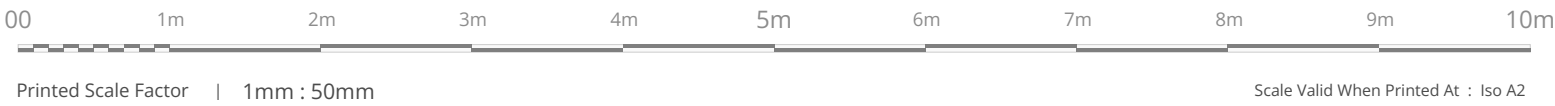

PROPOSED SCHEME

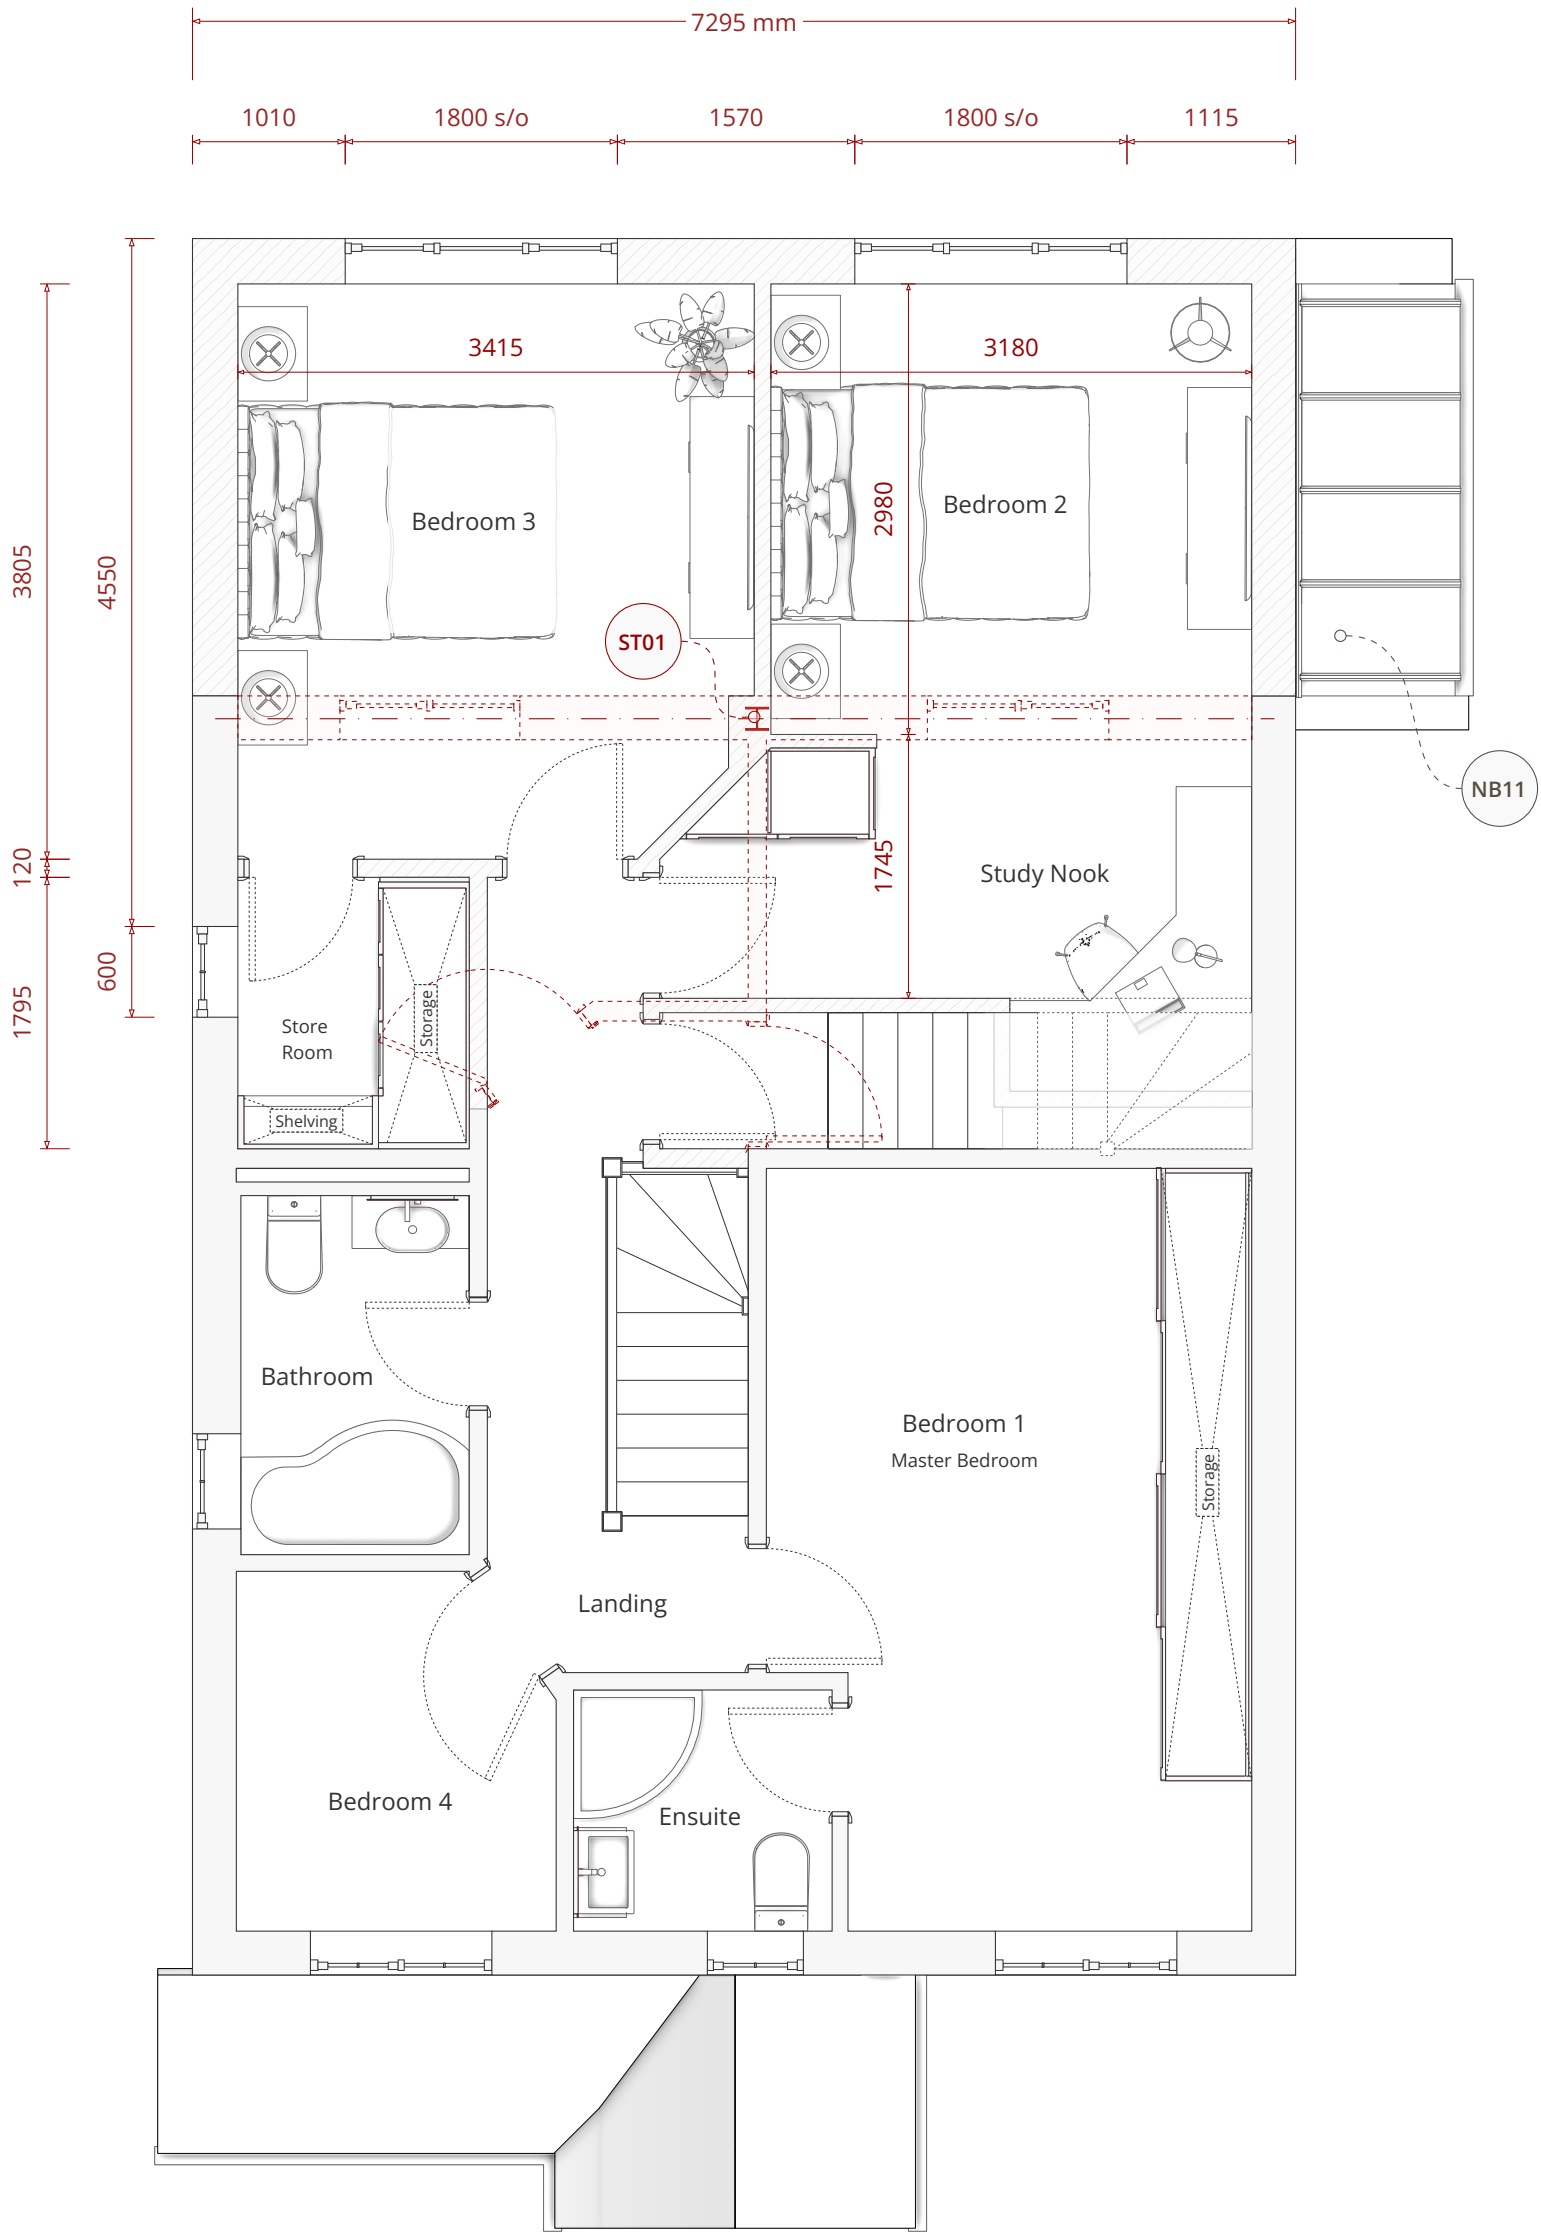

PROPOSED FIRST FLOOR PLAN



EXISTING CONDITIONS

NB05 | Roof Replacement and New Glazed Roof Section

The addition of the first-floor extension over the main body of the existing rear extension leaves a narrow, residual section of the ground-floor footprint. Retaining the existing roof arrangement here would result in an awkward and visually unresolved slender mono-pitched element. The existing structure currently relies on a disproportionately large and visually intrusive parapet wall on the side elevation which is an unsympathetic historical addition that relates poorly to the original character of the host dwelling.

To resolve these architectural issues, the proposal includes replacing this residual roof section with a newly configured pitched glazed roof. By reorienting the roof pitch to span the shorter dimension, the proposal facilitates a dramatic reduction in the height and massing of the bulky parapet wall. This crucial alteration removes a visually jarring element, returning the side elevation to a much more subservient and sympathetic appearance.

Crucially, introducing this new glazed roof section allows us to entirely reorganise the rear elevation. The original rear facade is visually disjointed and poorly composed, featuring mismatched window and door sizes that fail to align with one another. By utilising the new roof glazing to harvest abundant natural light, we gained the design freedom to reposition the existing ground-floor doors and windows. This rearrangement results in a substantially more balanced and aesthetically pleasing rear elevation, where the south facing doors & windows now align cohesively.

ST01 | Potential Structural Column

Noble Architecture has identified the probable need for a structural column in the position indicated "ST01" on the proposed plans. This is due to the substantial span across the rear elevation, it is anticipated that mid-point support will be necessary to safely accommodate the required structural loads. While there remains a possibility that the attic truss manufacturer could engineer a solution utilising structural girders in lieu of a traditional steel beam(s) and column arrangement, this must be formally evaluated. This element is highlighted purely as a provisional point of discussion and is merely a flag. The definitive structural strategy, including all final load-bearing calculations and specifications, falls outside the scope of this appointment and must be independently confirmed and detailed by a qualified structural engineer during the subsequent Building Regulations stage.

General Note | Planning Purpose Only

This document has been prepared explicitly for the purpose of a Planning Application. To ensure clarity for the Planning Officers assessment, the document pack is intentionally lightweight and omits detailed technical specifications, including structural arrangements, wall compositions, and floor / roof build-ups. Consequently, these documents are strictly not fit for construction purposes or Building Regulations approval. Comprehensive technical design and structural engineering plans must be commissioned and approved at a subsequent stage prior to the commencement of any works.

Preliminary & Unchecked Document

This document is issued as a preliminary draft for initial review and consultation purposes only. It is currently an unchecked drawing and has not yet been subjected to the rigorous final quality assurance and technical checking procedures conducted post-production. As such, it may contain drafting anomalies, typographical errors, or unverified dimensions. It must not be relied upon as a finalised document for pricing or planning submission until formally checked, approved, and issued as a completed revision.