




Scan Me


View Project Portal

- Measuring Tools
- Interactive 3D Model
- Live Documents Online
- 3D Images
- Videos

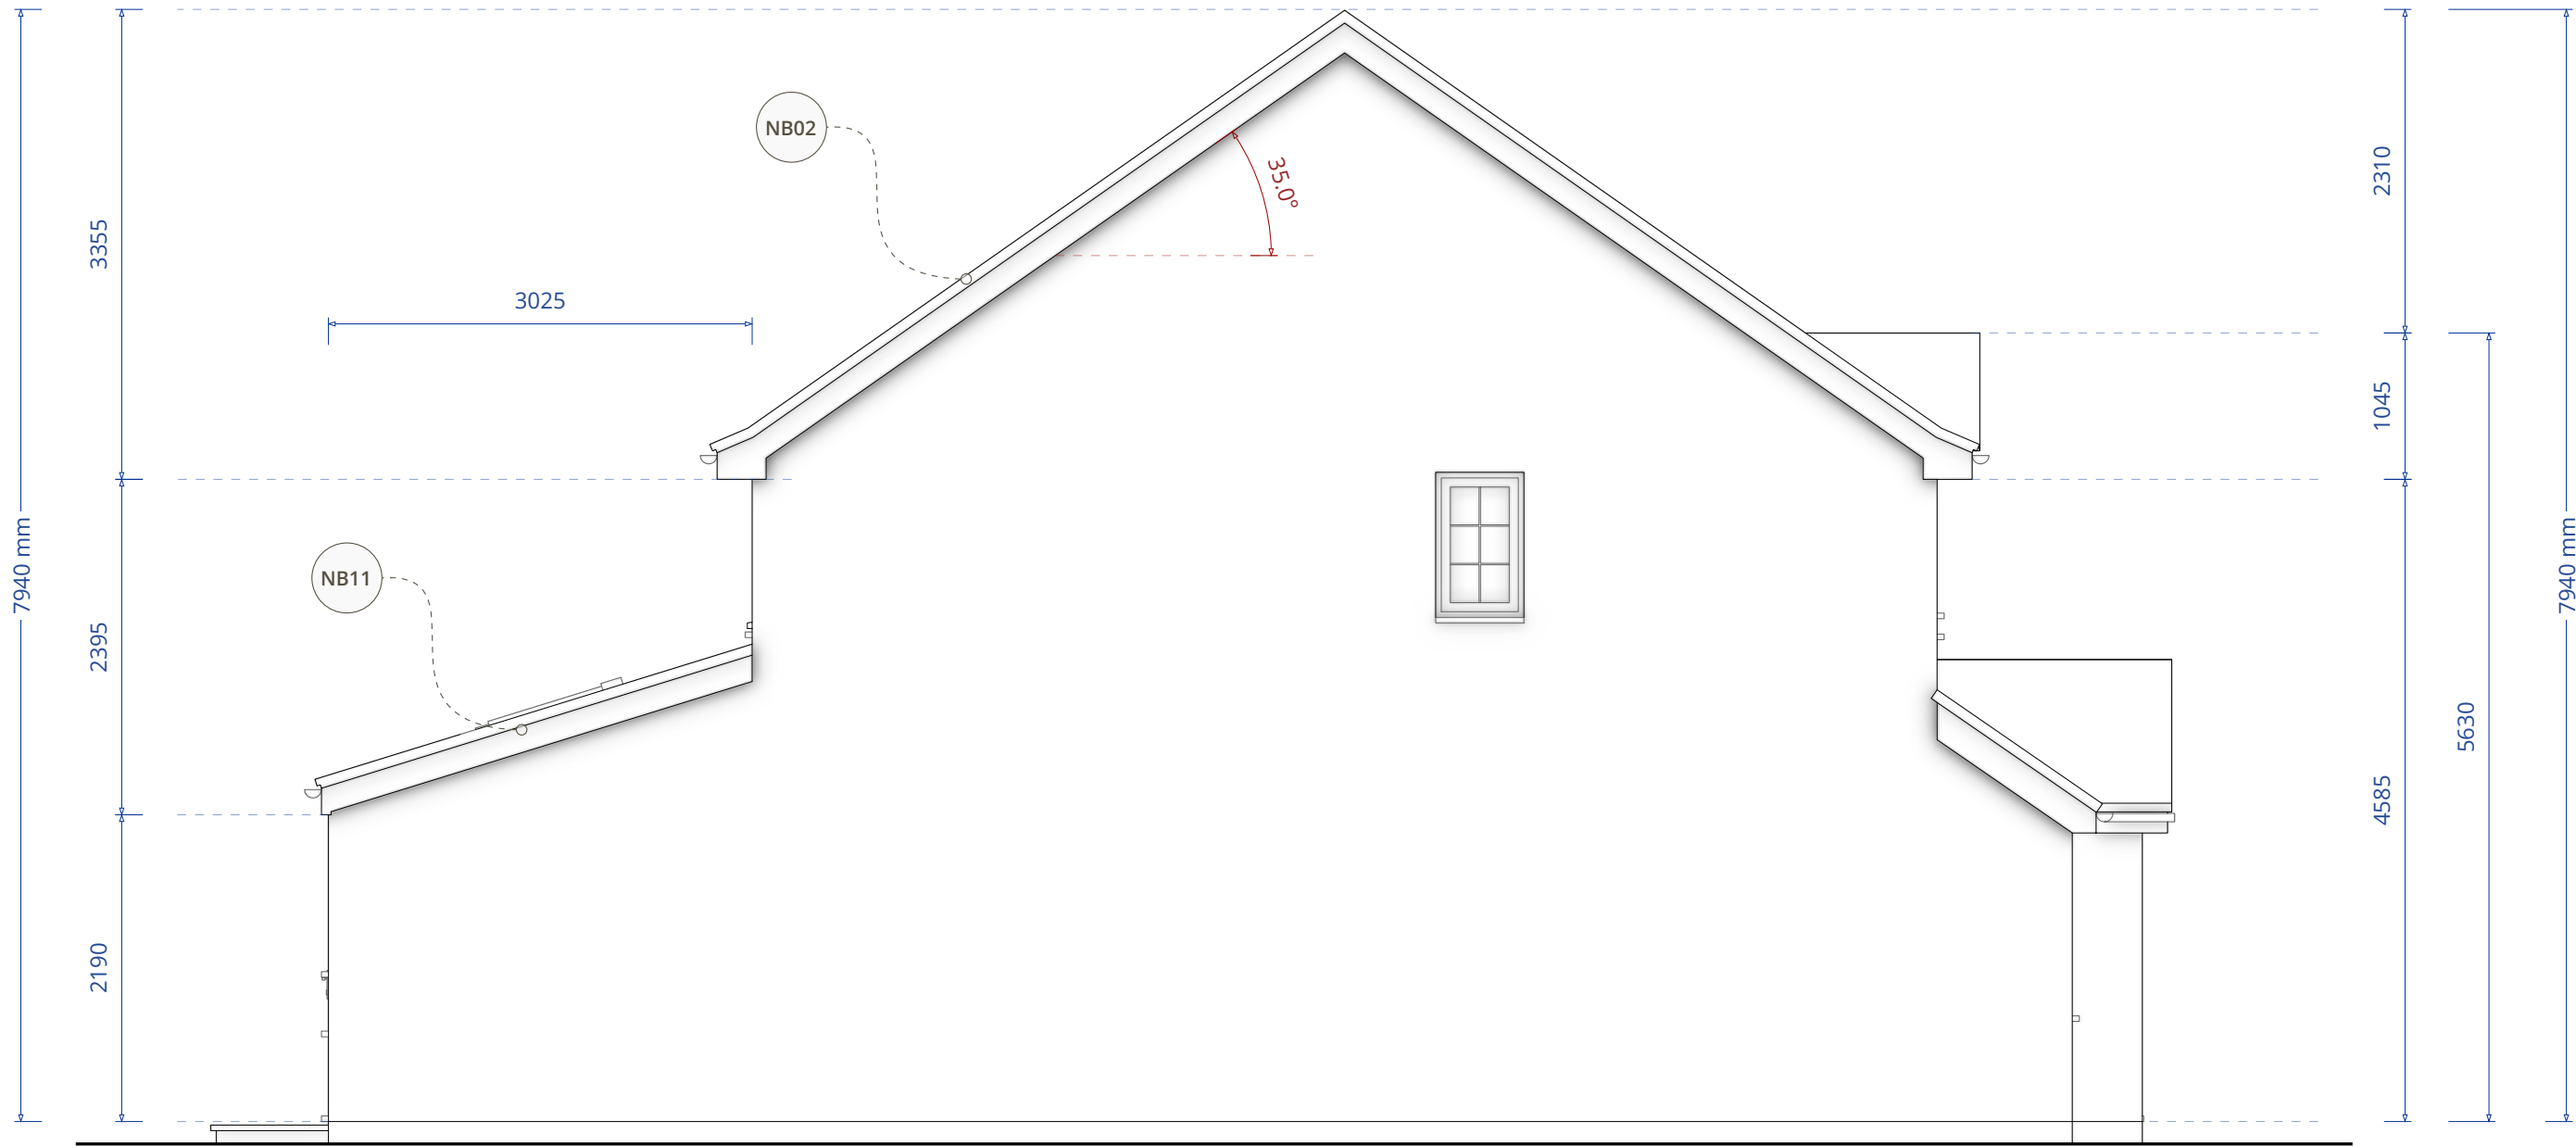

EXISTING CONDITIONS

PROPOSED SCHEME

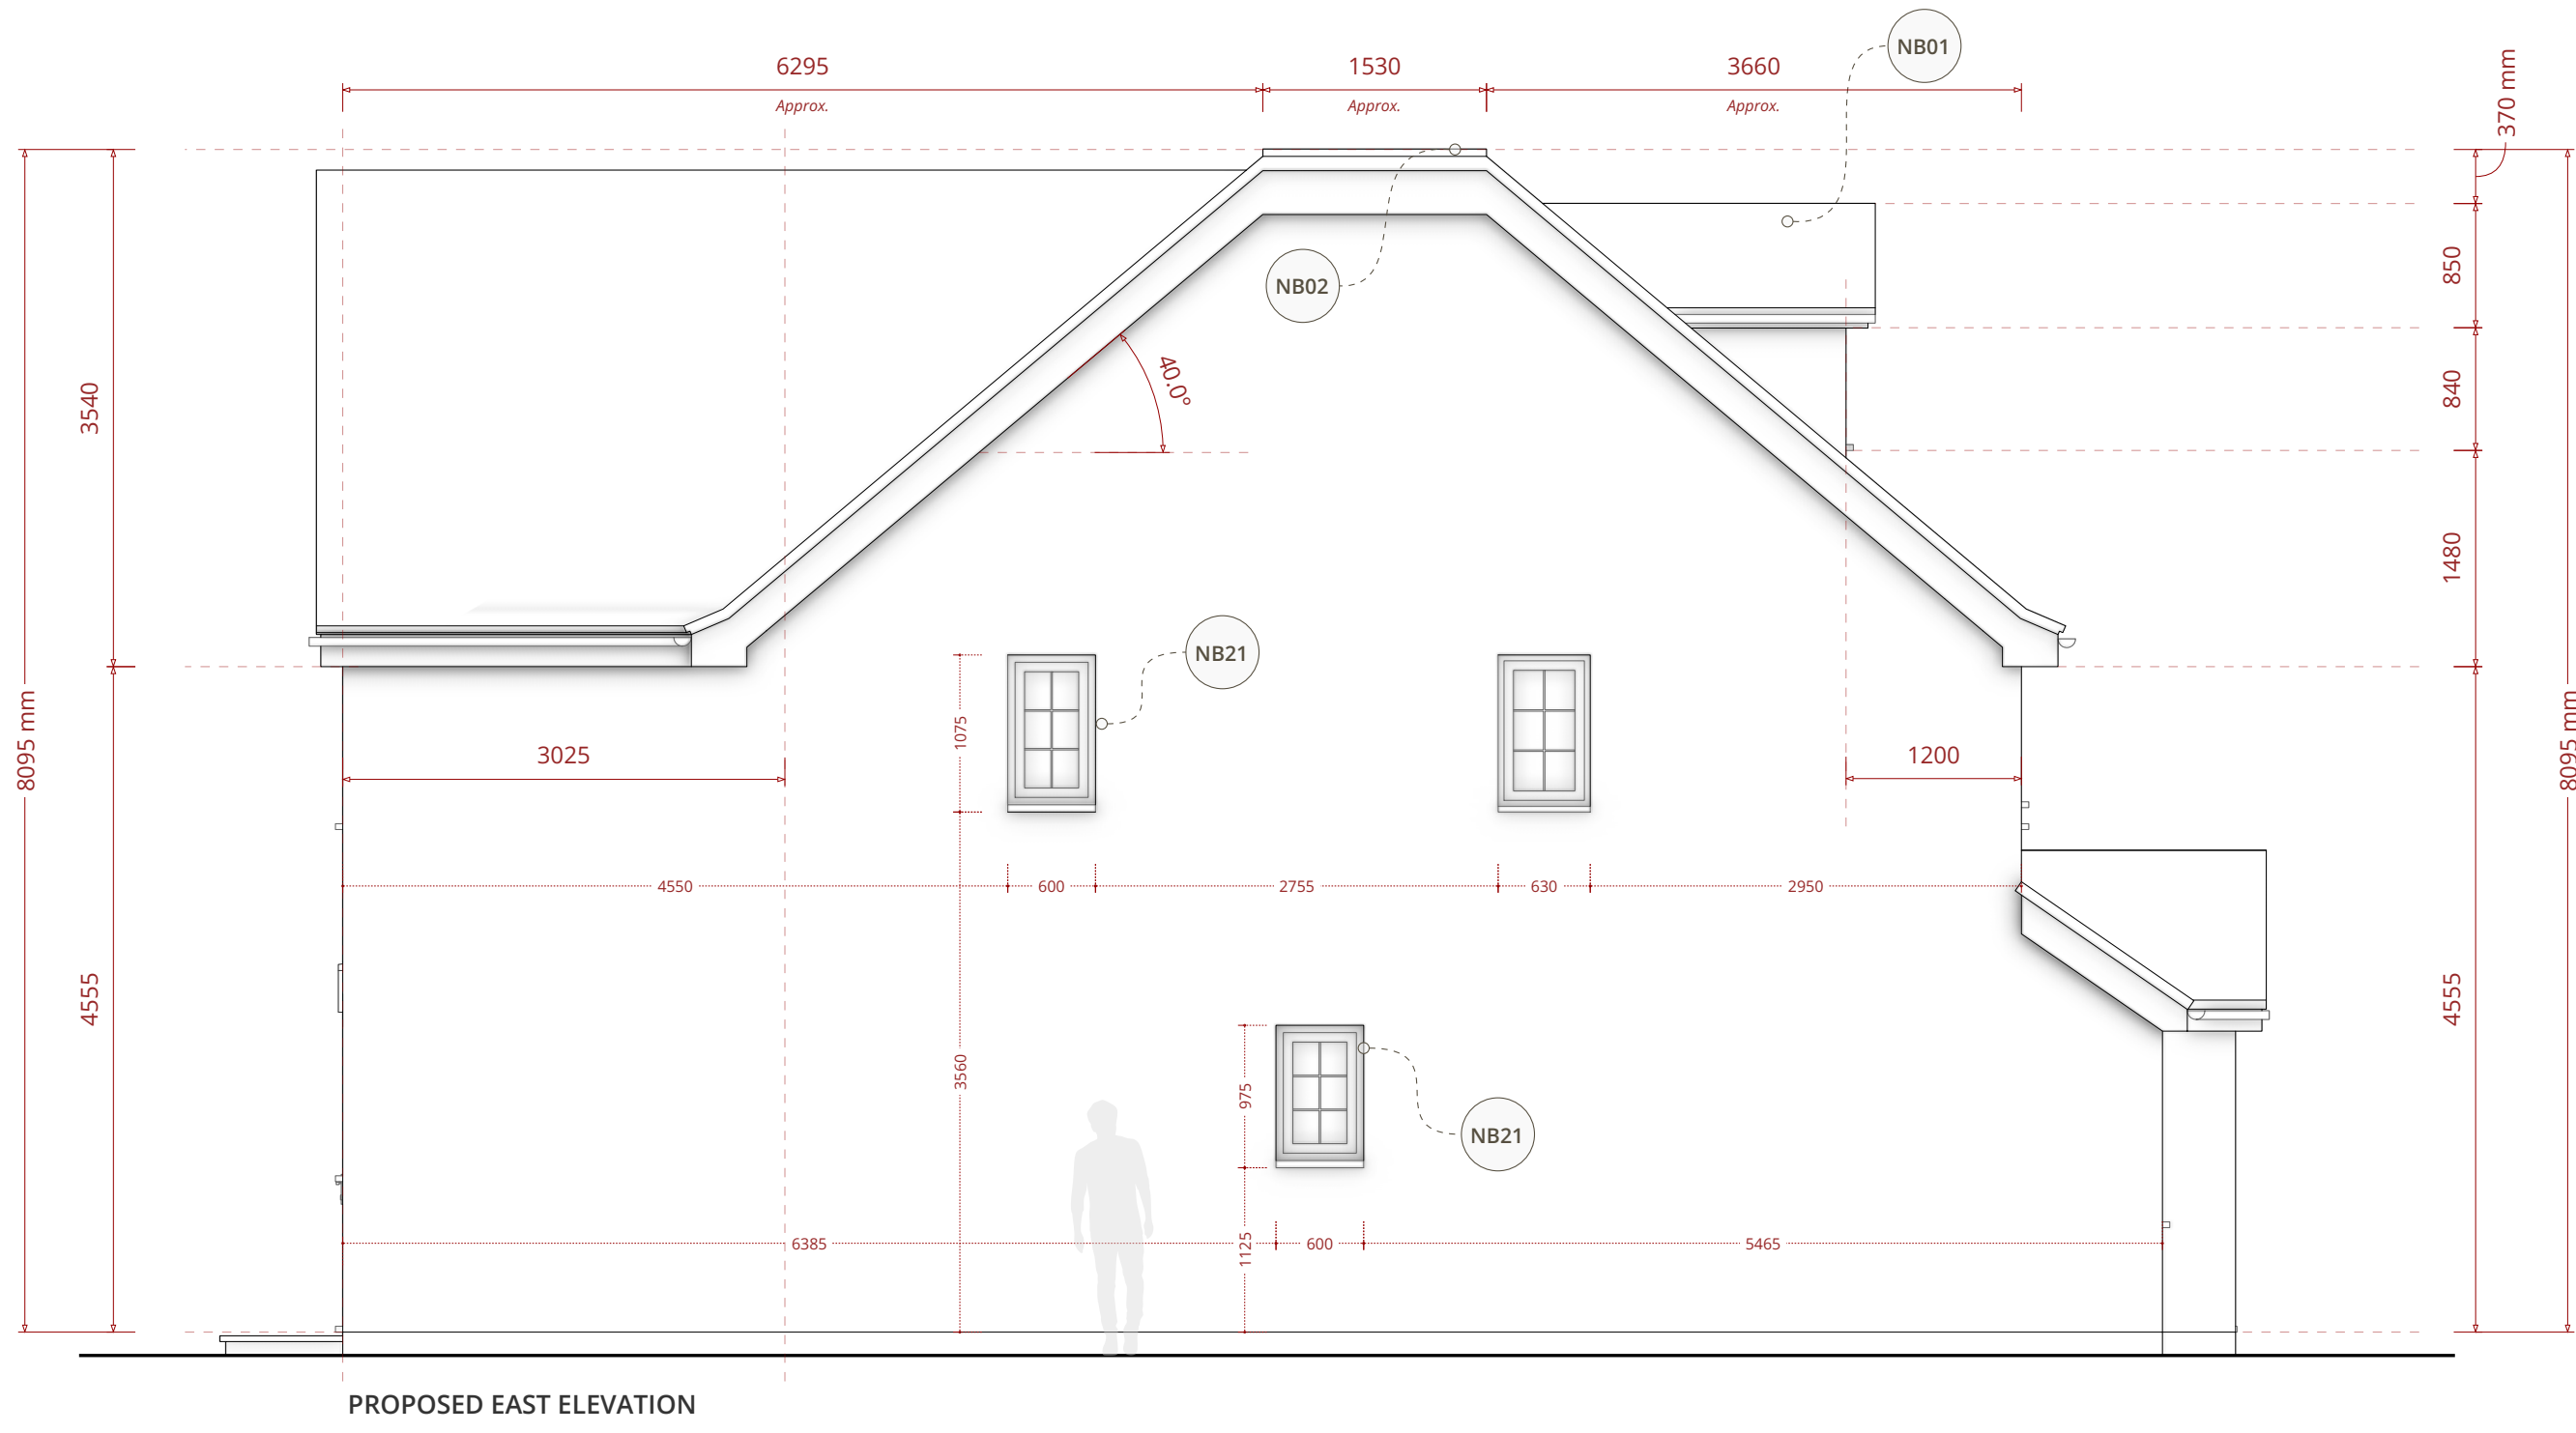

NB21 | New Additional Side Windows

Careful consideration has been given to the new windows proposed on the eastern side elevation to ensure openings remain subservient and sympathetic to the host dwelling. The newly introduced windows have been deliberately designed as modest, proportionately small openings that are highly appropriate for a secondary side elevation. To maintain a cohesive visual appearance across the property, these windows have been chosen to replicate the traditional cottage bar design already present on the existing elevation. These proportionate additions are strictly functional, providing essential natural light and ventilation to the newly formed ground-floor WC and the new first-floor store room, while respecting the overall architectural character of the building and mitigating any potential impact on neighbouring privacy amenity.

NB02 | Roof Replacement

To secure the necessary internal head height and usable floor area for the loft conversion, the proposal features a new crown roof. The current roof structure utilises restrictive fink-style trusses, meaning a complete roof replacement is fundamentally required. A traditional apex roof was discounted as it would raise the ridge to an unacceptable height. As evidenced by the drone imagery in the Design and Access Statement, the neighbouring property at No. 9 occupies an elevated topographical position with a significantly steeper, taller roof structure, establishing a clear precedent for a higher permissible ridge line on Ashness Close. Despite this precedent, the applicant consciously opted to cap the proposed ridge height by flattening the apex into a crown design. While a more financially intensive structural solution, this approach successfully mimics a traditional pitched roof from the principal front and rear elevations, remaining faithful to the original roof pitch and rigorously protecting the established character of the street scene.

The contractor is responsible for all technical roof design and coordinating the scheme with an attic truss manufacturer (e.g., Trusstec or similar). All insulation, vapour control, and structural elements must be designed and specified in full compliance with current Building Regulations.

ST02 | Technical Specifications And Structural Design

The proposed scheme involves significant structural alterations including a complete roof replacement to a crown roof design and the insertion of a large rear structural opening. All load bearing elements including steel beams structural columns attic trusses and foundations must be independently designed specified and certified by a fully qualified structural engineer. Furthermore the contractor is responsible for all mechanical electrical and plumbing designs including the new ground floor washroom drainage. Noble Architecture accepts no responsibility for the structural integrity or technical performance of the proposed design.

General Notes | Planning Purpose Only Package

This document and the associated drawing pack have been prepared explicitly and exclusively for the purpose of a statutory householder planning application. To ensure absolute clarity for the local planning authority assessing the scheme the document pack is intentionally lightweight. It deliberately omits detailed technical specifications including structural arrangements wall compositions thermal insulation details and floor or roof build ups. Consequently these documents are strictly not fit for construction purposes procurement or Building Regulations approval. Comprehensive technical design and structural engineering plans must be commissioned and approved at a subsequent stage prior to the commencement of any physical works.

Contractor Responsibilities & Verification

The appointed building contractor is solely responsible for verifying all dimensions site levels and existing boundary conditions prior to the commencement of any fabrication ordering of materials or construction works. Any discrepancies found between these preliminary planning drawings and the physical site must be reported immediately to Noble Architecture and the client. The contractor must not scale directly from these drawings for construction purposes. The appointed principal contractor assumes full responsibility for ensuring all executed works comply strictly with current Building Regulations local authority requirements and all relevant health and safety legislation.

Limitation Of Liability And Indemnity

Noble Architecture shall not be held liable for any direct indirect or consequential loss injury or damage arising from the unauthorised use of these drawings for any purpose other than obtaining town and country planning permission. The client and any subsequently appointed contractors fully indemnify Noble Architecture against any claims financial costs or legal liabilities resulting from the misuse of these drawings for construction pricing structural implementation or Building Control submissions. By proceeding with the project beyond the planning phase the client formally acknowledges the necessity of engaging appropriate technical professionals for the detailed construction phase.