





Scan Me

View Project Portal

- Measuring Tools
- Interactive 3D Model
- Live Documents Online
- 3D Images
- Videos

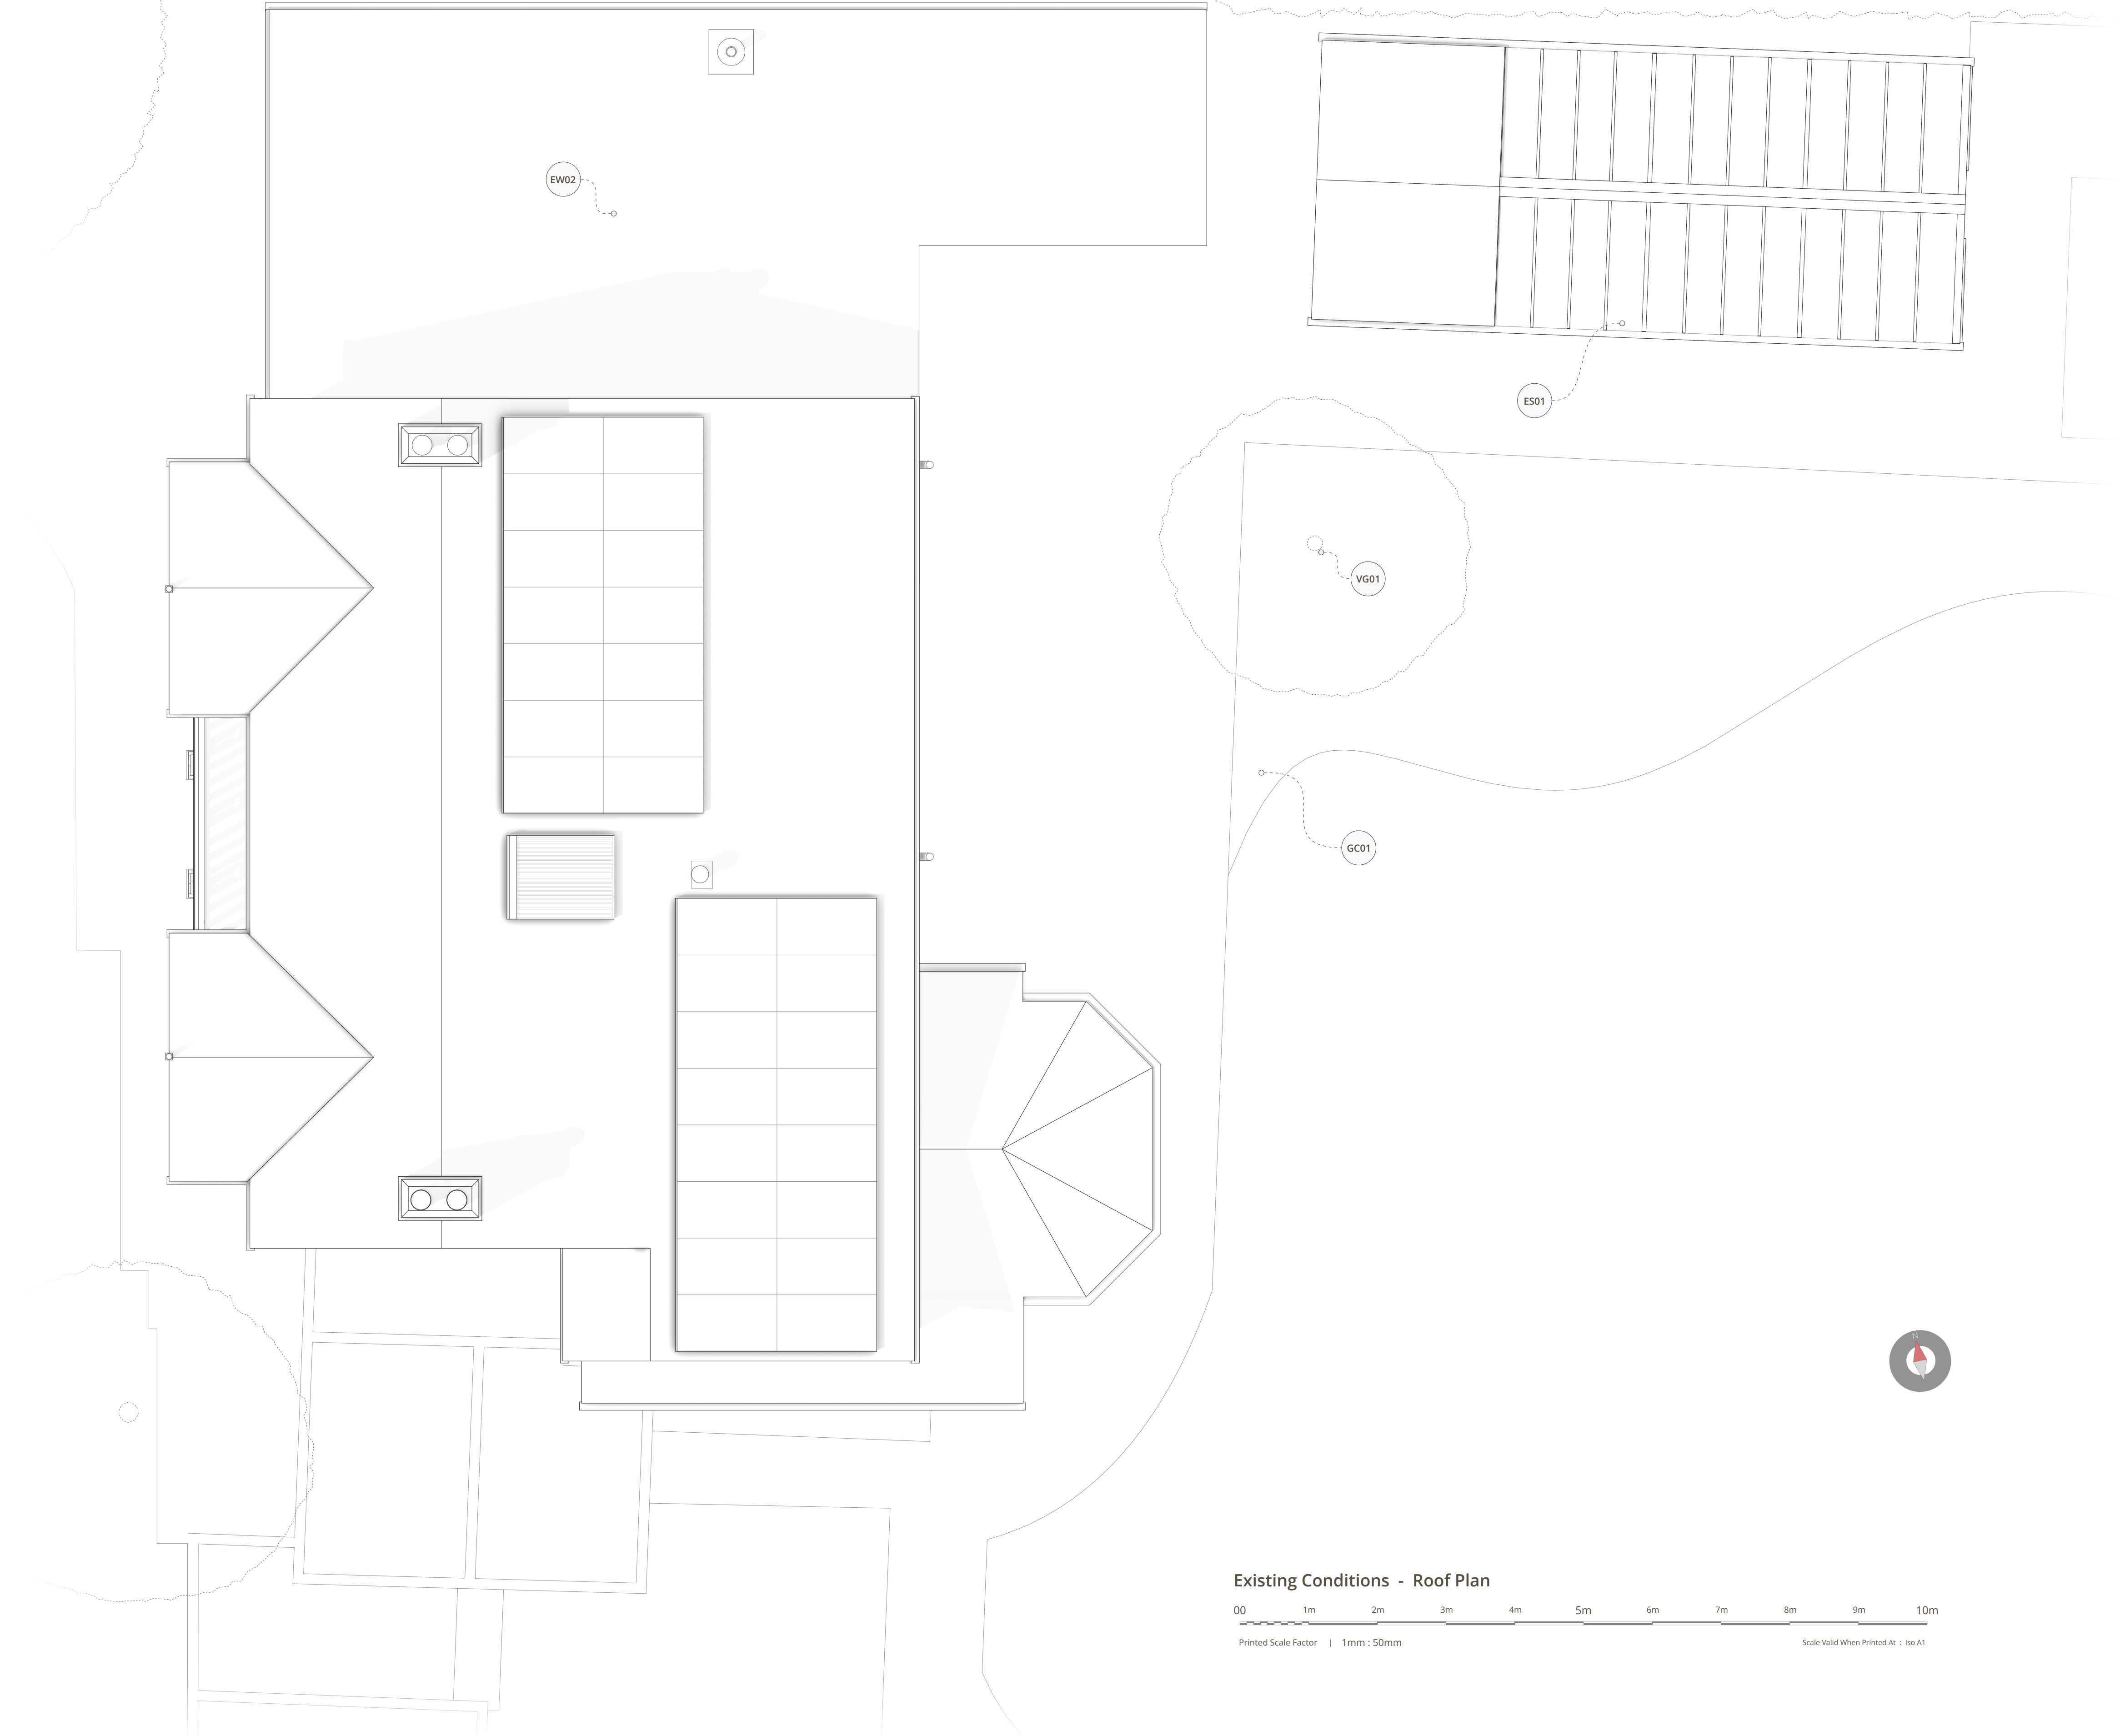

Existing Conditions - Roof Plan

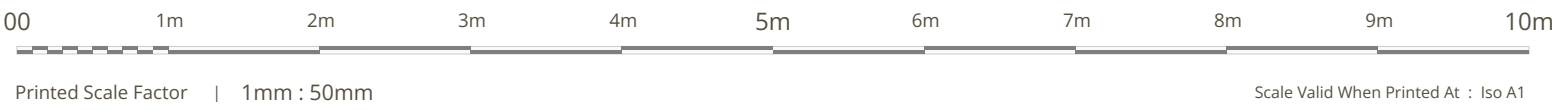

General Existing Conditions Notes

The following notes apply to the existing conditions drawings, including the existing ground floor plan, the existing first floor plan and the existing elevations, and record the basis, scope and limitations of the survey information upon which they rely.

EX01 | Existing Greenhouse Recorded Prior To Removal

The greenhouse shown to the east of the dwelling is recorded as existing and is earmarked for removal under the proposals. It is a derelict single-glazed structure long out of horticultural use, as set out at Section 1.0 of the Design and Access Statement, and its footprint is re-used by the proposed garden room (notes GF06 and ES01). Its inclusion on this plan records the existing developed footprint relied upon in the Green Belt case at Section 11.0 of the Design and Access Statement.

EX02 | Existing First Floor Arrangement

The first floor is recorded as existing with four bedrooms, a family bathroom and a single en suite serving Bedroom 1. Bedroom 4 presently serves as a games room and playroom and contains the redundant chimney breast whose external stack was removed above the roof line many years ago. An internal step guards the approach to two of the bedrooms beyond the landing, while Bedroom 4 alone is reached entirely on the level from the head of the single straight staircase flight. These recorded characteristics underpin the accessible first floor reconfiguration described at Section 4.5 of the Design and Access Statement and at notes FF01 to FF06.

EX03 | Concealed Structure Not Surveyed Or Opened Up

The survey is non-intrusive and no opening up of the existing fabric has been undertaken. Wall constructions, lintel provisions, floor build-ups, roof structures and foundations are therefore not recorded and must not be assumed. The existing beams indicated at markers EB01, EB02 and EB03 are recorded from visible downstands and finishes only; their sizes, conditions, bearings and load paths are unknown. A destructive structural survey and a full structural design by a qualified structural engineer are required before any structural works, in accordance with notes ST02 and ST03.

EX04 | Basis And Purpose Of The Measured Survey

The existing conditions plans are derived from a measured building survey undertaken to RICS-aligned standards and commissioned expressly and exclusively as a means of supporting a statutory householder planning application. The level of measured accuracy and detail is proportionate to that purpose and to no other. The survey data is supplemented by the high precision LiDAR terrain capture and the photogrammetric orthographic mapping described at Sections 17.1 and 17.2 of the Design and Access Statement, which together provide an independently verifiable record of the site as existing. These drawings must be read in conjunction with the standing General Notes at the end of this schedule.

EX05 | Not For Construction, Fabrication Or Procurement

These existing conditions drawings are strictly not fit for construction purposes, fabrication, procurement, joinery or steelwork ordering, kitchen or sanitaryware setting out, or Building Regulations approval. No dimension shall be scaled from these drawings. Any party requiring dimensions for fabrication or ordering of any kind, including without limitation the principal contractor, subcontractors, steel fabricators, joinery manufacturers and window and door suppliers, must take and rely upon their own site measurements.

EX06 | Contractor Verification Of All Dimensions

The appointed principal contractor is solely responsible for verifying all dimensions, levels, openings and existing boundary conditions on site prior to the commencement of any fabrication, ordering of materials or construction works. Any discrepancy found between these drawings and the physical site must be reported immediately to Noble Architecture and the client before proceeding. The contractor must not scale from these drawings for any purpose.

EX07 | Services And Drainage Not Traced

Existing mechanical, electrical and plumbing services, together with below-ground drainage runs, have not been traced and are not recorded on these drawings. Where any sanitaryware, appliance or service position is shown it is indicative of surface-visible fittings only. The contractor must locate, trace and verify all services and drainage on site prior to any works, must undertake a CCTV drainage survey where below-ground connections are to be made or altered, and must protect all live services throughout the construction period.

EX08 | Boundaries, Gardens And Site Features Indicative

Beyond the footprint of the measured buildings, garden features, planting, tree canopies, hard landscaping edges and boundary lines are shown indicatively, derived from the photogrammetric orthographic mapping and licensed mapping data described at Section 17.2 of the Design and Access Statement. The drawings do not constitute a legal boundary survey, no title investigation has been undertaken by Noble Architecture, and legal boundaries must be confirmed against the registered title wherever they are material to any works.

EX09 | Levels And Datums

Levels shown on the existing conditions drawings are relative to the ground floor finished level (GFFL) datum. Site levels in metres AOD are to be appended on completion of the topographical survey, and the flood-related level commitments of the scheme are recorded at Sections 9.2 and 9.3 of the Design and Access Statement.

EX10 | Survey Markers On The Existing Plans

The coded markers appearing on the existing conditions plans are cross-referenced as follows: EB01 to EB03 record existing beams (note ST03); GC01 and GC02 record the hand-dug ground condition trial pits (Site Plan Landscaping Notes); and VG01 records the ornamental cherry tree to be carefully relocated, not felled (note VG01). Each marker is provided so that the assessing officer can locate the physical evidence relied upon in the Design and Access Statement directly on the survey record.

General Note | Planning Purpose Only

This document and the associated drawing pack have been prepared explicitly and exclusively for the purpose of a statutory householder planning application. To ensure absolute clarity for the local planning authority assessing the scheme the document pack is intentionally lightweight. It deliberately omits detailed technical specifications including structural arrangements wall compositions thermal insulation details and floor or roof build ups. Consequently these documents are strictly not fit for construction purposes procurement or Building Regulations approval. Comprehensive technical design and structural engineering plans must be commissioned and approved at a subsequent stage prior to the commencement of any physical works.

Contractor Responsibilities And Verification

The appointed building contractor is solely responsible for verifying all dimensions site levels and existing boundary conditions prior to the commencement of any fabrication ordering of materials or construction works. Any discrepancies found between these preliminary planning drawings and the physical site must be reported immediately to Noble Architecture and the client. The contractor must not scale directly from these drawings for construction purposes. The appointed principal contractor assumes full responsibility for ensuring all executed works comply strictly with current Building Regulations local authority requirements and all relevant health and safety legislation.

Limitation Of Liability And Indemnity

Noble Architecture shall not be held liable for any direct indirect or consequential loss injury or damage arising from the unauthorised use of these drawings for any purpose other than obtaining town and country planning permission. The client and any subsequently appointed contractors fully indemnify Noble Architecture against any claims financial costs or legal liabilities resulting from the misuse of these drawings for construction pricing structural implementation or Building Control submissions. By proceeding with the project beyond the planning phase the client formally acknowledges the necessity of engaging appropriate technical professionals for the detailed construction phase.