




PL10 | Existing Site Context & Roof Plan

Printed Scale Factor | 1mm : 200mm | Scale Valid When Printed At : ISO 216 A

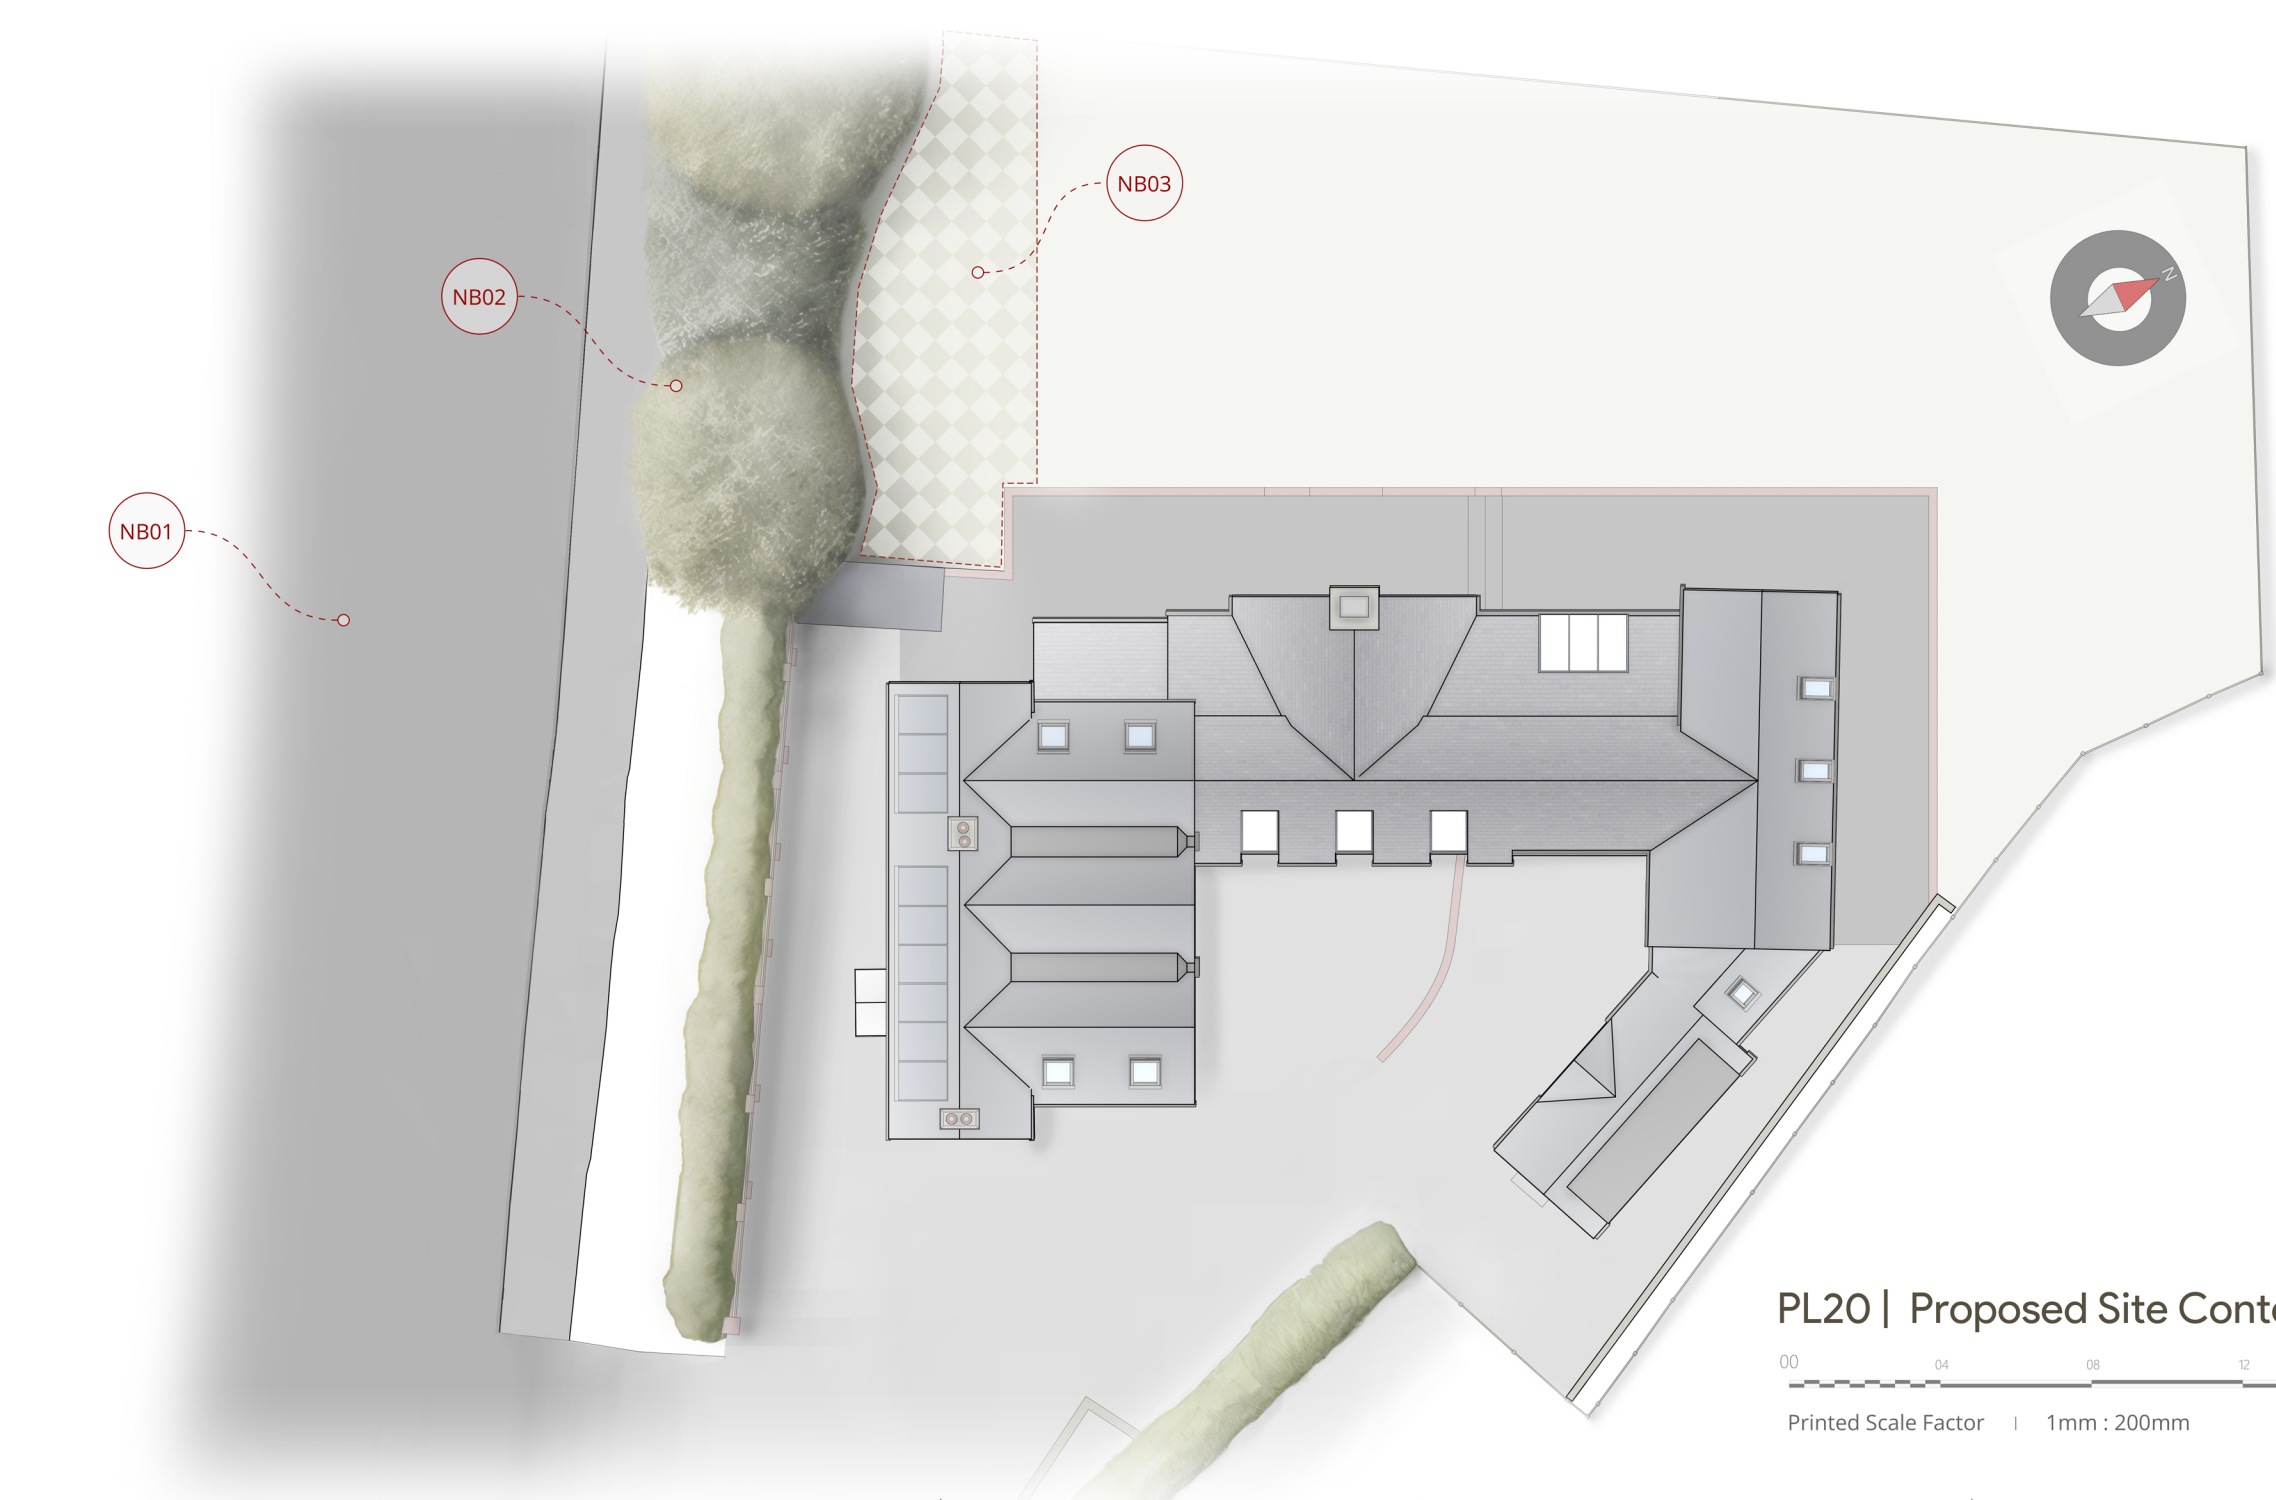


PL20 | Proposed Site Context & Roof Plan

Printed Scale Factor | 1mm : 200mm | Scale Valid When Printed At : ISO 216 A

Existing Conditions

Design Proposals

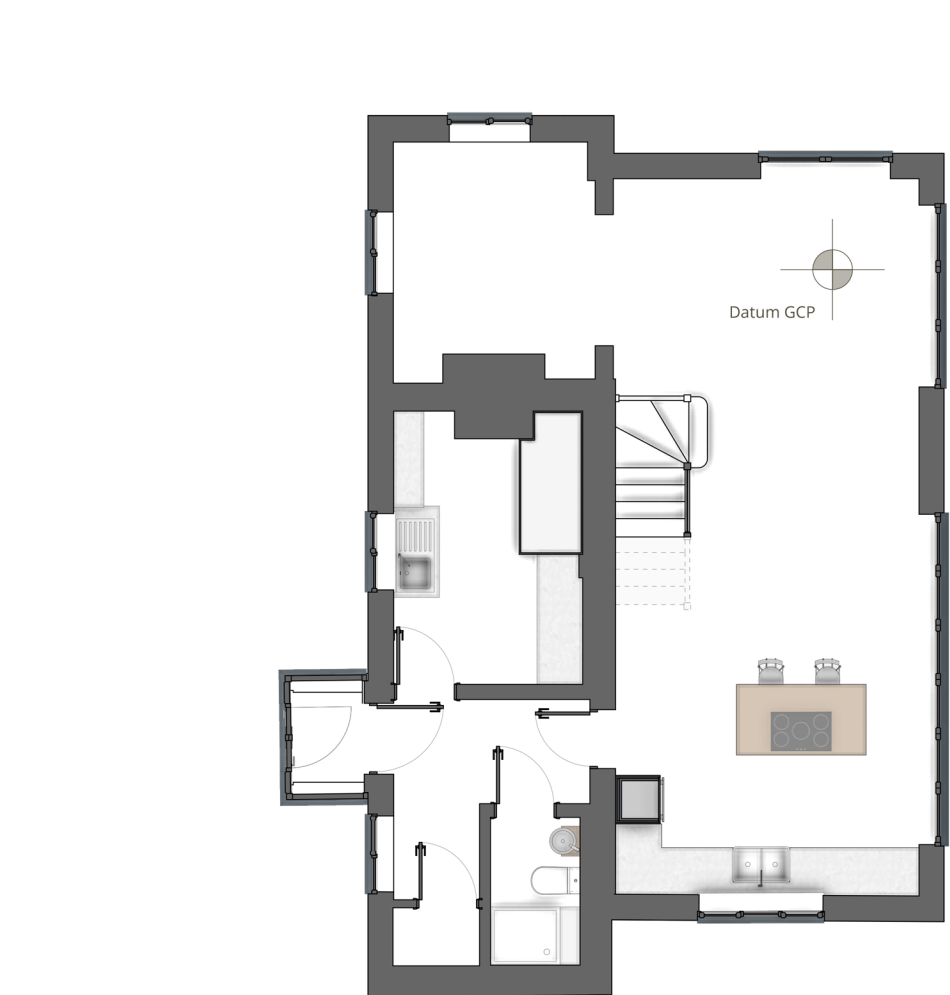

PL11 | Existing Ground Floor Layout Plan

Printed Scale Factor | 1mm : 100mm | Scale Valid When Printed At : ISO 216 A



Global Height Benchmark

Datum GCP | Ground Floor Finished Floor Level

All height measurements on this drawing are taken from the existing ground floor finished floor level, which serves as the universal site datum benchmark unless otherwise specified. Heights are set globally based on the primary ground control point established during the survey. If exact coordinates of this ground control point are required, please contact Noble Architecture.


Survey Tolerances

This project was surveyed using a SLAM Lidar Scanner, achieving the RICS survey detail accuracy of band E. Therefore, Noble Architecture can guarantee an accuracy of +/- 25mm.

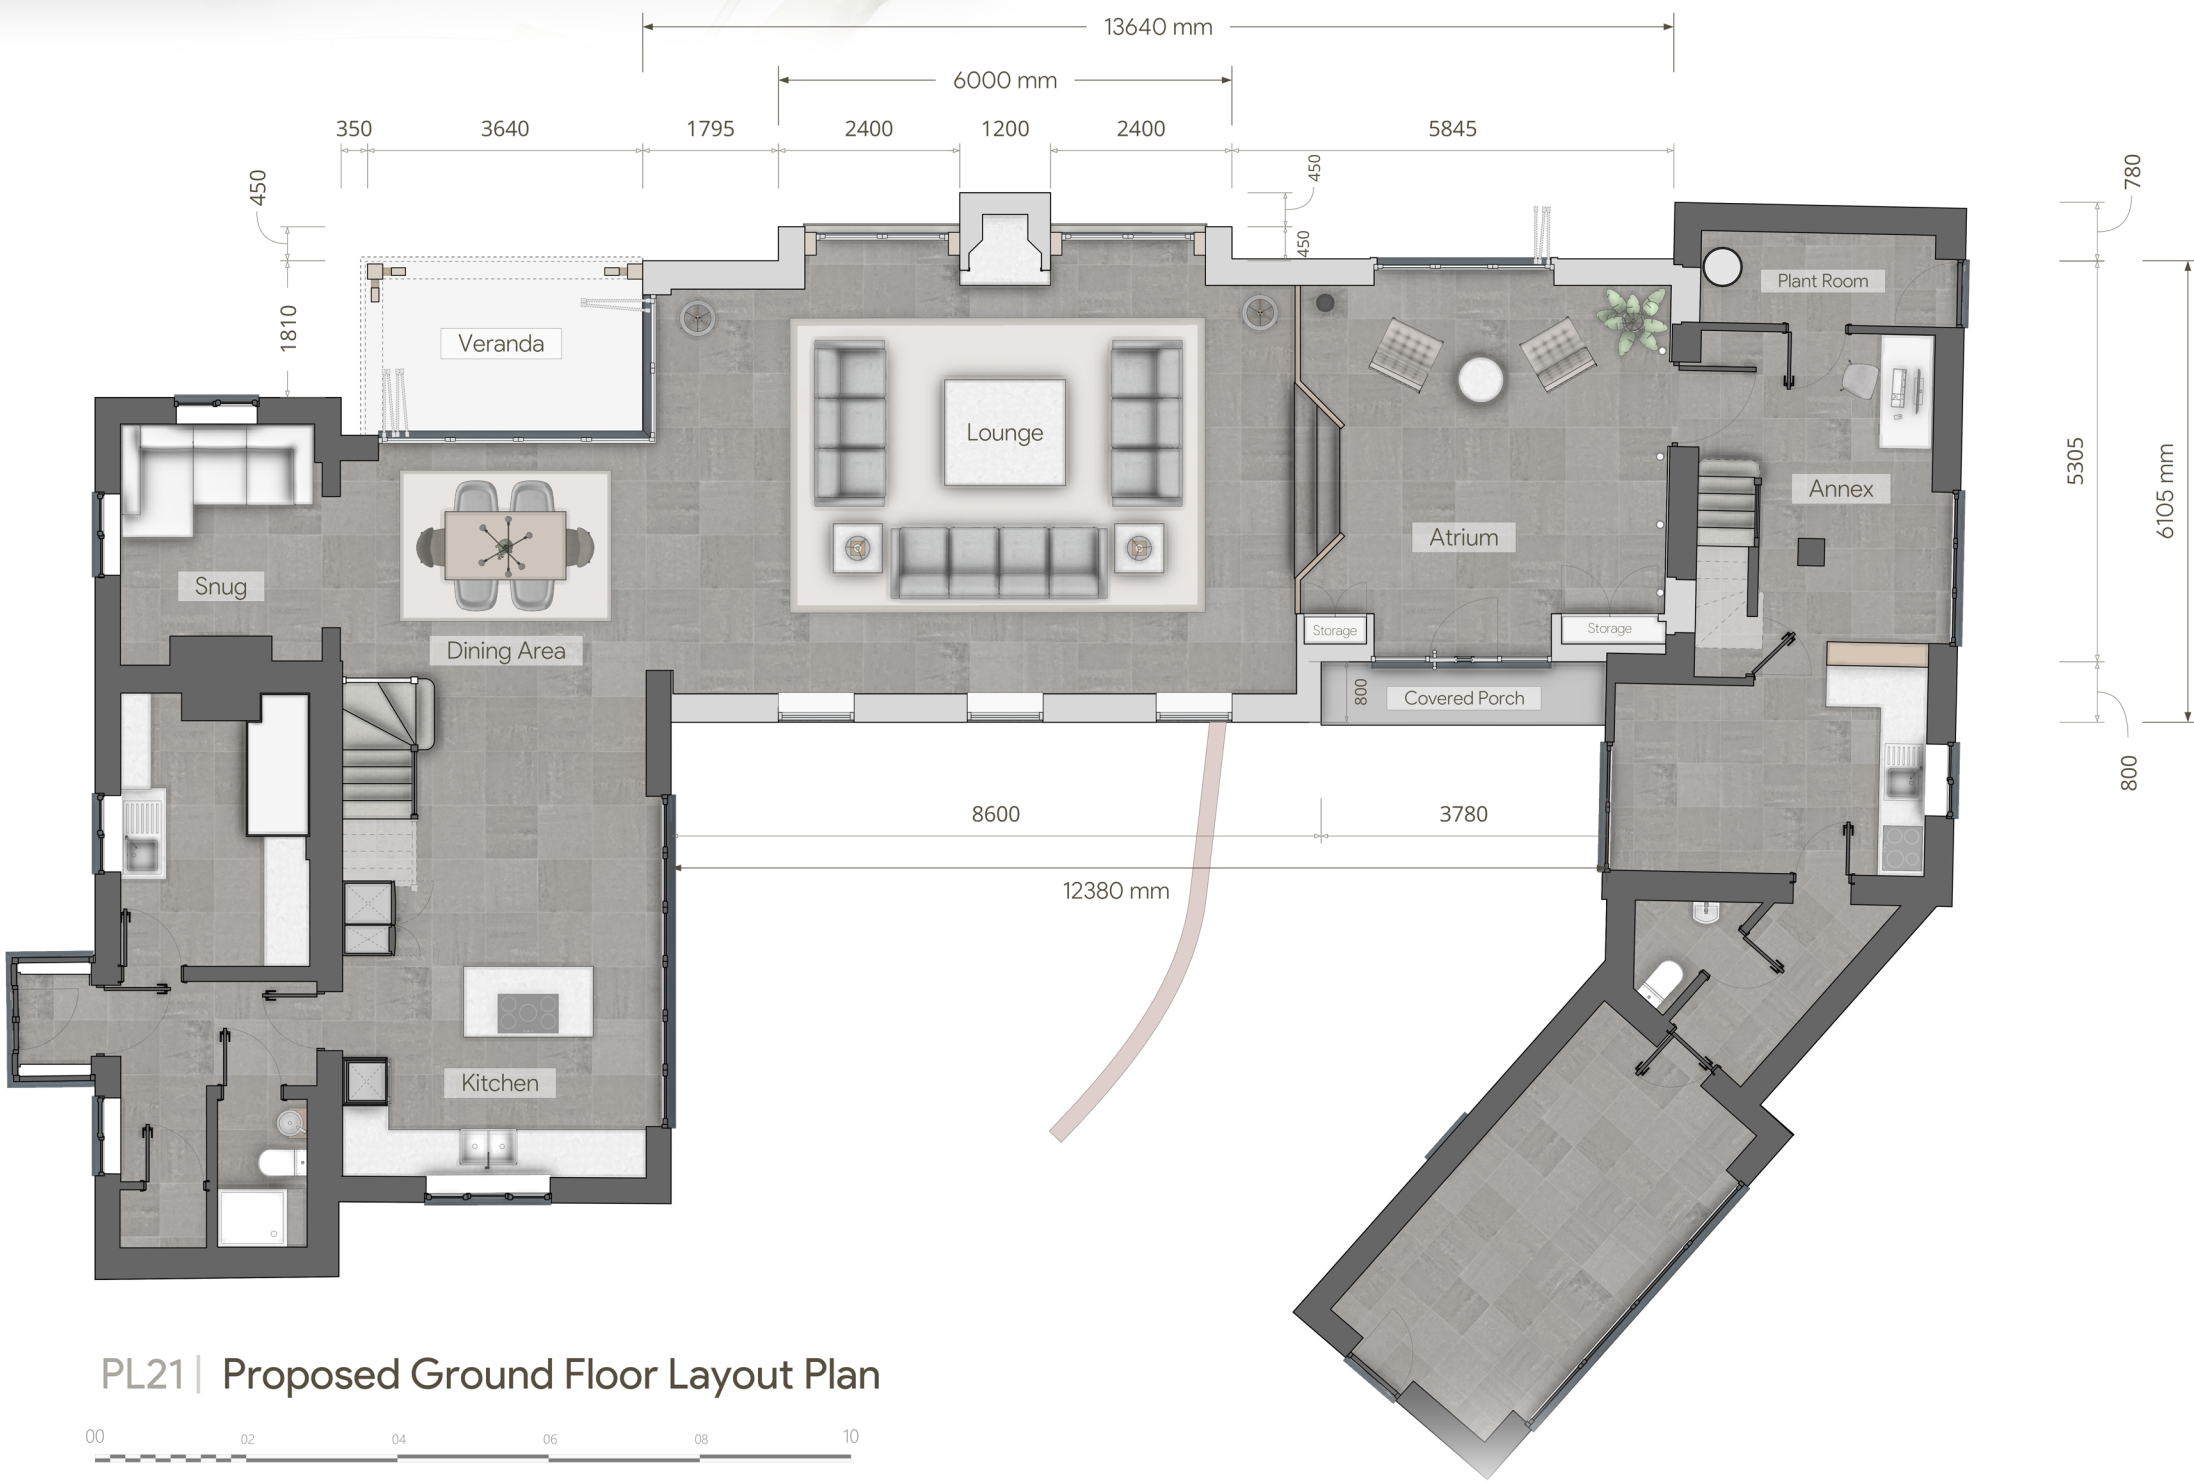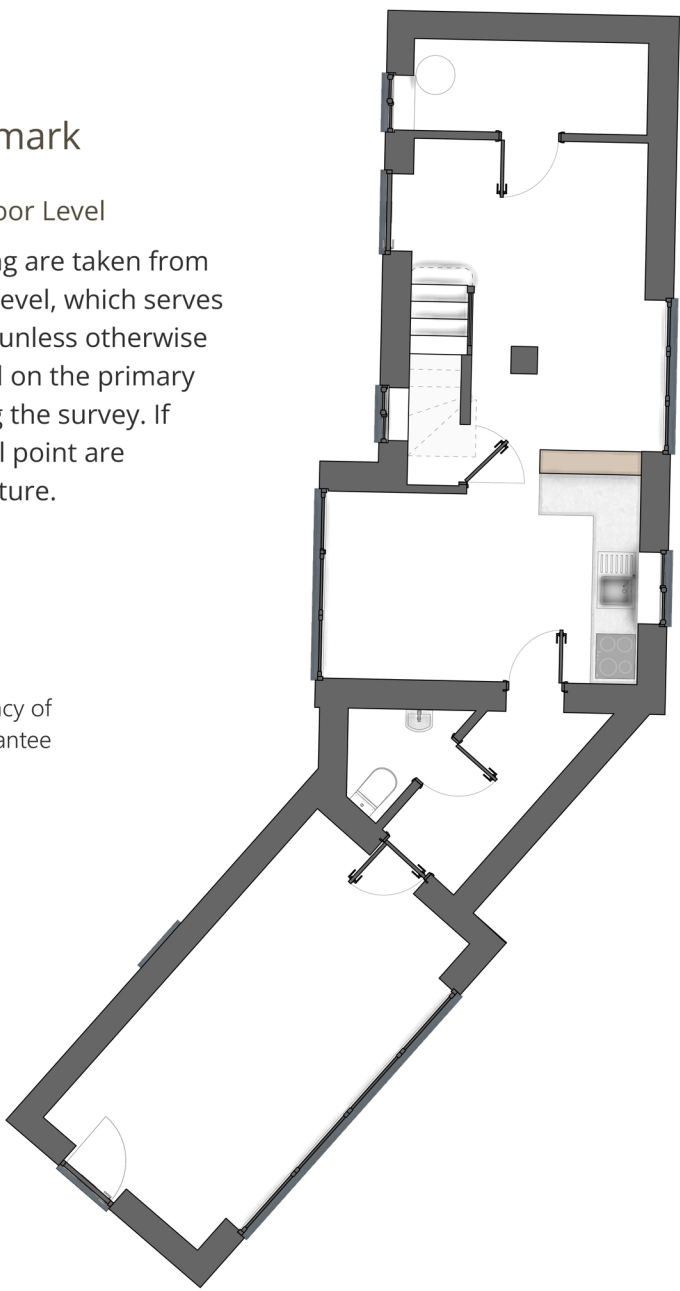

PL21 | Proposed Ground Floor Layout Plan

Printed Scale Factor | 1mm : 100mm | Scale Valid When Printed At : ISO 216 A

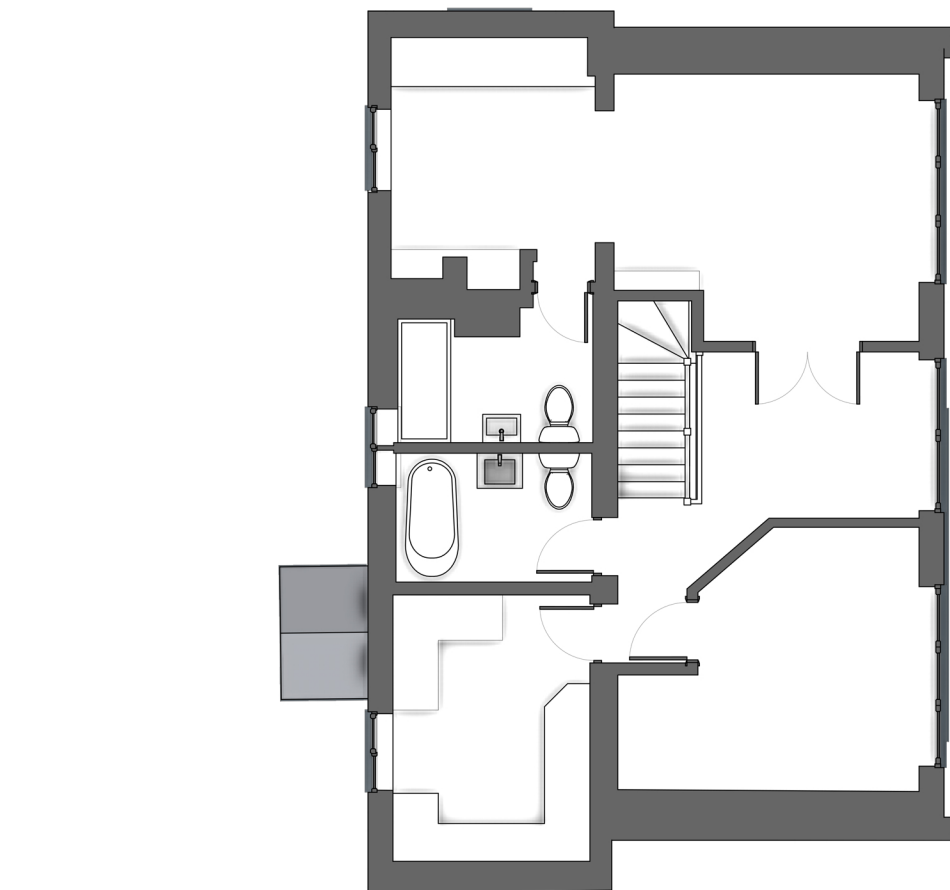

PL12 | Existing First Floor Layout Plan

PRELIMINARY DRAWING:

This plan provides a preliminary outline of the proposed scheme and is not intended for construction use. It is designed for planning officials and early stage project tendering only. Before issuing final construction drawings, further design coordination with specialists is required. Using this plan for construction is at the user's risk with no guarantees regarding its accuracy or completeness. Noble Architecture or any affiliated parties are not liable for any errors or discrepancies. By using this document for construction, the user agrees to indemnify all involved parties against claims or damages stemming from its use.

PLANNING OFFICER



Existing Site Context Photographs

Noble Architecture has compiled a comprehensive collection of site survey images, including drone photography, which are available upon request. Should these be of assistance, please reach out to Noble Architecture directly.

CONTRACTOR

Ensuring Material Consistency

The contractor is required to carefully match new materials to the existing structure, ensuring an exact match in colour, material, and texture is achieved.

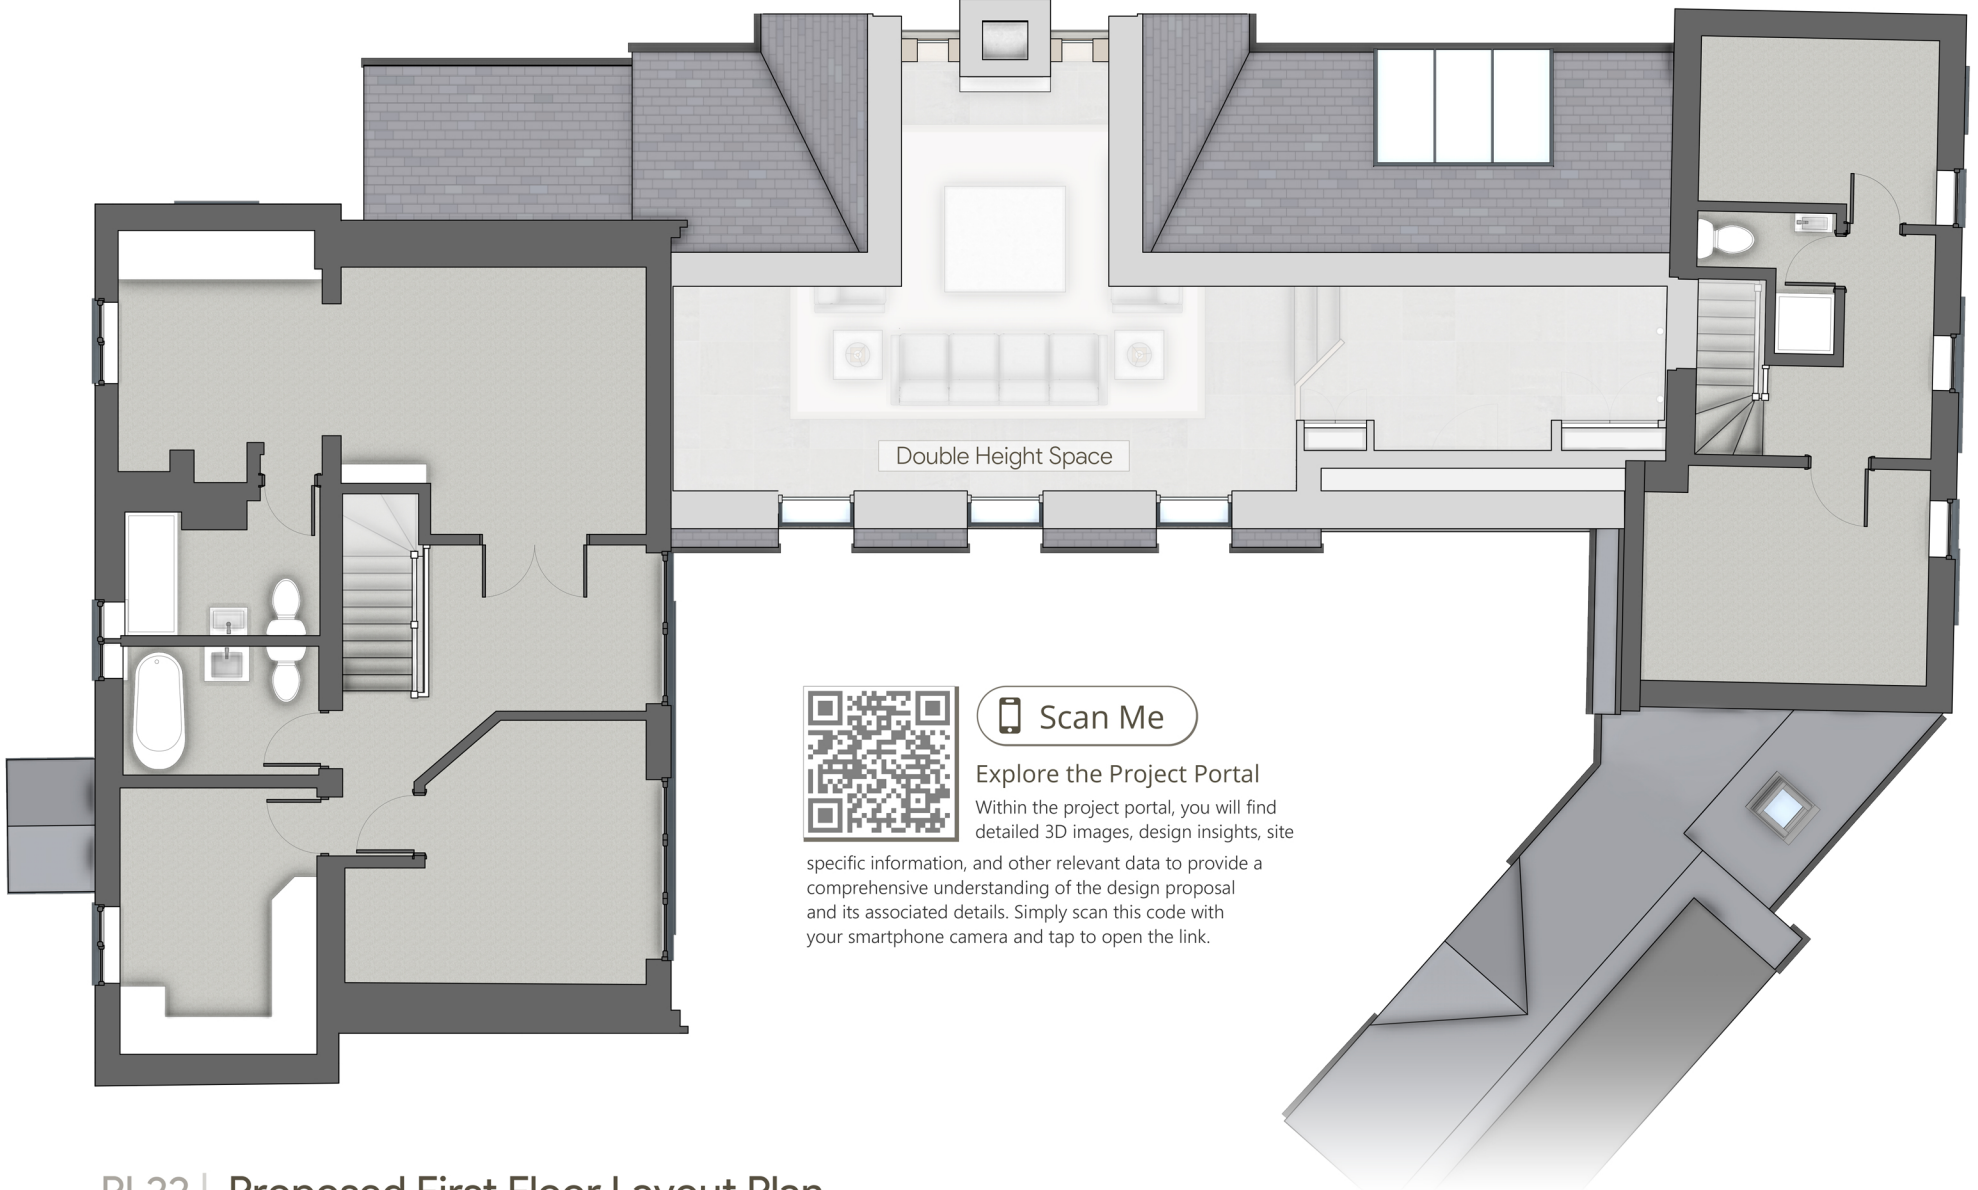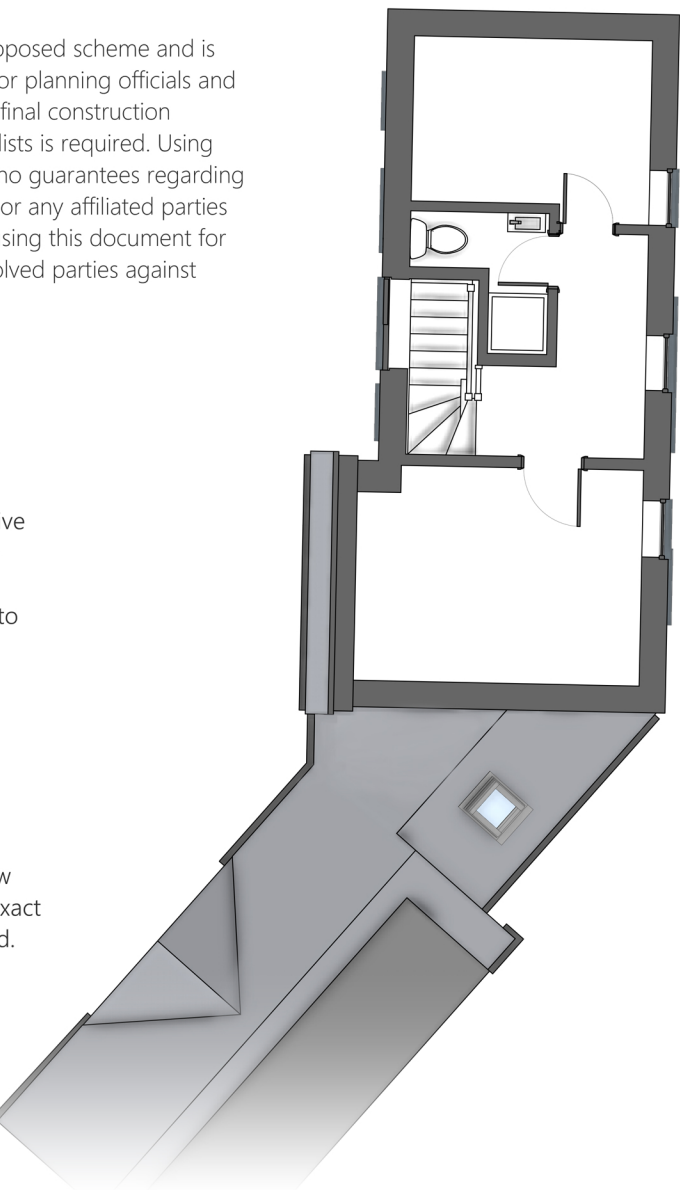

PL22 | Proposed First Floor Layout Plan



Scan Me

Explore the Project Portal
Within the project portal, you will find detailed 3D images, design insights, site specific information, and other relevant data to provide a comprehensive understanding of the design proposal and its associated details. Simply scan this code with your smartphone camera and tap to open the link.

Stafford Borough | Relevant Council Policies

Documents Referenced When Researching

- Stafford Borough Local Plan (2011-2031) | The Plan for Stafford Borough
- Design Supplementary Planning Document (SPD)

Policy N1 | Design

Emphasises the importance of high-quality design that respects the character and appearance of the surrounding area.

Relevant Context | Our selection of materials and finishes, such as weathered red brickwork and traditional slate roofing, ensures the extension harmonises with the existing structure and the local architectural vernacular, maintaining the area's character. By incorporating natural oak elements and carefully matching the existing materials, the design integrates seamlessly with the rural setting.

NB01 | The topographic height difference of the A51 means the extension will naturally appear less imposing from street level, reducing its visual impact and ensuring the design fits sensitively within the existing context.

Sustainability and Energy Efficiency

Policy N2 | Climate Change

Encourages measures that reduce energy consumption and promote sustainability in building design.

Relevant Context | The use of high-performance double or triple glazing with low-E argon-filled units in windows and doors enhances thermal efficiency, reducing energy consumption and contributing to a sustainable development. Additionally, the selection of durable, low-maintenance composite materials reduces the long-term environmental impact.

Biodiversity and Environmental Enhancement

Policy N4 | Natural Environment and Green Infrastructure

Supports initiatives to enhance biodiversity and improve green infrastructure.

Relevant Context | Our proposal includes increasing planting density in **Area NB03**, using a diverse range of plant species to create habitats for local wildlife. This contributes to the site's ecological value by providing nesting opportunities for birds and insects.

NB03 | The proposal focuses on improving the area adjacent to the boundary along the road. A new buffer zone will be created, transforming poorly draining ground into a naturally draining habitat. This aims to reduce flooding risks and help dissipate surface runoff effectively.

Landscaping and Screening

Policy N8 | Landscape Character

Highlights the importance of maintaining and enhancing local landscape character, particularly through effective planting and screening.

Relevant Context | The proposed natural sandstone patio and the use of natural materials like oak and slate ensure the development complements the existing landscape, preserving and enhancing the site's natural character. By retaining and enhancing the existing hedge along the A51 (NB02), we ensure the extension remains discreet and visually unobtrusive from public viewpoints.

NB02 | The established hedge along the A51 provides significant visual screening and will be further supplemented with additional planting, enhancing the natural boundary and softening the development's appearance.

Supplementary Planning Documents (SPDs)

Design SPD | Stafford Borough Council

Encourages careful consideration of materials, finishes, and detailing to ensure new developments are in harmony with their surroundings.

Relevant Context | The careful selection of materials, such as matching brickwork and traditional slate tiles, aligns with the Design SPD's emphasis on respecting local architectural styles and ensuring visual continuity with the existing building. The use of natural stone for the feature chimney further reinforces the high-quality design while creating a key focal point.

Application-Specific Notes

Visual Impact

Policy Compliance | Our commitment to maintaining and enhancing natural screening addresses concerns under Policy N8 and the Design SPD, ensuring the extension does not negatively impact the local landscape. The topographic difference of the A51 (NB01) further minimises the visual prominence of the extension from street level.

Environmental Enhancements

Policy Compliance | Biodiversity improvements, particularly in NB03, align with Policies N2 and N4, demonstrating our commitment to sustainable development and ecological enhancement.

Landscape Integration

Policy Compliance | The design's consideration of local landscape character, enhanced by material selection and strategic planting, ensures the extension integrates seamlessly with its surroundings, supporting Policy N8 and the Design SPD.

Design Impact Summary

Our proposal reflects Stafford Borough Council's planning priorities by adhering to design, sustainability, and landscape policies. By addressing key site characteristics such as the topographic height difference (NB01), retaining and enhancing existing foliage (NB02), and improving biodiversity (NB03), the design ensures a cohesive, environmentally responsible, and aesthetically pleasing & context sensitive home extension.