



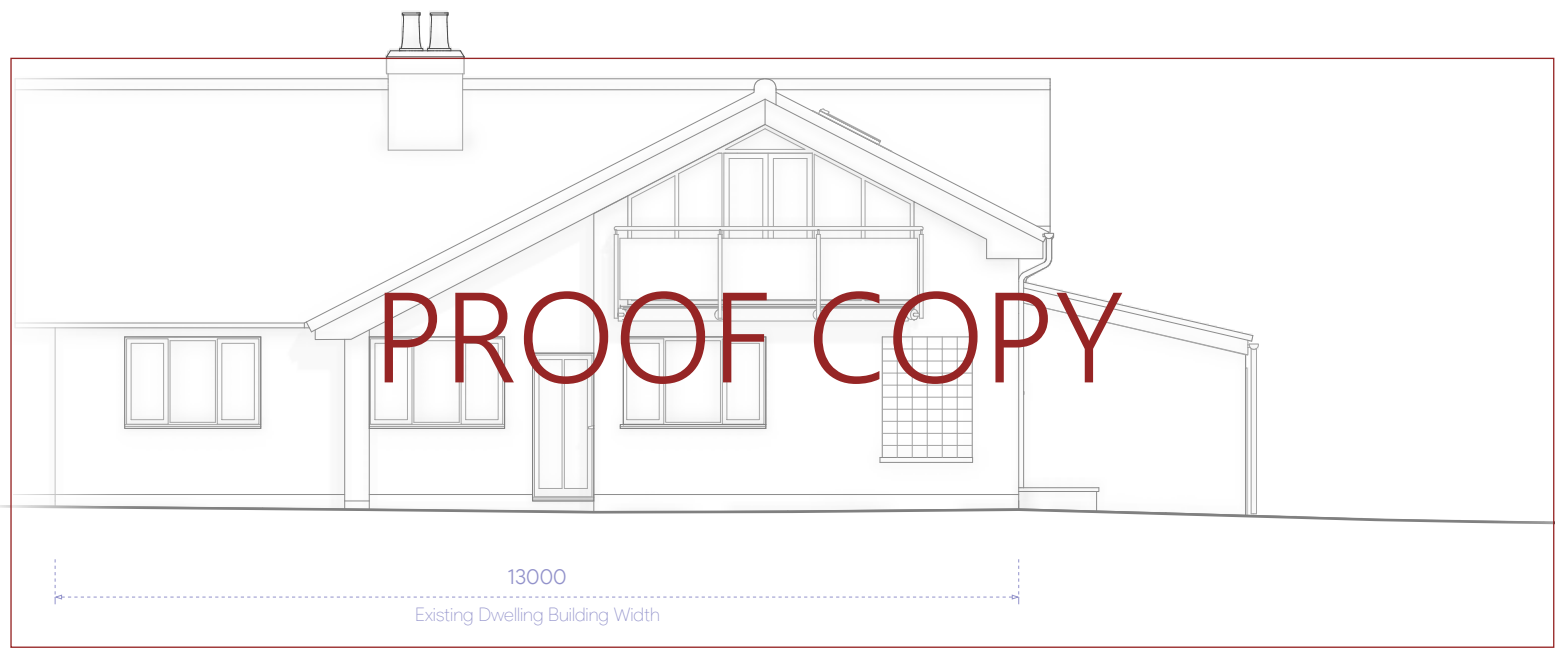


Existing East Elevation – Dwelling Frontage

00 02 04 06 08 10
Printed Scale Factor | 1mm : 100mm | Scale Valid When Printed At : ISO 216 A2

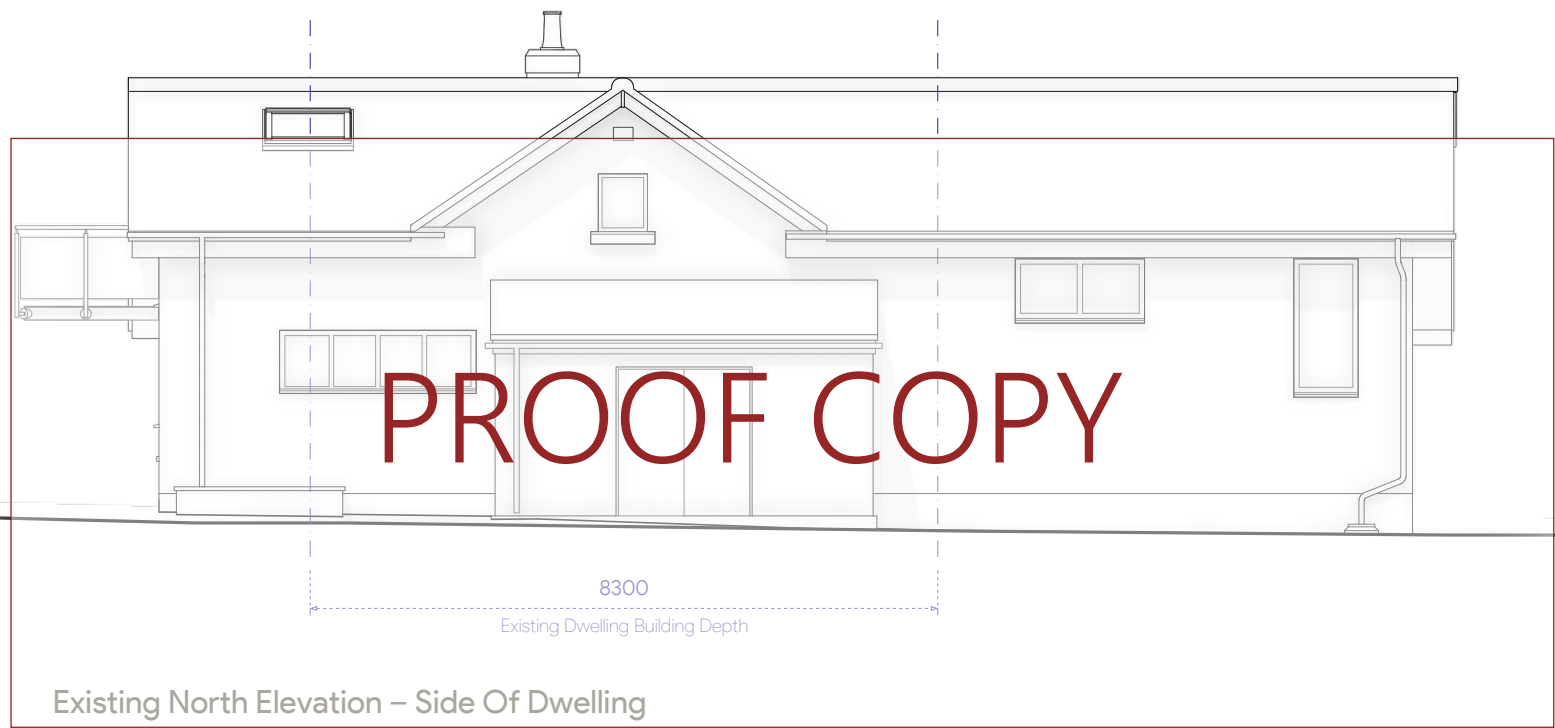

Existing North Elevation – Side Of Dwelling

00 02 04 06 08 10
Printed Scale Factor | 1mm : 100mm | Scale Valid When Printed At : ISO 216 A2

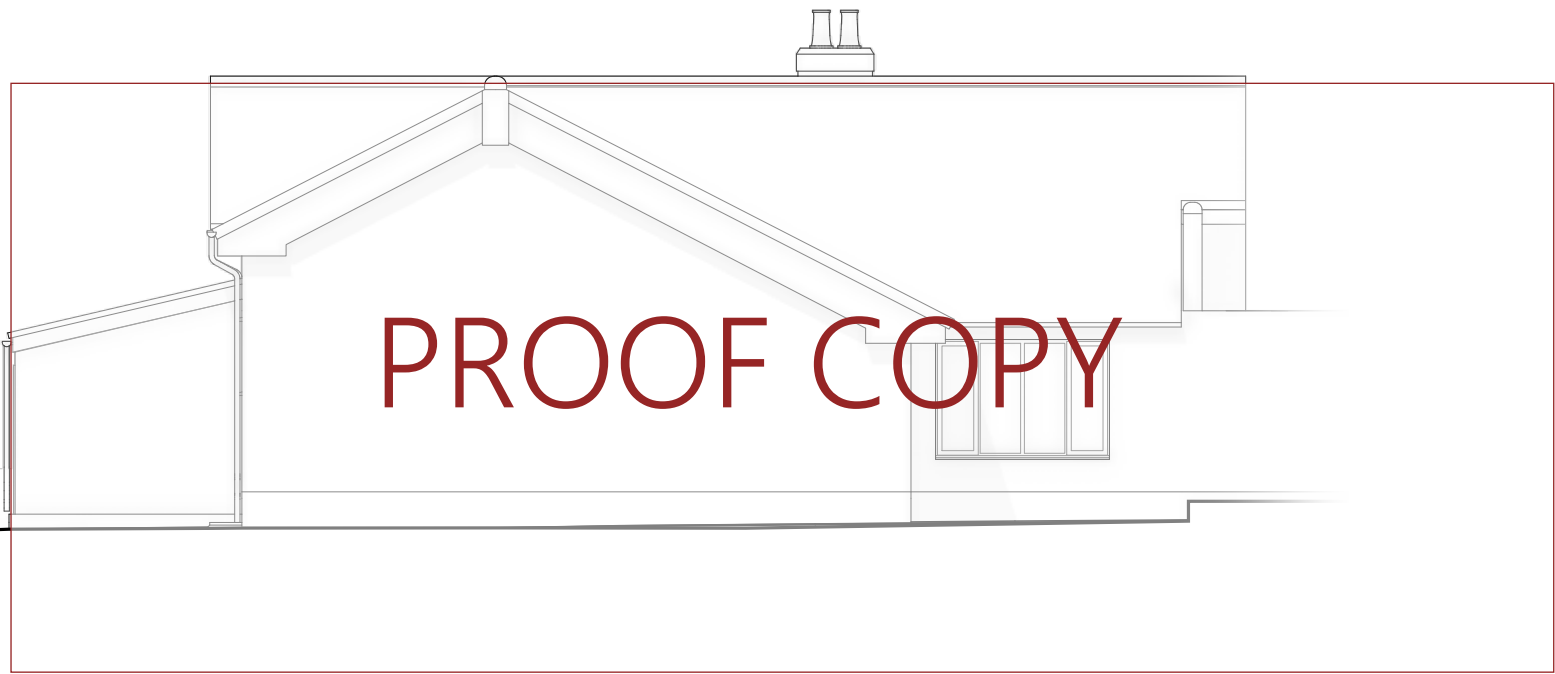

Existing West Elevation – Rear Of Dwelling

00 02 04 06 08 10
Printed Scale Factor | 1mm : 100mm | Scale Valid When Printed At : ISO 216 A2


PRELIMINARY DRAWING:

This plan provides a preliminary outline of the proposed scheme and is not intended for construction use. It is designed for planning officials and early stage project tendering only. Before issuing final construction drawings, further design coordination with specialists is required. Using this plan for construction is at the user's risk with no guarantees regarding its accuracy or completeness. Noble Architecture or any affiliated parties are not liable for any errors or discrepancies. By using this document for construction, the user agrees to indemnify all involved parties against claims or damages stemming from its use.

PLANNING DEPARTMENT


Existing Site Context Photographs

Noble Architecture has compiled a comprehensive collection of site survey images, including drone photography, which are available upon request. Should these be of assistance, please reach out to Noble Architecture directly.

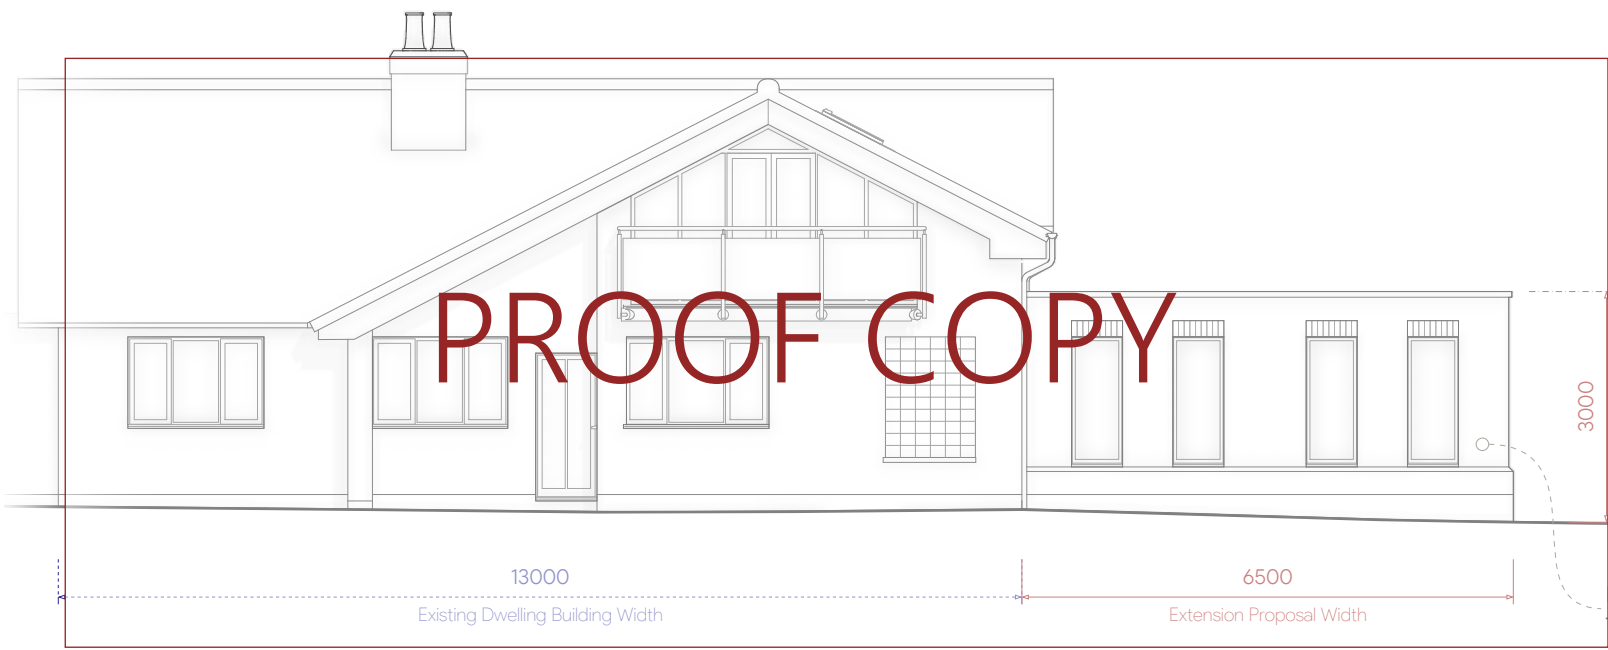


Proposed East Elevation – Dwelling Frontage & Front Of Extension

00 02 04 06 08 10
Printed Scale Factor | 1mm : 100mm | Scale Valid When Printed At : ISO 216 A2

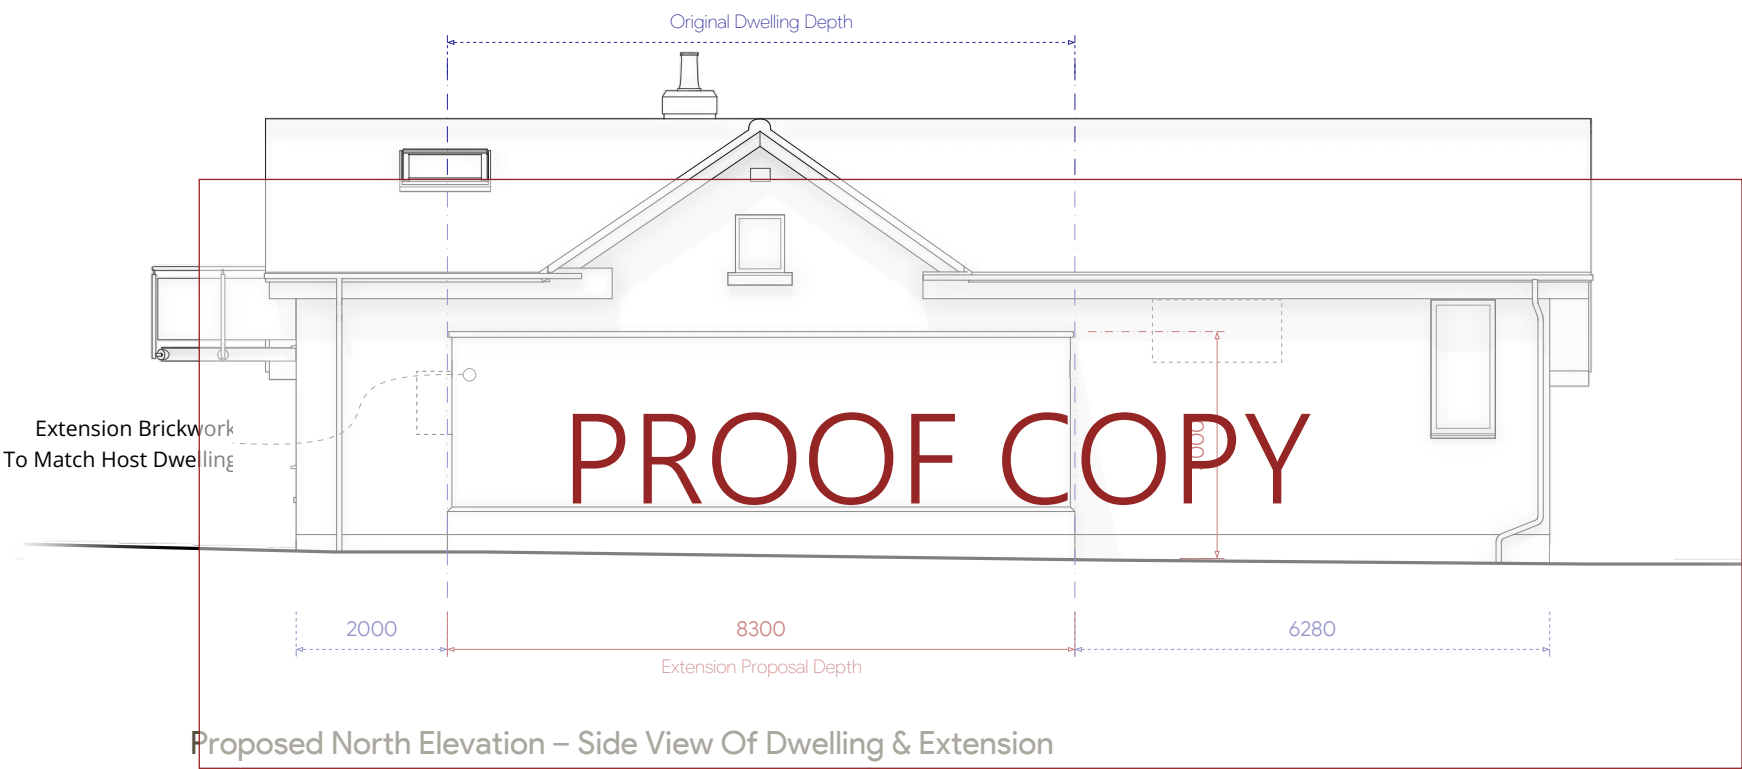

Proposed North Elevation – Side View Of Dwelling & Extension

00 02 04 06 08 10
Printed Scale Factor | 1mm : 100mm | Scale Valid When Printed At : ISO 216 A2

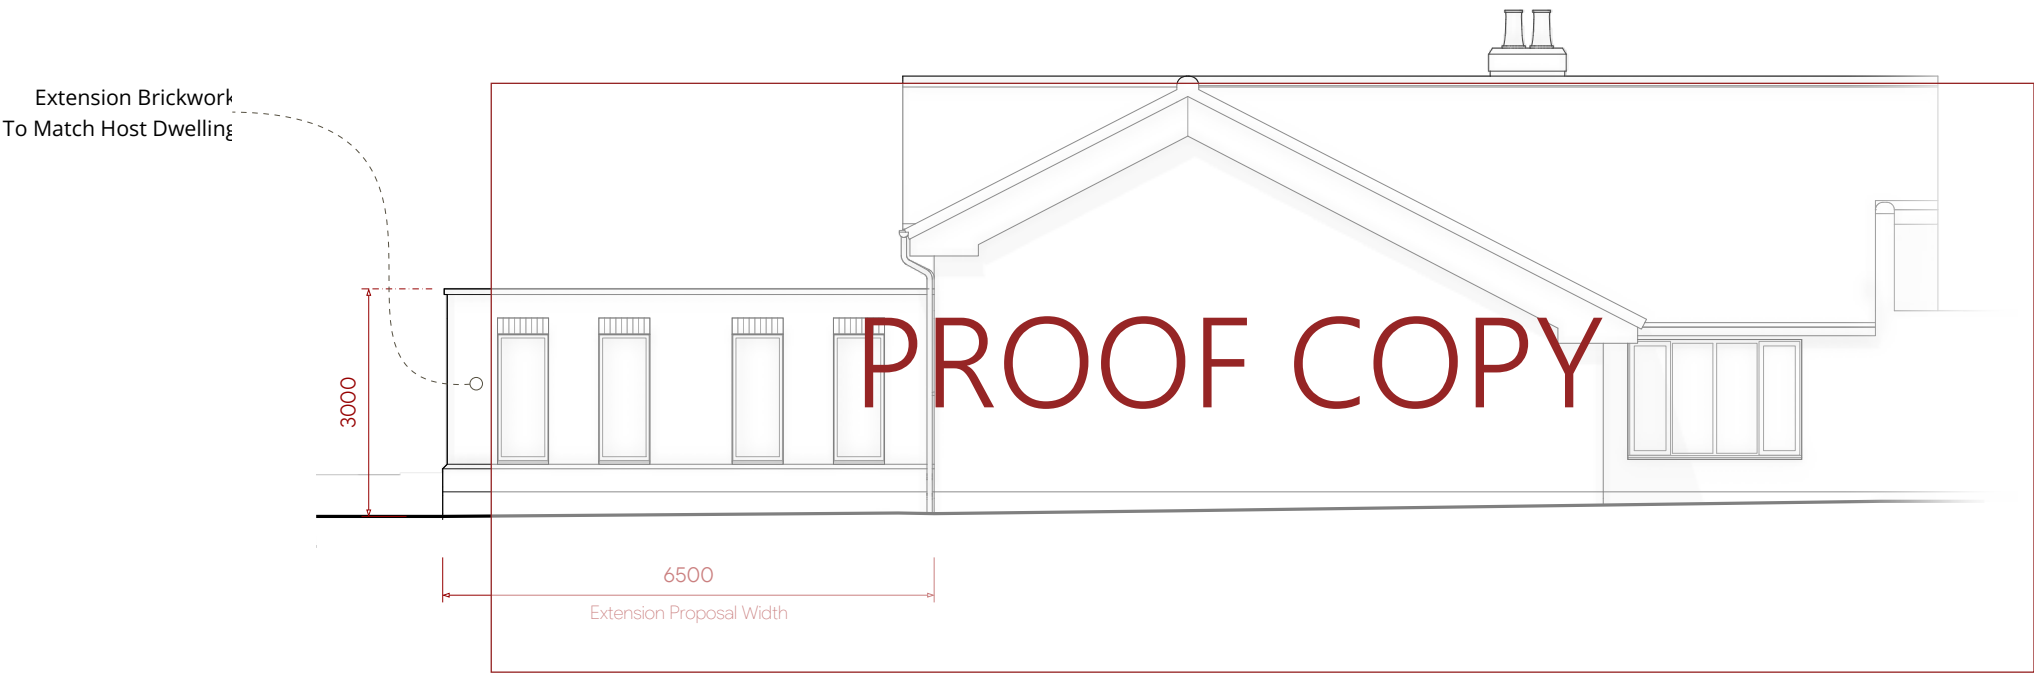

Proposed West Elevation – Rear View Of Dwelling & Extension

00 02 04 06 08 10
Printed Scale Factor | 1mm : 100mm | Scale Valid When Printed At : ISO 216 A2

CONTRACTOR

Ensuring Material Consistency

The contractor is required to carefully match new materials to the existing structure, ensuring an exact match in colour, material, and texture is achieved.