




Use your phone or tablet camera

[View Project Portal](#)

- Walk Through the 3D Model
- Saved Scenes and Viewpoints
- Measuring Tools
- Live Drawings Online

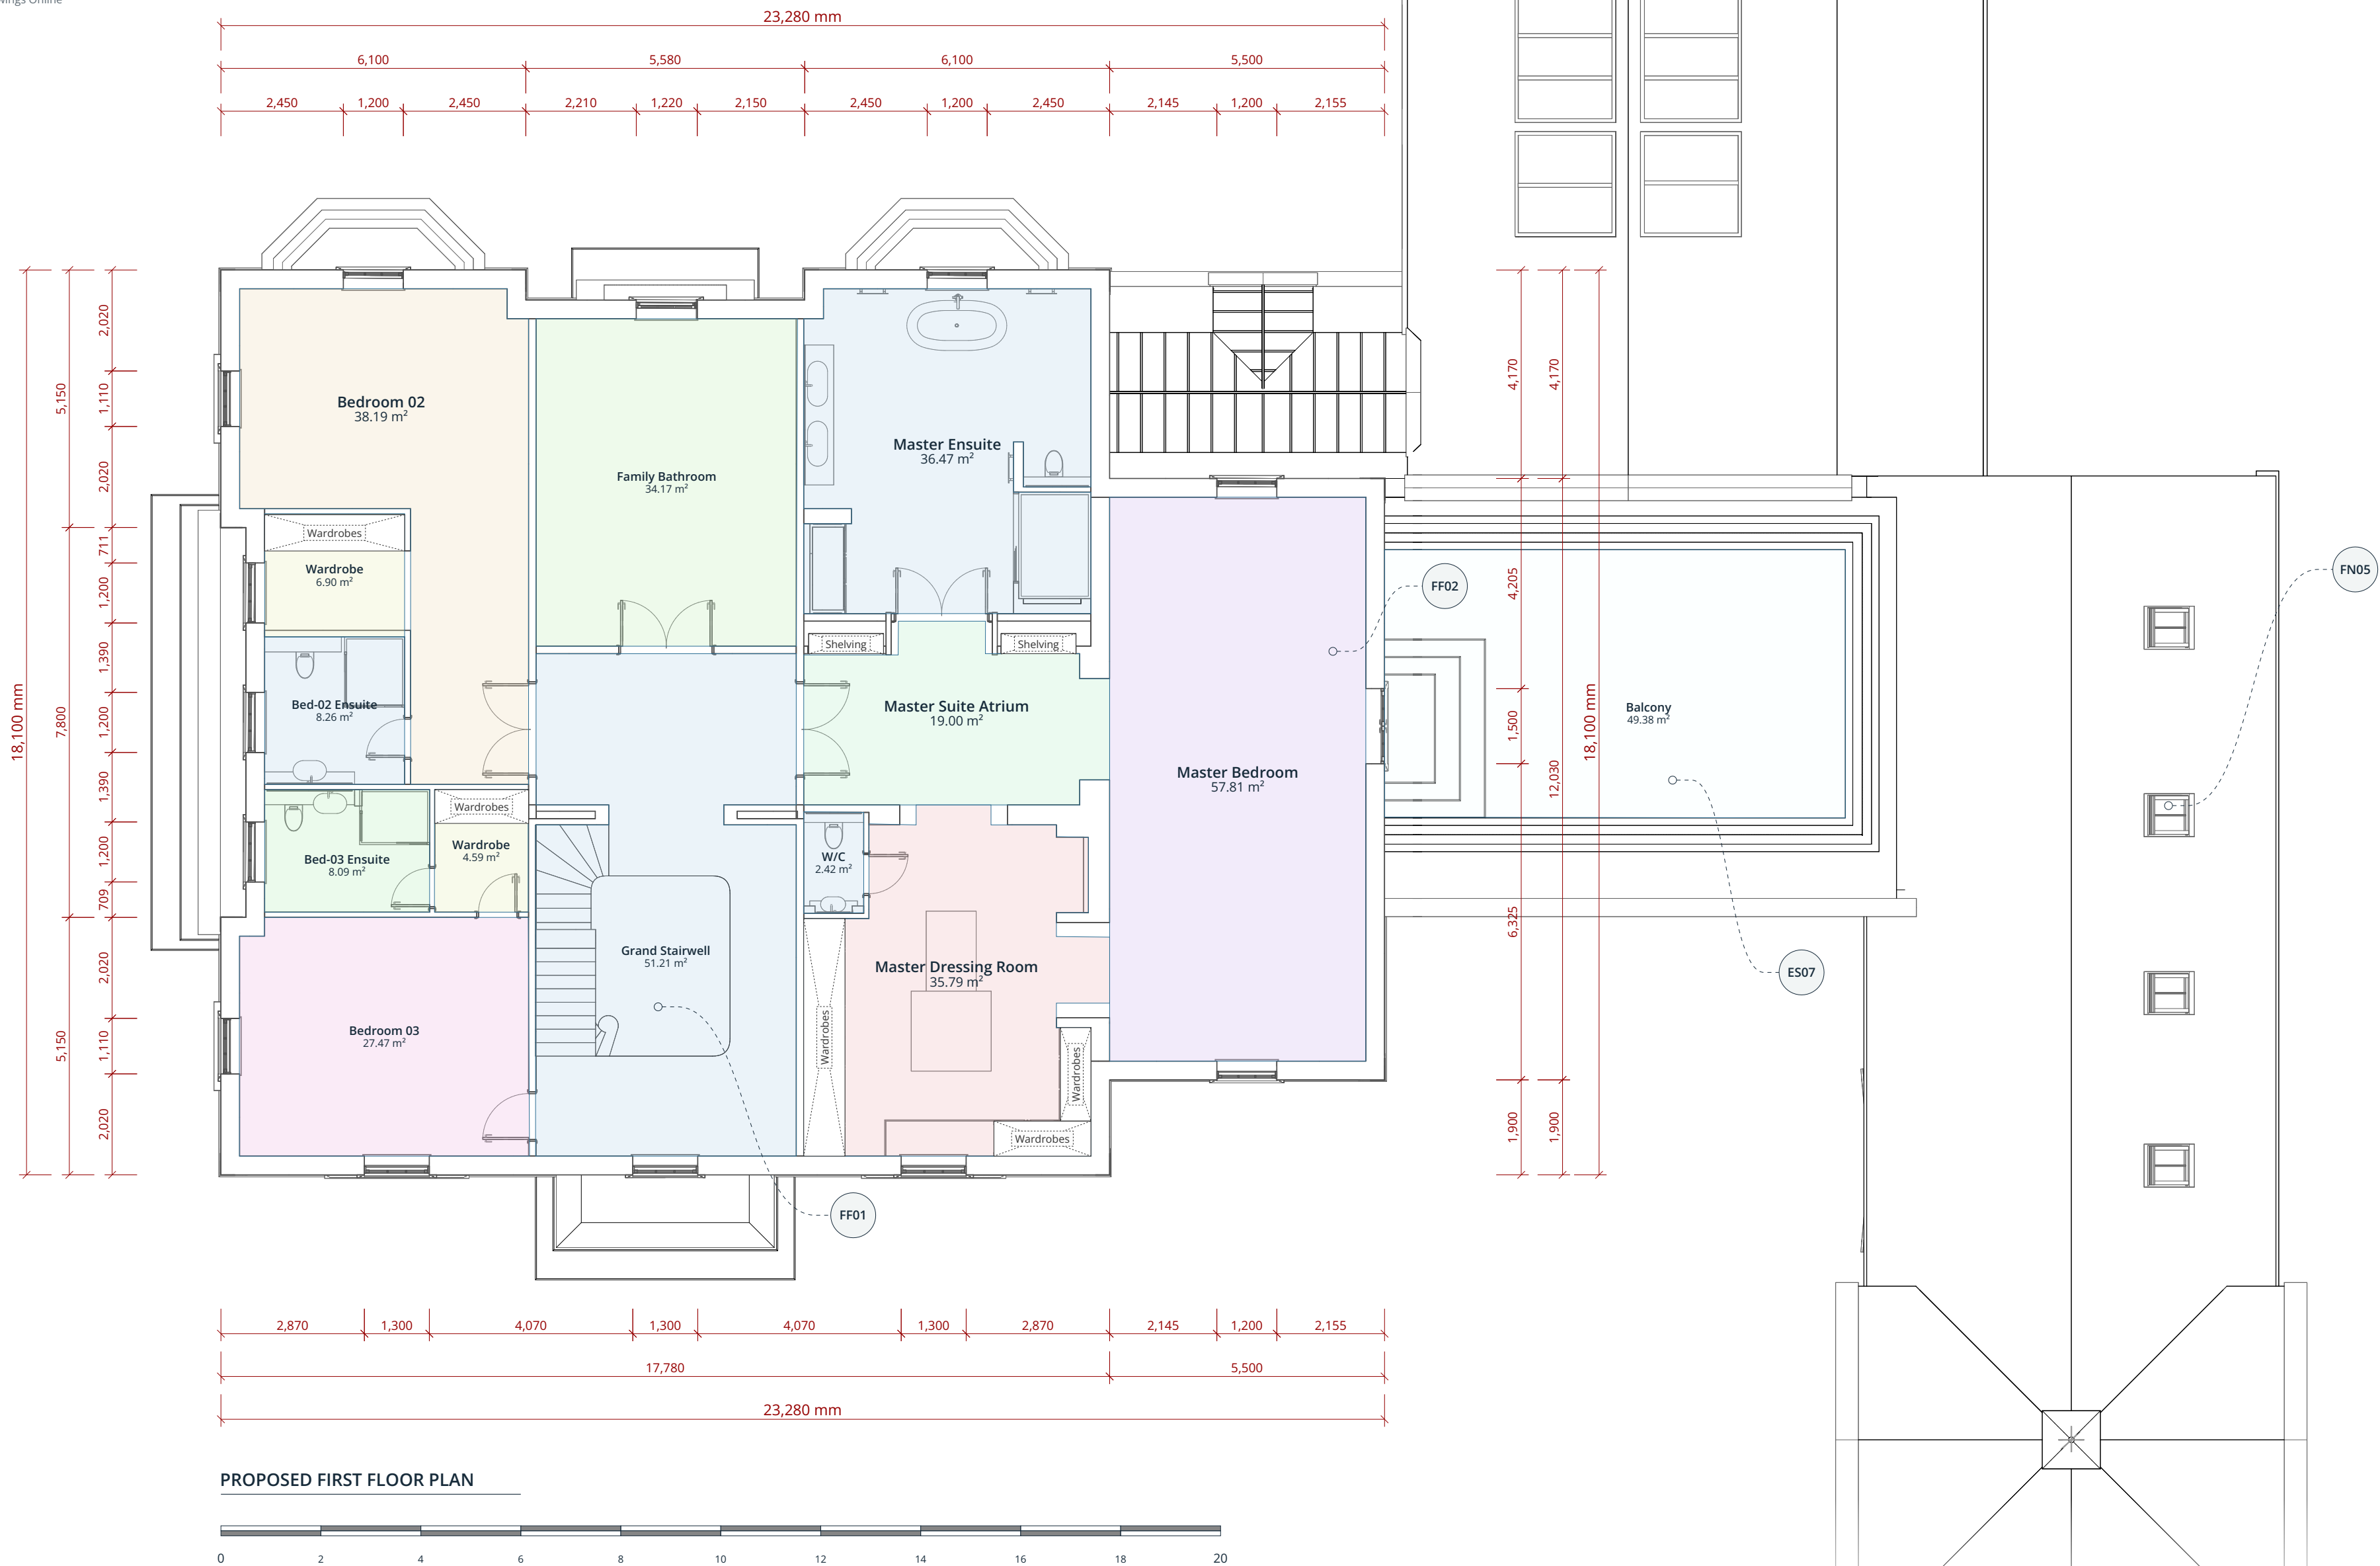

NOTES

ES07 | Colonnade Balcony

Balcony over the colonnade entrance, reached down steps from the master bedroom suite. Parapet set back from the face below, with planting beds to the edges in place of a balustrade. The set-back keeps the balcony reading as the colonnade roof from ground level. Refer to the three-dimensional model on the project portal.

FN05 | Rooflights

Conservation pattern rooflights set flush within the roof plane to the coach house
Kitchen building apex rooflights as EN06. Product to be confirmed before a full
application.

FF01 | Stairwell void and lantern

Grand Stairwell: void through the first and second floors over the Grand Atrium, beneath the ridge lantern as ES04. Daylight from the lantern reaches the ground floor.

FF02 | Master suite

Master suite at the north east end of the first floor. The Master Bedroom leads out onto the colonnade balcony, as ES07.

GN01 | Drawing Scope

Drawings describe the proposed development for planning assessment. They are not construction drawings or a complete Building Regulations specification. Obtain coordinated construction details, structural calculations and Building Control approval before relevant work starts. Refer discrepancies to Noble Architecture before proceeding.

GN02 | Survey And Dimensions

Site information derived from a photogrammetric aerial survey of the holding, with purchased Ordnance Survey data to the site plans. No measured building survey of the existing dwelling has been carried out. Proposed buildings are derived from Noble Architecture's three-dimensional model. Do not scale from these drawings. Verify all dimensions on site.

GN03 | Pre-Application Status

Issued for pre-application advice. Materials, dimensions and levels are indicative at this stage and to be fixed before a planning application.

Floor Areas

Room	Area
First Floor - Main House	330.39 m²
Bedroom 02	38.19 m²
Wardrobe	6.90 m²
Bed-03 Ensuite	8.09 m²
Wardrobe	4.59 m²
Bedroom 03	27.47 m²
Grand Stairwell	51.21 m²
Family Bathroom	34.17 m²
Master Ensuite	36.47 m²
Master Bedroom	57.81 m²
Master Suite Atrium	19.00 m²
Master Dressing Room	35.79 m²
W/C	2.43 m²
Bed-02 Ensuite	8.26 m²
Total	330.39 m²

Floor Areas

Room	Area
First Floor - Main House	3,556 ft²
Bedroom 02	411 ft²
Wardrobe	74 ft²
Bed-03 Ensuite	87 ft²
Wardrobe	49 ft²
Bedroom 03	296 ft²
Grand Stairwell	551 ft²
Family Bathroom	368 ft²
Master Ensuite	393 ft²
Master Bedroom	622 ft²
Master Suite Atrium	204 ft²
Master Dressing Room	385 ft²
W/C	26 ft²
Bed-02 Ensuite	89 ft²
Total	3,556 ft²

