

NOTES

EN01 | Entrance Composition
Central entrance: six-panel painted timber door with narrow sidelights, on cut ashlar jambs standing on plinth blocks. A deep moulded entablature with projecting cornice sits above, and a semicircular radial fanlight above that, framed by concentric moulded archivolts.

EN02 | Canted Bay Windows
Canted bays flank the entrance, in cut ashlar throughout, with a moulded cornice and blocking course at the head. French doors to the centre face and sashes to the played returns, opening onto the terrace.

EN04 | Orangery Link
Orangery between the house and the kitchen building: painted timber, glazed the full height of its bays, under a bespoke glazed lantern, applicant to consider a traditional manufacturer such as Vale Garden House who can provide the level of finish required for such a bespoke painted hardwood orangery structure..

EN05 | Kitchen Building Gable Openings
Kitchen building gable: two tall arched openings with radial fanlights in cut ashlar surrounds. Stone chimney stack against the gable.

EN06 | Kitchen apex rooflights
Kitchen building: glazed apex rooflights to both roof slopes at the ridge, set flush with the roof covering of FN03 in the manner of conservation rooflights. They light a vaulted ceiling with exposed roof timbers. Frame material, finish and product to be confirmed before a full application.

ES01 | Entrance Porch
Central entrance: a pair of Tuscan columns on plinth blocks carry a full entablature with a projecting moulded cornice. Beneath it a six-panel painted timber door with a semicircular radial fanlight, dressed in cut ashlar and approached over stone steps. The porch projects slightly from the wall plane.

ES05 | Colonnade Entrance
Single-storey colonnade entrance to the right of the main block: Tuscan columns flanking a glazed painted timber door, with flat ashlar lintels over the windows either side, beneath a flat roof with a moulded cornice. Leads through to the kitchen building and the coach house.

ES08 | Coach House External Stair
Indicative external staircase to the accommodation over the coach house, shown to establish the access only. Form, construction and finish to be confirmed before a full application.

EE02 | Lean-To Store
Single-storey lean-to store against the kitchen building, under a mono-pitch roof with eaves set below those of the kitchen building. Horizontal timber weatherboarding to the walls. Ancillary storage for garden furniture and pool equipment. Roof covering to be confirmed before a full application.

EW01 | Loggia Arcade
Three arched openings in a recessed bay at ground floor. Tuscan columns, with matching responds returned against the flanking walls, carry a full entablature with plain frieze and projecting cornice. French doors beneath radial fanlights to each arch. The arcade is recessed within the wall plane and does not project beyond the elevation.

FN01 | Walling Stone
Coursed squared natural stone walling to the external walls of the house, the kitchen building and the coach house. Rough faced and laid to courses, with the dressed elements in cut ashlar of the same stone as FN10, FN11 and FN12. Stone type and source to be confirmed before a full application.

FN02 | Classical Order
All columns and pilasters are of the Tuscan order in cut ashlar: the entrance porch, the loggia arcade and the colonnade entrance.

FN03 | Roof Covering
Natural stone slate laid to diminishing courses to all pitched roofs. Stone slate type, and whether new or reclaimed, to be confirmed before a full application.

FN04 | Chimney Stack
Natural stone chimney stacks with moulded caps to the house, the kitchen building and the coach house.

FN05 | Rooflights
Conservation pattern rooflights set flush within the roof plane to the coach house. Kitchen building apex rooflights as EN06. Product to be confirmed before a full application.

FN06 | Windows And Joinery
External joinery painted timber with slender glazing bars, to a single pattern across every building in the group. Pane configuration and paint colour to be confirmed before a full application.

FN07 | External Doors
Painted timber six-panel entrance doors with radial fanlights to the house. French doors to the loggia, the terraces and the orangery. Boarded and strapped timber doors to the coach house.

FN08 | Oak Weatherboard Cladding
Weathered oak shiplap cladding to the lean-to store, laid horizontally, with vertically boarded and strapped doors. Left untreated to silver naturally. Board profile, lap and fixings to be confirmed before a full application.

FN09 | Classical Entablatures
Full Tuscan entablature to the entrance porch, the loggia arcade and the colonnade entrance: plain architrave, unornamented frieze and projecting moulded cornice. Order as FN02. Profiles and proportions to be confirmed before a full application.

FN10 | Ashlar Quoins
Cut ashlar quoins of the same stone as the walling to every external angle of the house, the kitchen building and the coach house. Laid in alternating long and short courses. Finely dressed to contrast with the coursed walling of FN01. Coursing module and margin widths to be confirmed before a full application.

FN11 | Ashlar Plinth
Cut ashlar plinth of the same stone as the walling running continuously around the base of the house, the kitchen building and the coach house, returned at all projections and terminated against the external ground level. Height, projection and weathering detail to be confirmed before a full application.

FN12 | Cut Ashlar Dressings
Cut ashlar dressings of the same stone as the walling to the window and door surrounds, cills, eaves cornice, canted bays, the two entrance compositions and the carriage arch. Finely dressed and moulded where shown. Profiles to be confirmed before a full application.

CE02 | Carriage Arch
Central gabled bay carries a semicircular carriage arch turned in voussiors with a projecting keystone, on cut ashlar impostes with quoined jambs. The arch carries the pedestrian and service route through from the courtyard.

CE03 | Gable Oculus
Circular louvred oculus in the gable above the arch, set in a cut ashlar surround with four projecting keyblocks.

CE04 | Cupola
Cupola on the ridge above the gable: square base with an arched louvred opening and a moulded cornice, pyramidal roof, ball finial and weathervane. Material and finish to be confirmed before a full application.

GN01 | Drawing Scope
Drawings describe the proposed development for planning assessment. They are not construction drawings or a complete Building Regulations specification. Obtain coordinated construction details, structural calculations and Building Control approval before relevant work starts. Refer discrepancies to Noble Architecture before proceeding.

GN02 | Survey And Dimensions
Site information derived from a photogrammetric aerial survey of the holding, with purchased Ordnance Survey data to the site plans. No measured building survey of the existing dwelling has been carried out. Proposed buildings are derived from Noble Architecture's three-dimensional model. Do not scale from these drawings. Verify all dimensions on site.


GN03 | Pre-Application Status
Issued for pre-application advice. Materials, dimensions and levels are indicative at this stage and to be fixed before a planning application.



PROPOSED WEST FACADE - SIDE FACING



PROPOSED SOUTH FACADE - FRONT FACING

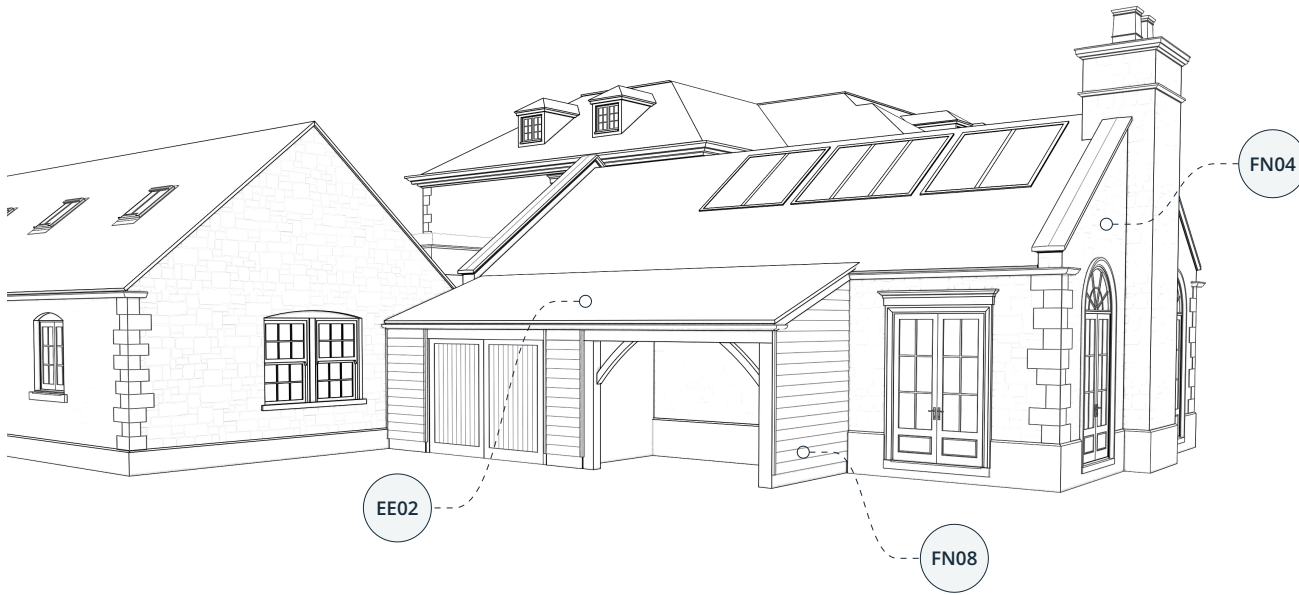


PROPOSED EAST - STORAGE



PROPOSED NORTH FACADE - REAR FACING



PROPOSED NORTH - ORANGERY

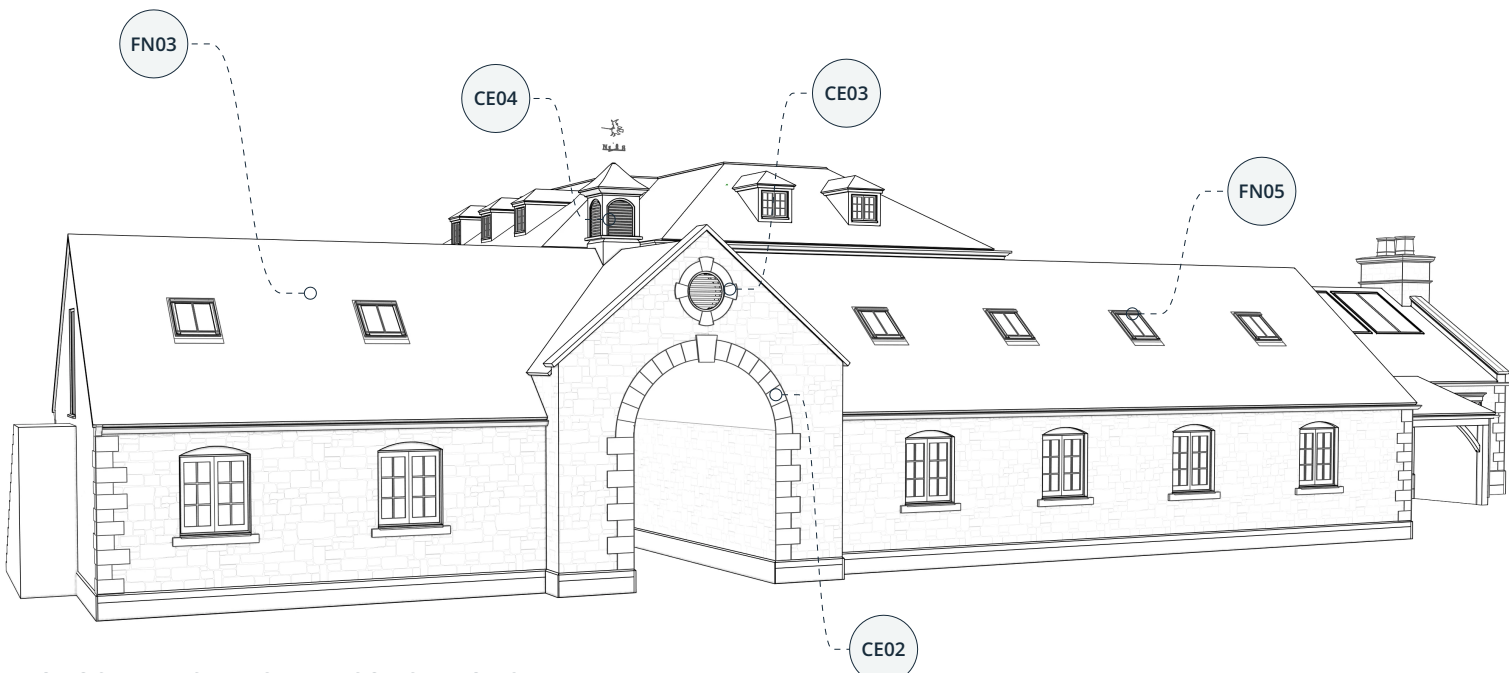

PROPOSED WEST FACADE - COACH HOUSE