


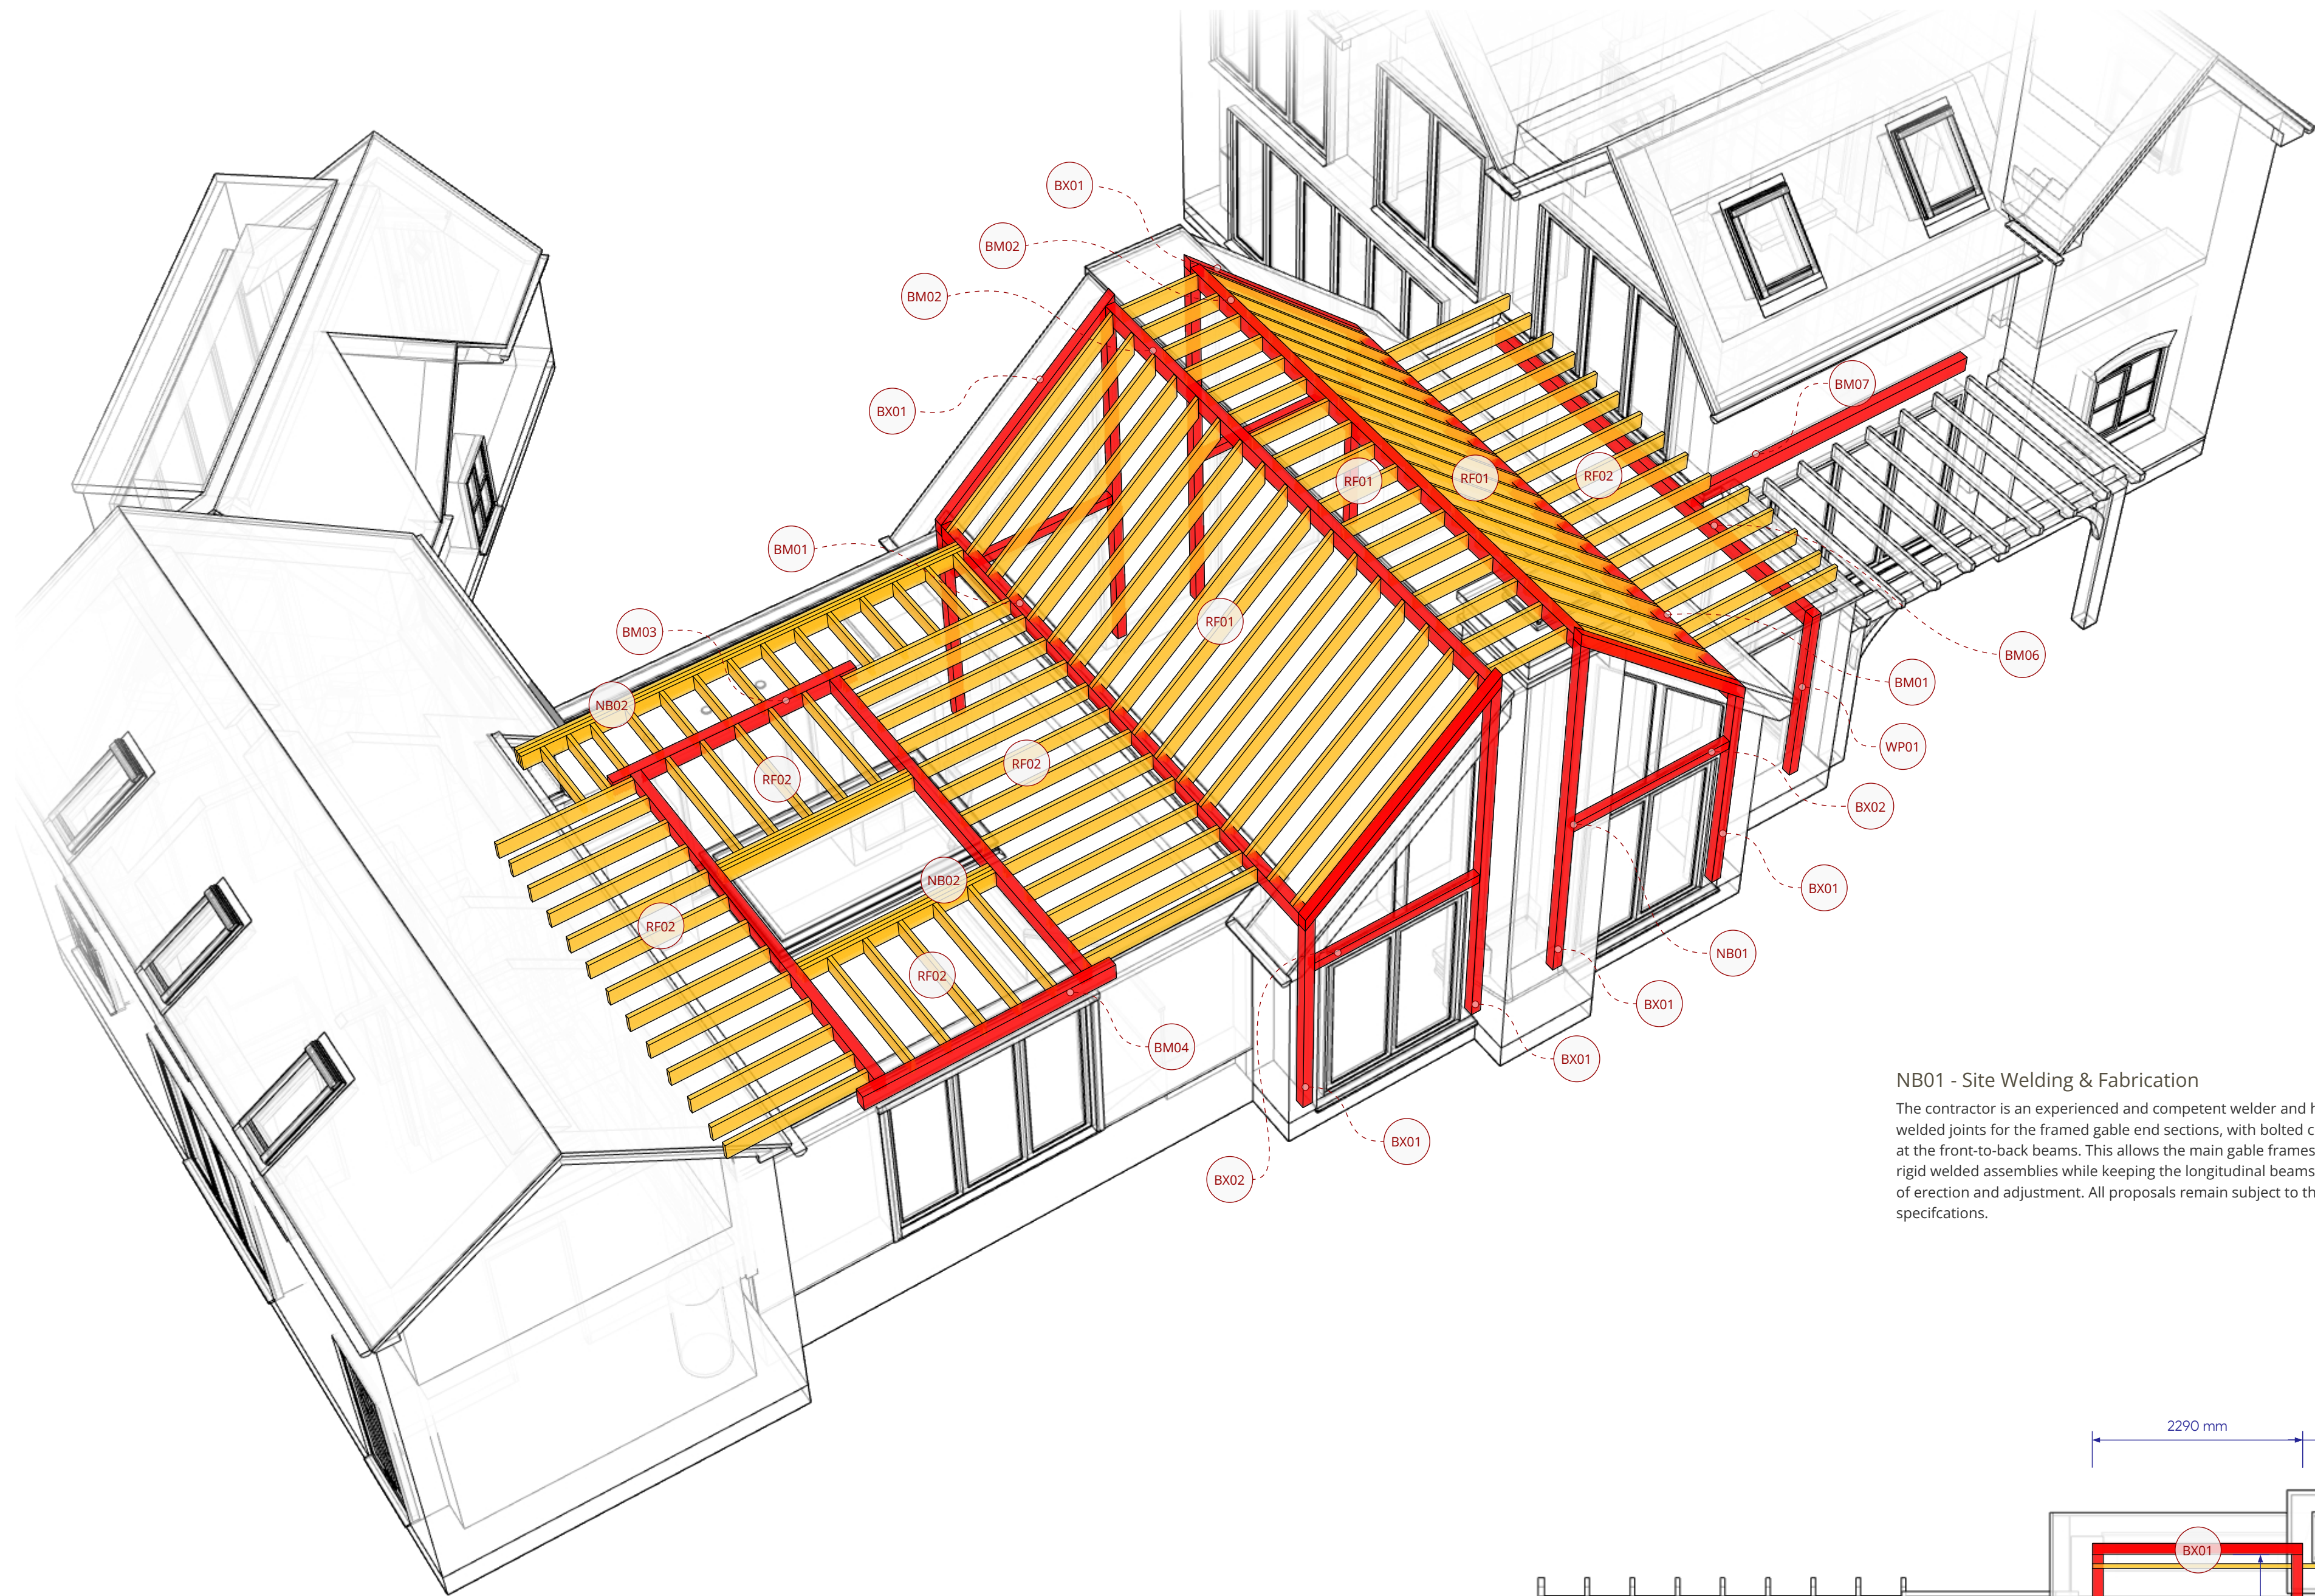

NB01 - Site Welding & Fabrication

The contractor is an experienced and competent welder and has proposed fully welded joints for the framed gable end sections, with bolted connections used only at the front-to-back beams. This allows the main gable frames to be fabricated as rigid welded assemblies while keeping the longitudinal beams demountable for ease of erection and adjustment. All proposals remain subject to the Structural engineer's specifications.

Structural Member Rough Profiles Table	
Member	Description
BX01	120 x 120 x ### SHS
BX02	120 x 120 x ### SHS
RF01	150 ~ 200 x 50 C24 : Pitched Timber Rafters
RF02	150 ~ 200 x 50 C24 : Flat Timber Rafters
BM01	250 ~ 350 x 100 ~ 125 : Universal Beam : Eaves Beam
BM02	250 ~ 350 x 100 ~ 125 : Universal Beam : Ridge Beam
BM03	175 ~ 250 x 100 : Universal Beam : Entrance Door Beam
BM04	175 ~ 250 x 100 : Universal Beam : Gallery Door Beam
BM05	175 ~ 225 x 100 : Universal Beam / Col : Roof Light Ring Beam
BM06	175 ~ 250 x ###? : Universal Beam / Col : Wall Removal
BM07	175 ~ 250 x ###? : Universal Beam / Col : Wall Removal & Bifolds
WP01	100 x 100 x ### SHS Corner Windpost

Structural Member Table Notes

The preliminary structural member dimensions shown are rough allowances that have been built into the bulkheads, wall zones, and cavity widths. The engineer should work as closely as practical to these indicative sizes, as the architectural envelope has been detailed around the spatial allowance. If significantly larger members are required, the engineer should contact Noble Architecture before progressing. These sizes are not intended to represent standard steel sections; they are indicative bounding boxes only, provided to guide what can be accommodated within the architectural layout. Final section sizes and specifications remain entirely at the engineer's discretion.

Preliminary Structural Coordination Sketch


This drawing is a preliminary coordination sketch prepared to help the structural engineer assess and price the structural design work. It sets out a basic starting point for the proposed structural arrangement so that Noble Architecture and the engineer can develop the detailed scheme in tandem. It is not a final design, and the structural elements shown are indicative only and subject to the engineer's confirmation, amendment, or replacement.

PRELIMINARY DRAWING:

This drawing is strictly for use in supporting the structural engineer's tendering process and must not be used for fabrication, ordering, or installation under any circumstances. The contractor must not manufacture or install any components until the full approved structural calculations pack and final construction-issue drawings have been issued by the engineer and coordinated with Noble Architecture.

NB02 - Timber Trimmers

Timber rafter trimmers have been shown to complete the roof light ring beam and to also for the front porch fascia overhang. These have been used at this stage to keep installation weight down and simplify handling for the contractor. The engineer should advise whether these elements need to be replaced with steel members for structural performance or deflection control. Timber has been assumed as the lighter, more practical option, but steel can be introduced if required.

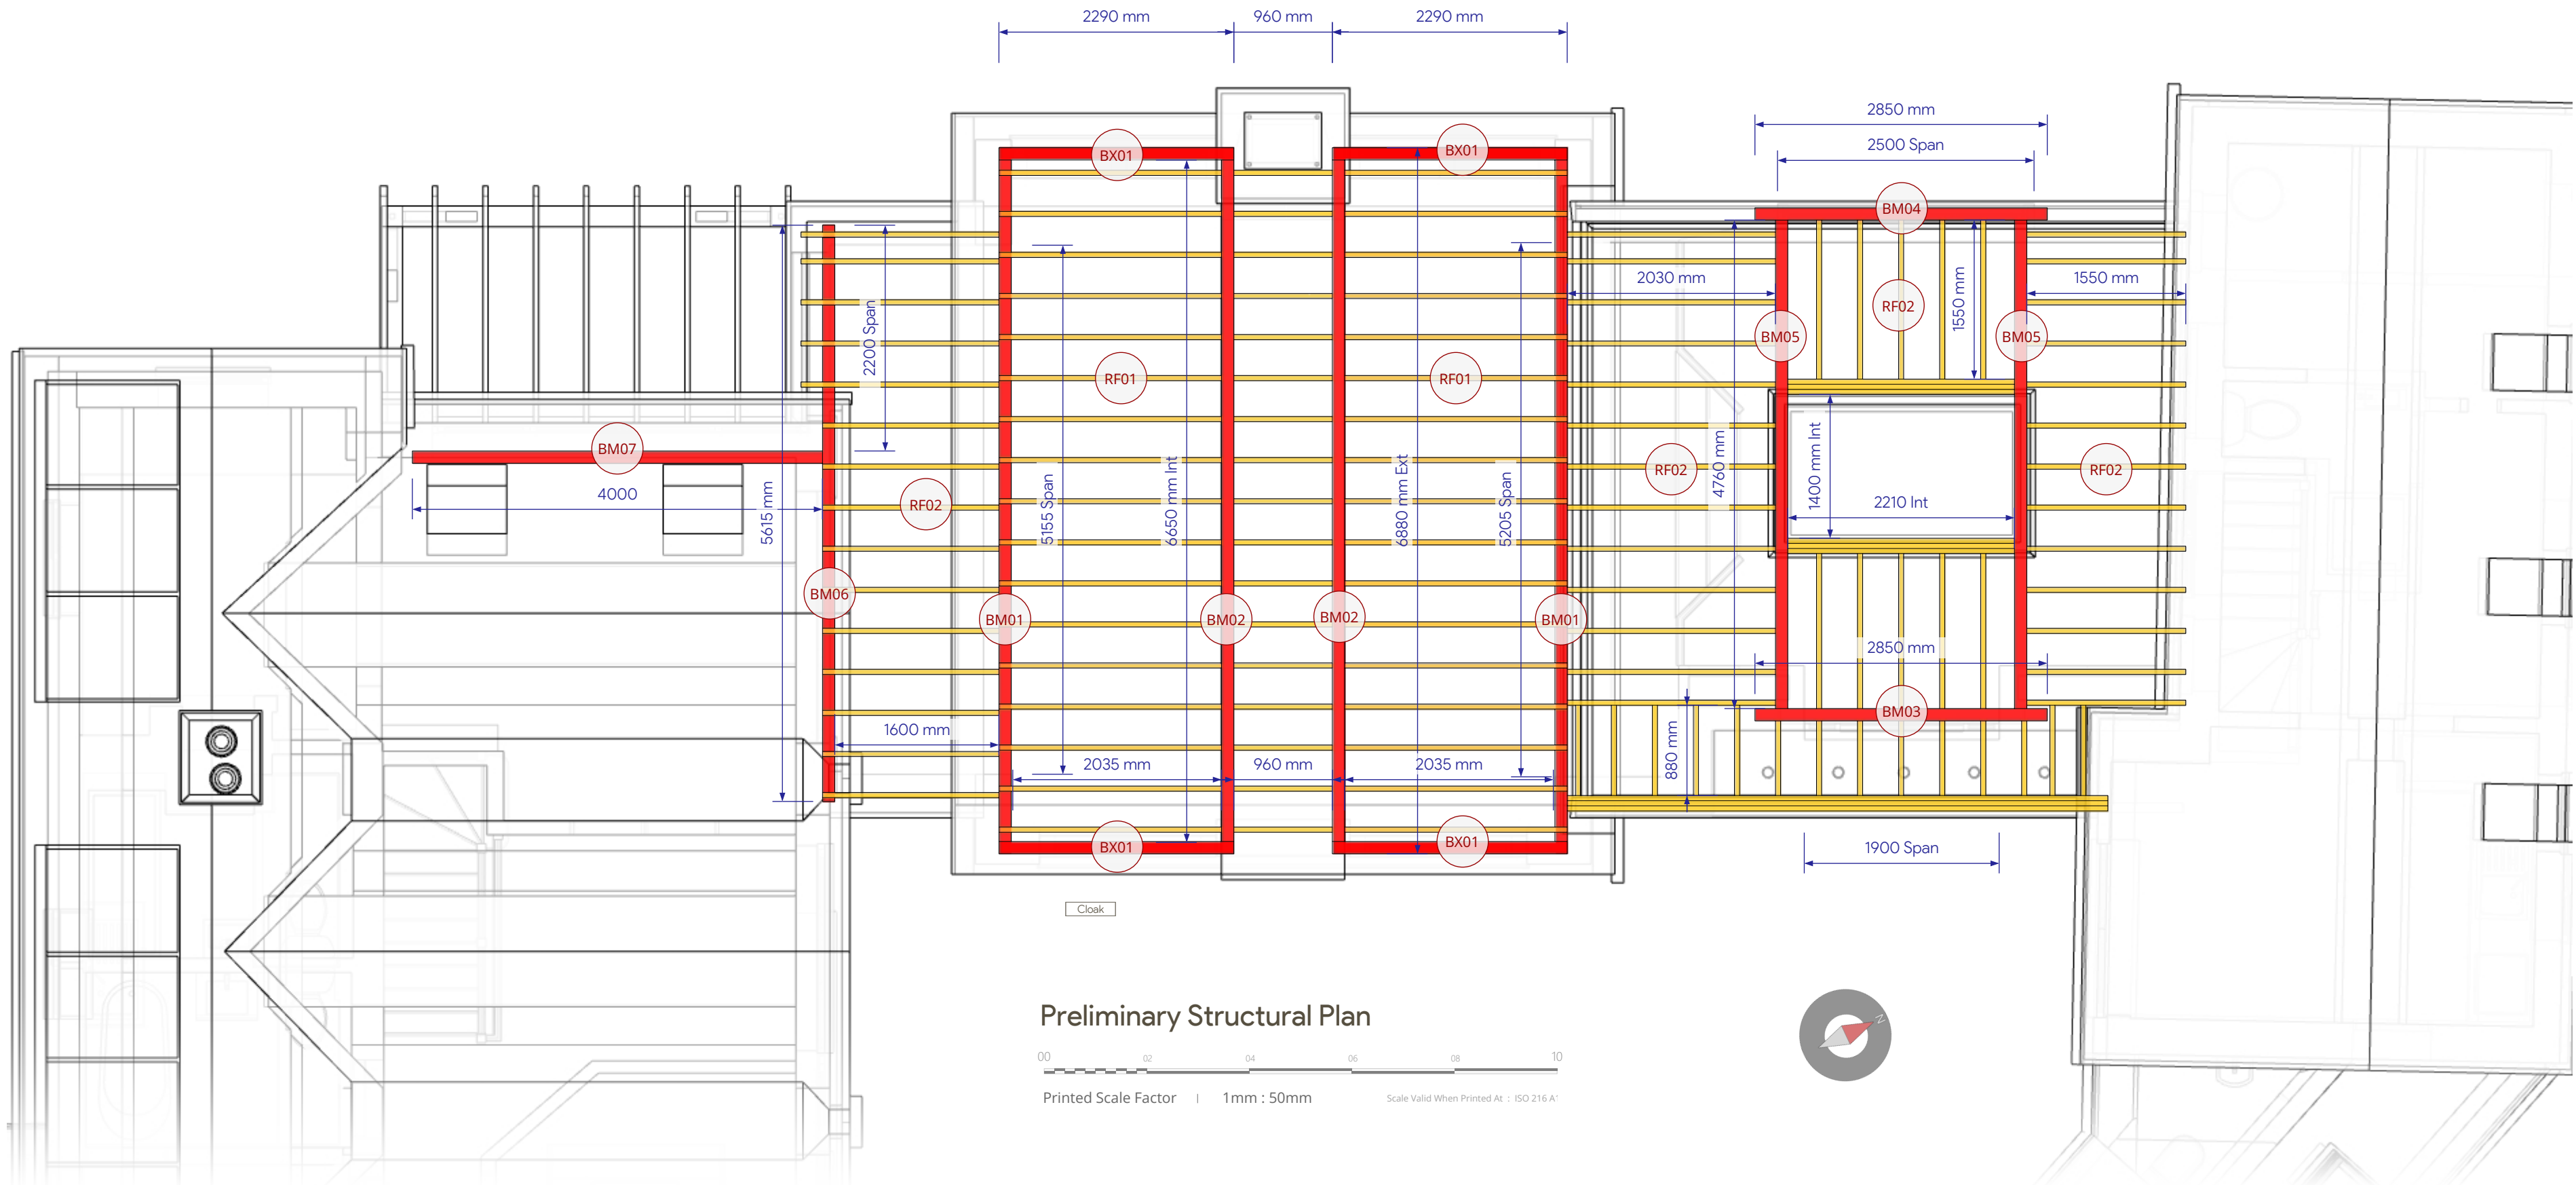

Preliminary Structural Plan

Printed Scale Factor | 1 mm : 50mm | Scale Valid When Printed At : ISO 216 A1

