


Use your phone or tablet camera

View Project Portal

- Walk Through the 3D Model
- Saved Scenes and Viewpoints
- Measuring Tools
- Live Drawings Online

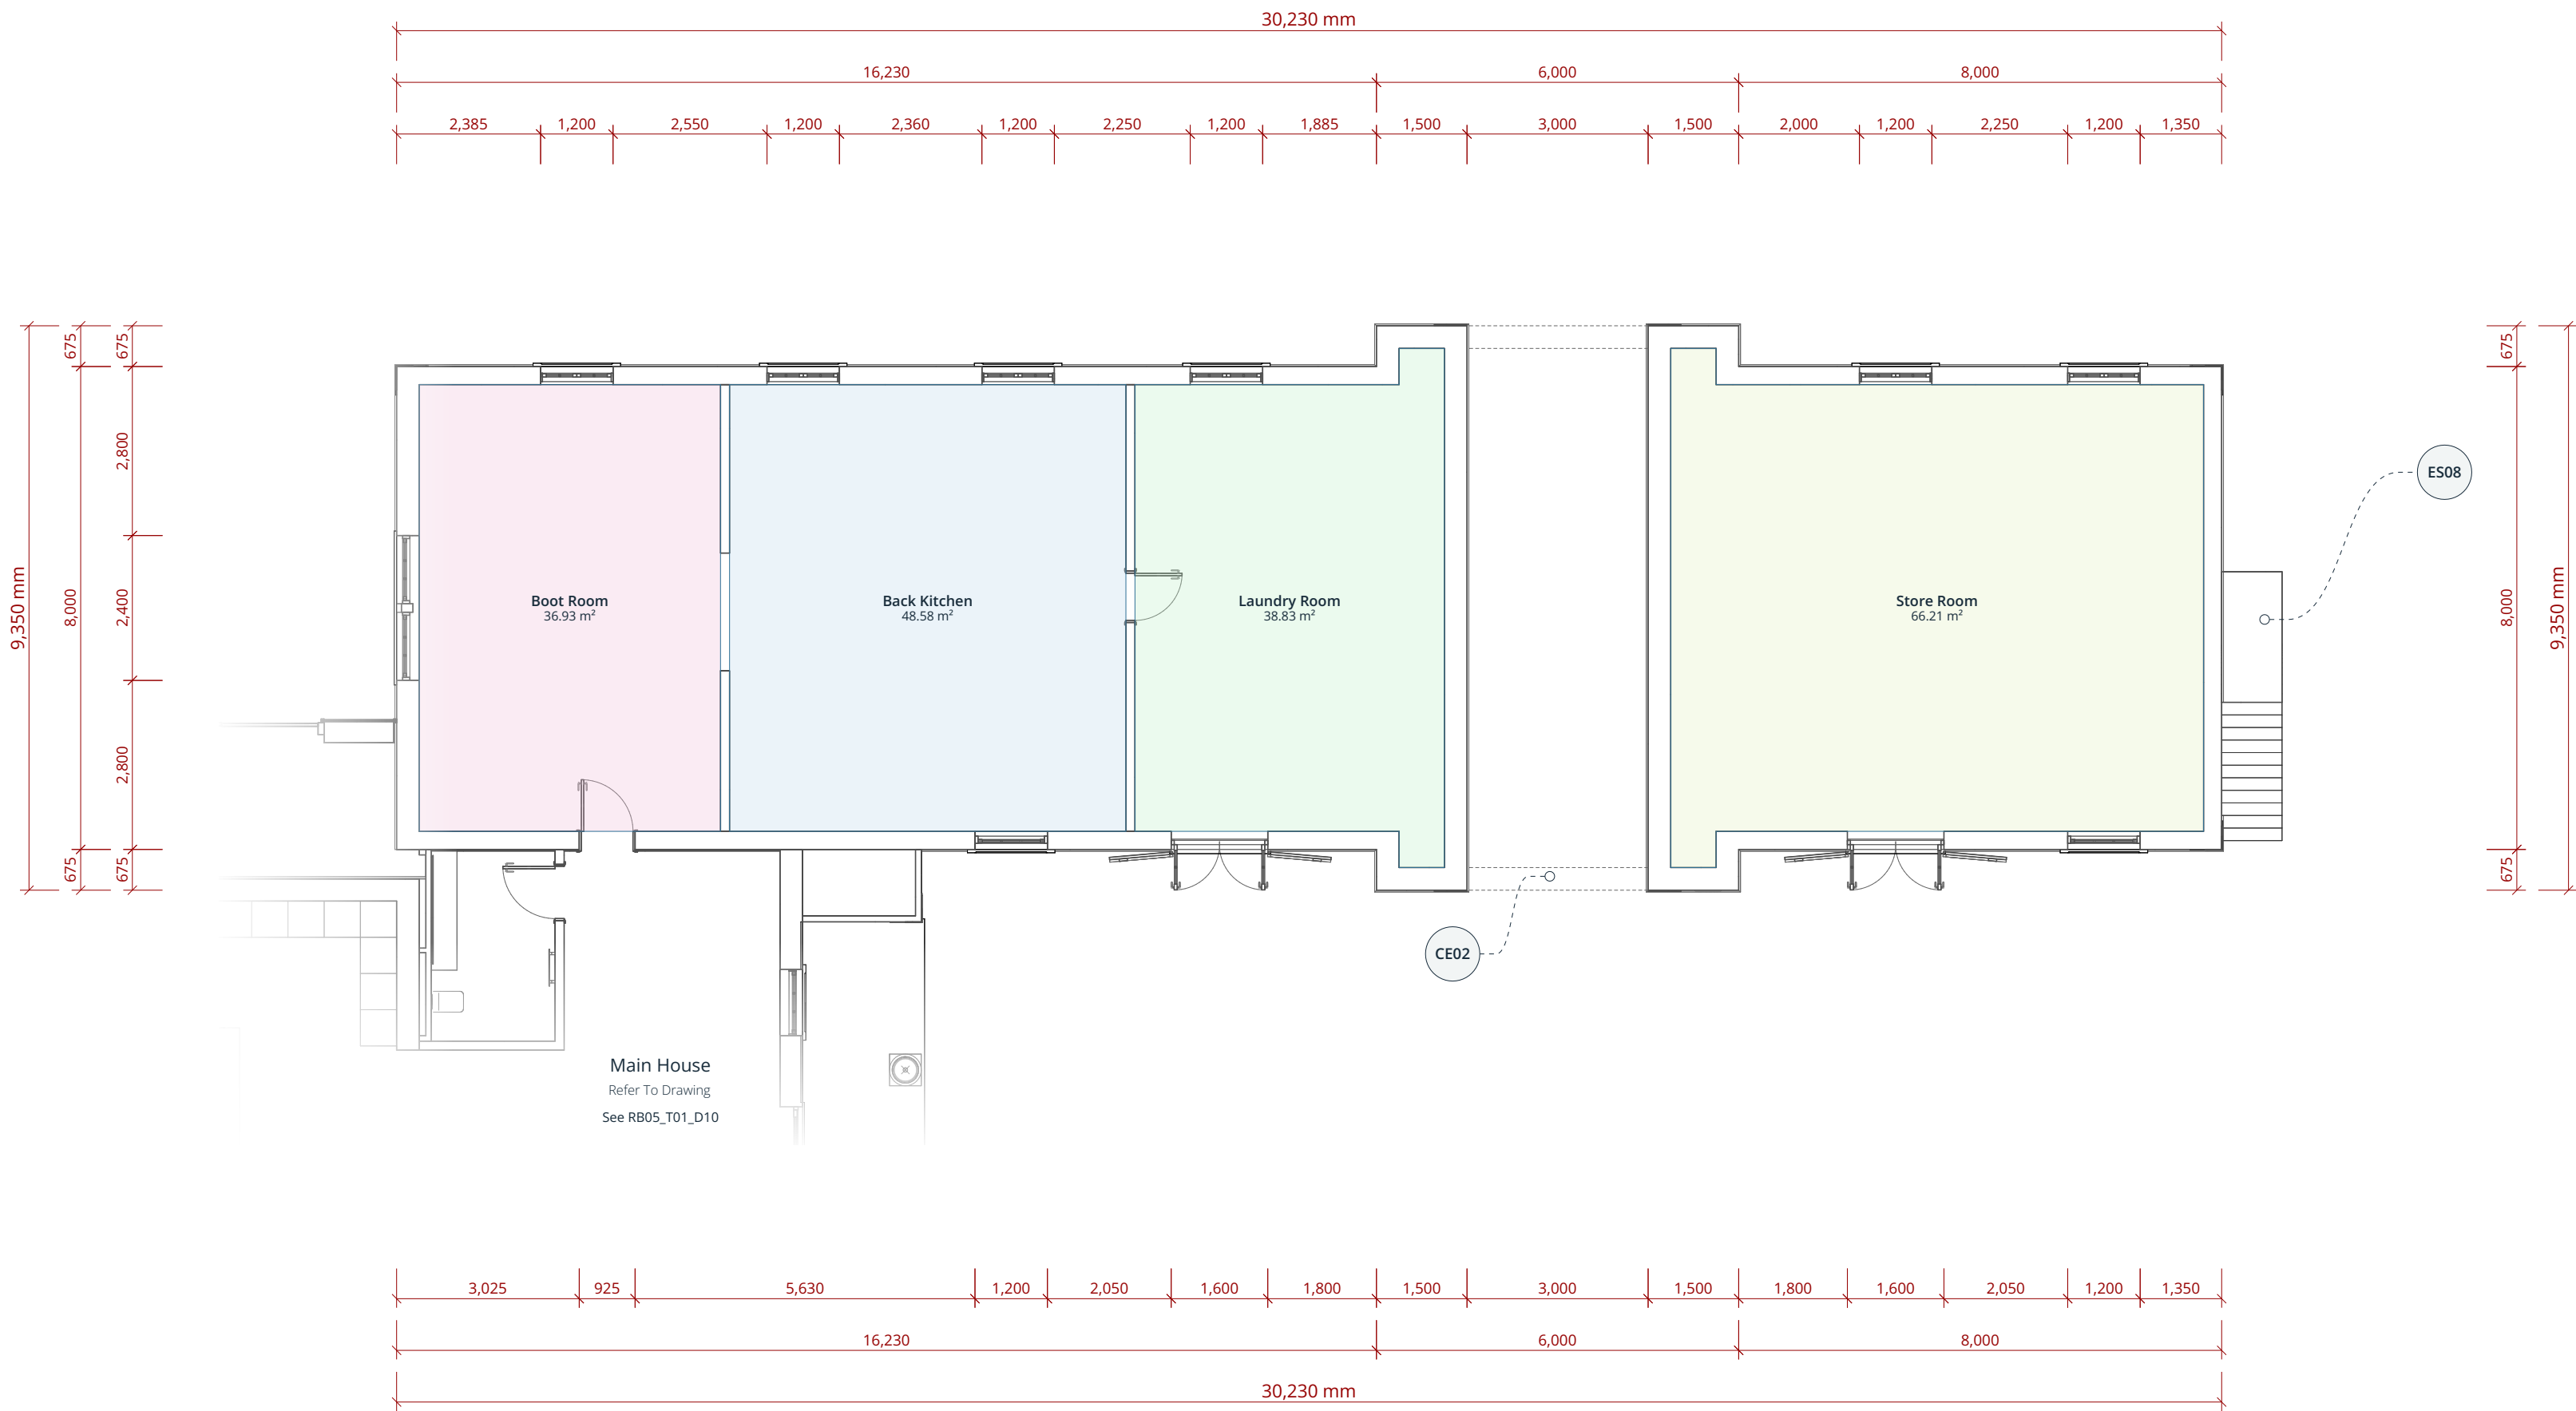

PROPOSED GROUND FLOOR PLAN - COACH HOUSE

NOTES

ES08 | Coach House External Stair
Indicative external staircase to the accommodation over the coach house, shown to establish the access only. Form, construction and finish to be confirmed before a full application.

CE02 | Carriage Arch
Central gabled bay carries a semicircular carriage arch turned in voussiors with a projecting keystone, on cut ashlar imposts with quoined jambs. The arch carries the pedestrian and service route through from the courtyard.

GN01 | Drawing Scope
Drawings describe the proposed development for planning assessment. They are not construction drawings or a complete Building Regulations specification. Obtain coordinated construction details, structural calculations and Building Control approval before relevant work starts. Refer discrepancies to Noble Architecture before proceeding.

GN02 | Survey And Dimensions
Site information derived from a photogrammetric aerial survey of the holding, with purchased Ordnance Survey data to the site plans. No measured building survey of the existing dwelling has been carried out. Proposed buildings are derived from Noble Architecture's three-dimensional model. Do not scale from these drawings. Verify all dimensions on site.

GN03 | Pre-Application Status
Issued for pre-application advice. Materials, dimensions and levels are indicative at this stage and to be fixed before a planning application.

Floor Areas

Room	Area
Ground Floor - Coach House	190.54 m²
Boot Room	36.93 m²
Back Kitchen	48.58 m²
Laundry Room	38.83 m²
Store Room	66.21 m²
Total	190.54 m²

Floor Areas

Room	Area
Ground Floor - Coach House	2,051 ft²
Boot Room	397 ft²
Back Kitchen	523 ft²
Laundry Room	418 ft²
Store Room	713 ft²
Total	2,051 ft²