



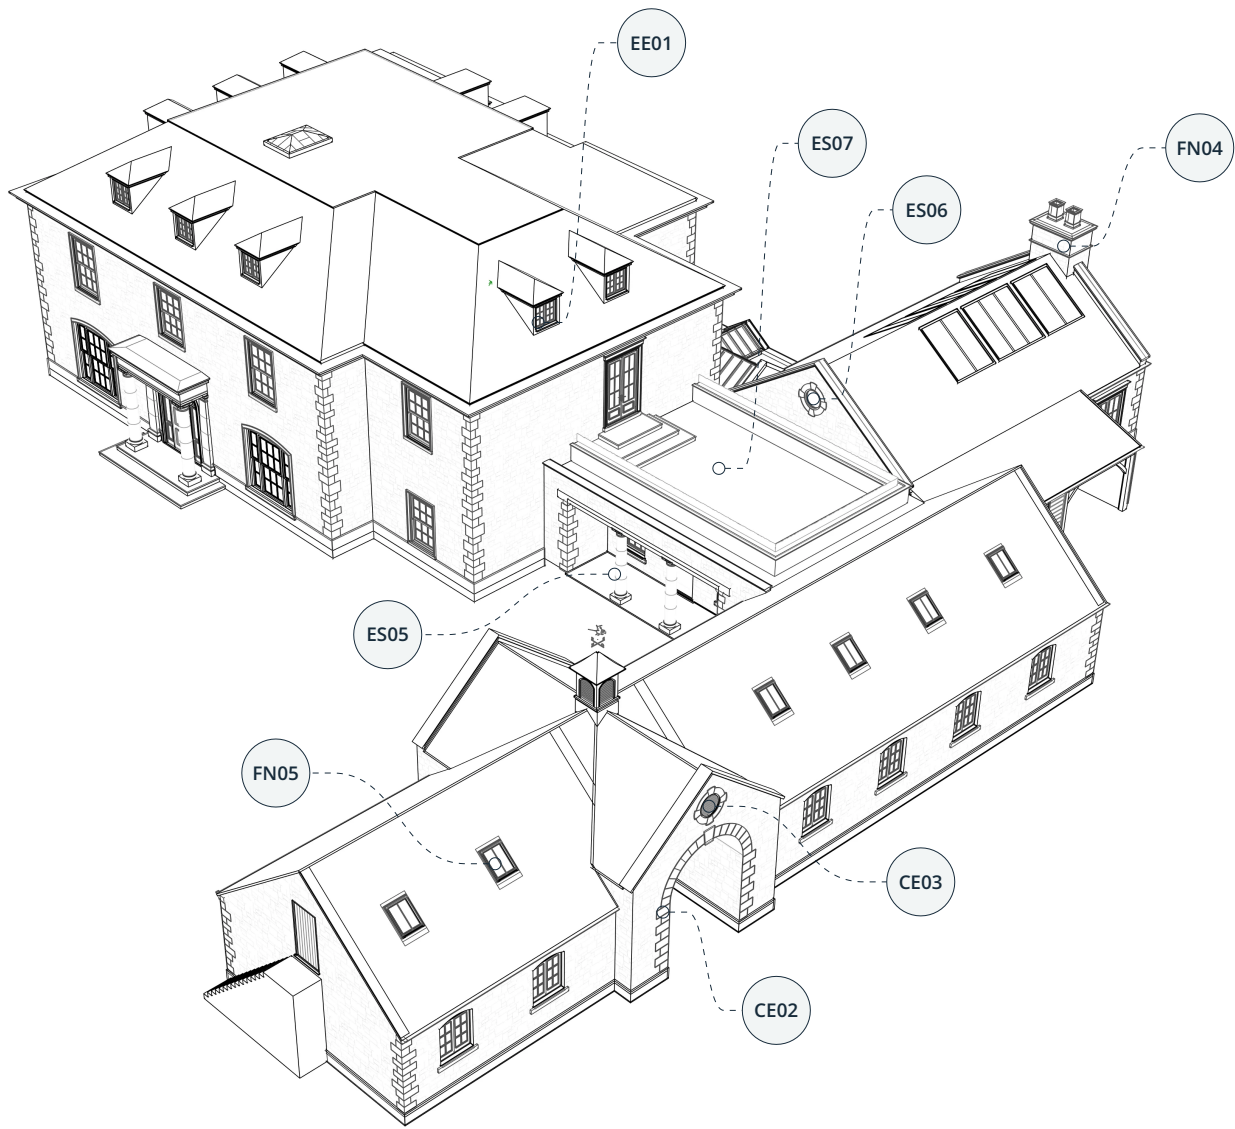


Design Proposal | Birds-eye View 01

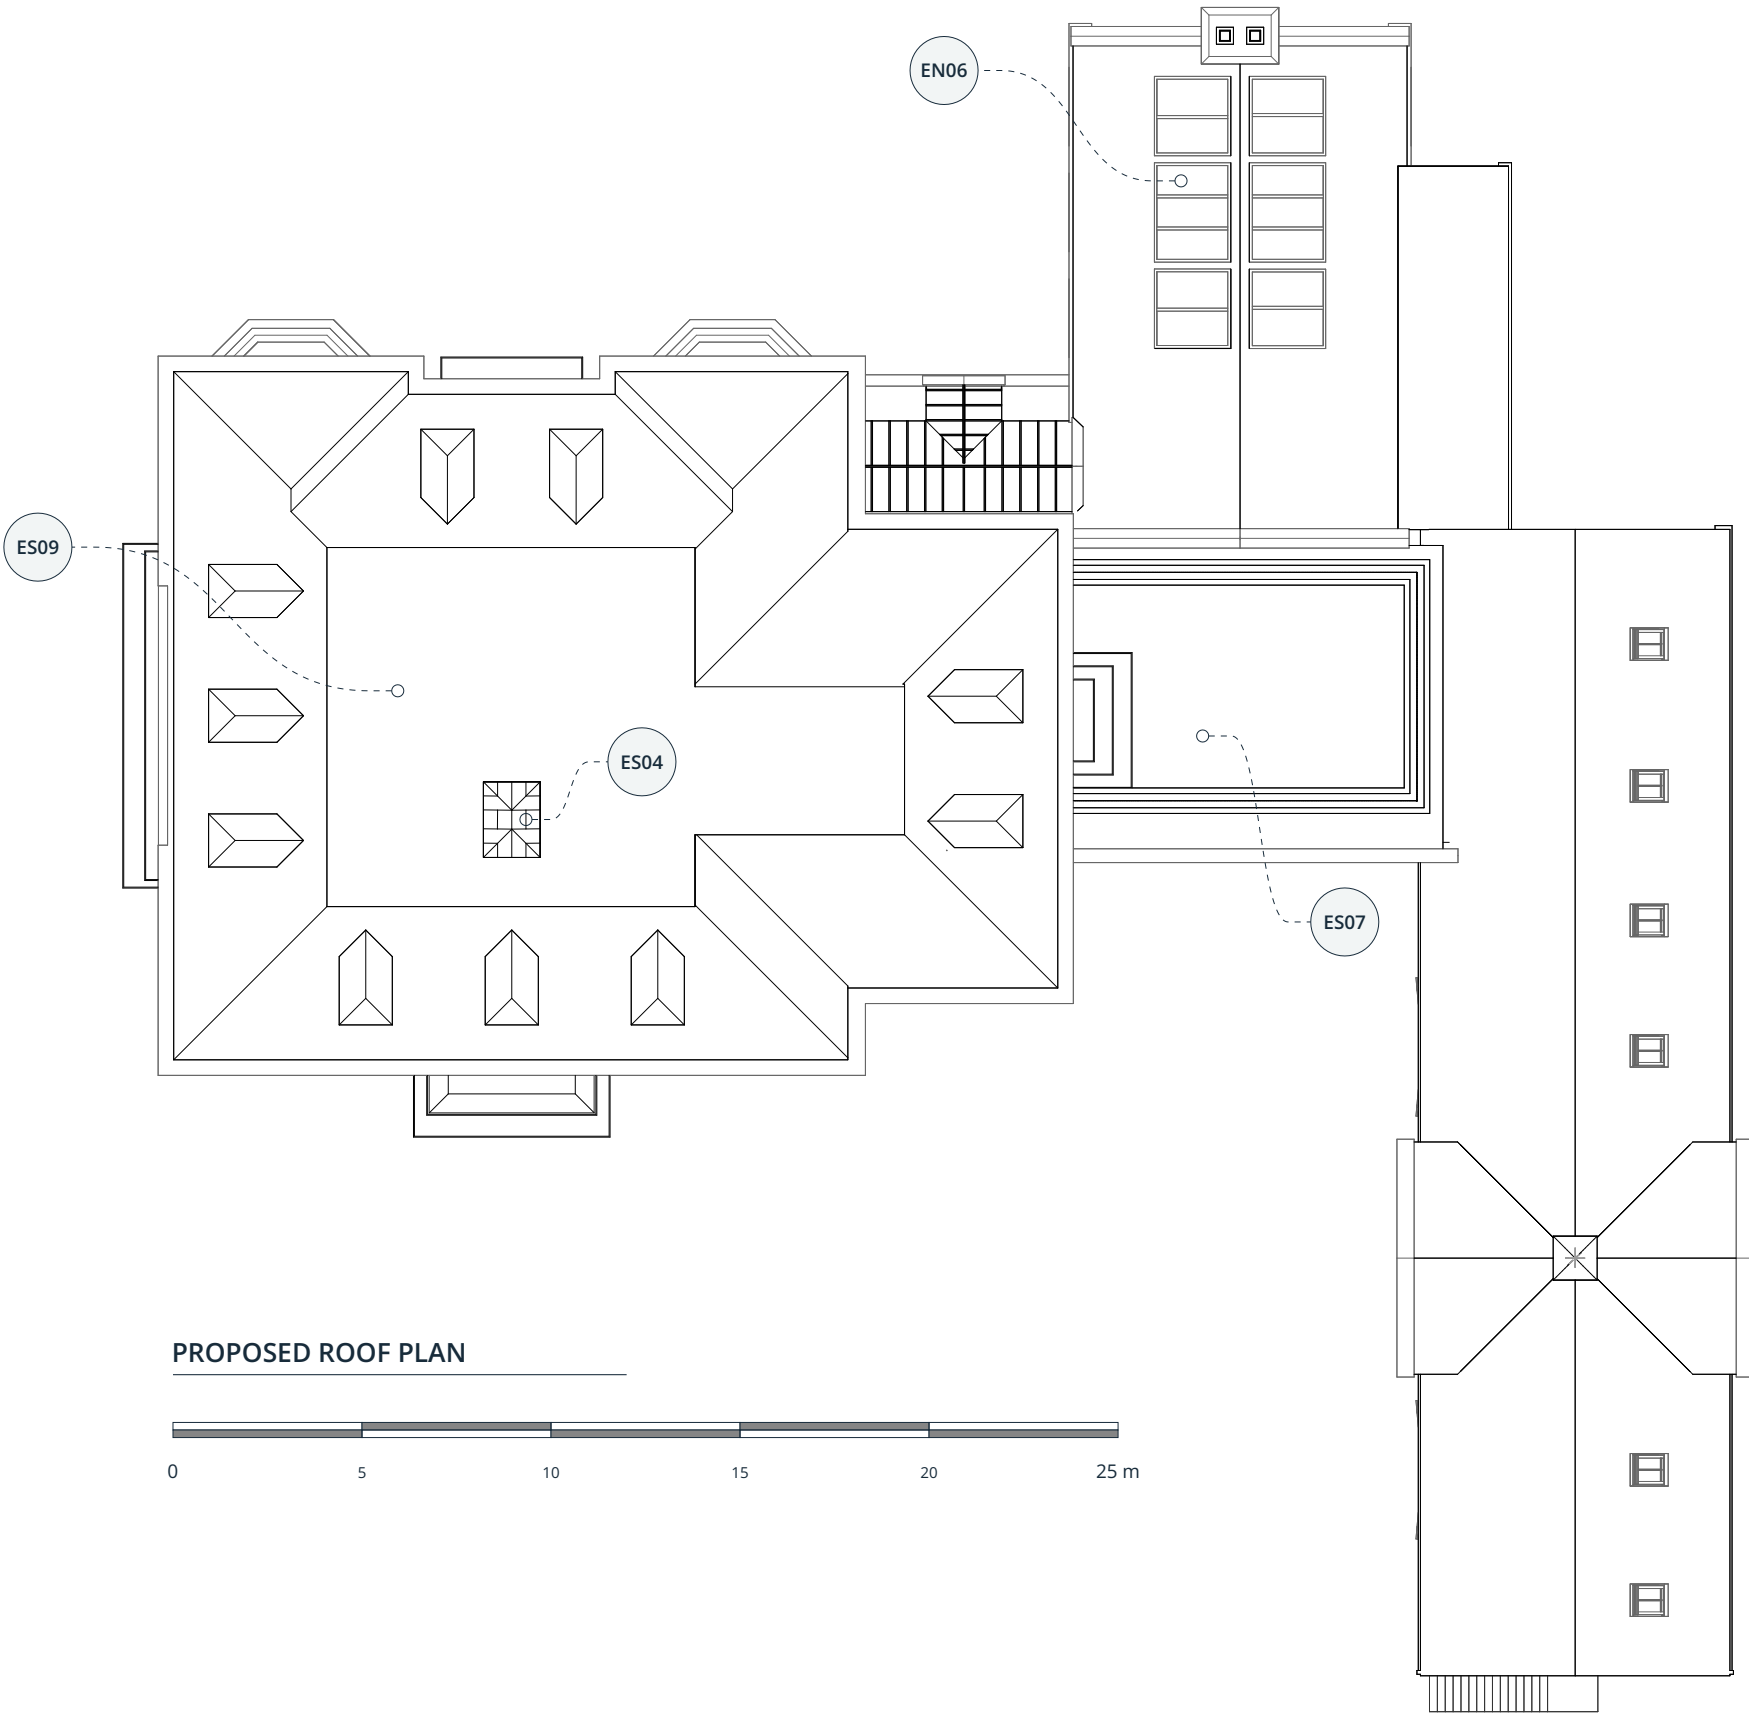

PROPOSED ROOF PLAN



Design Proposal | Birds-eye View 02

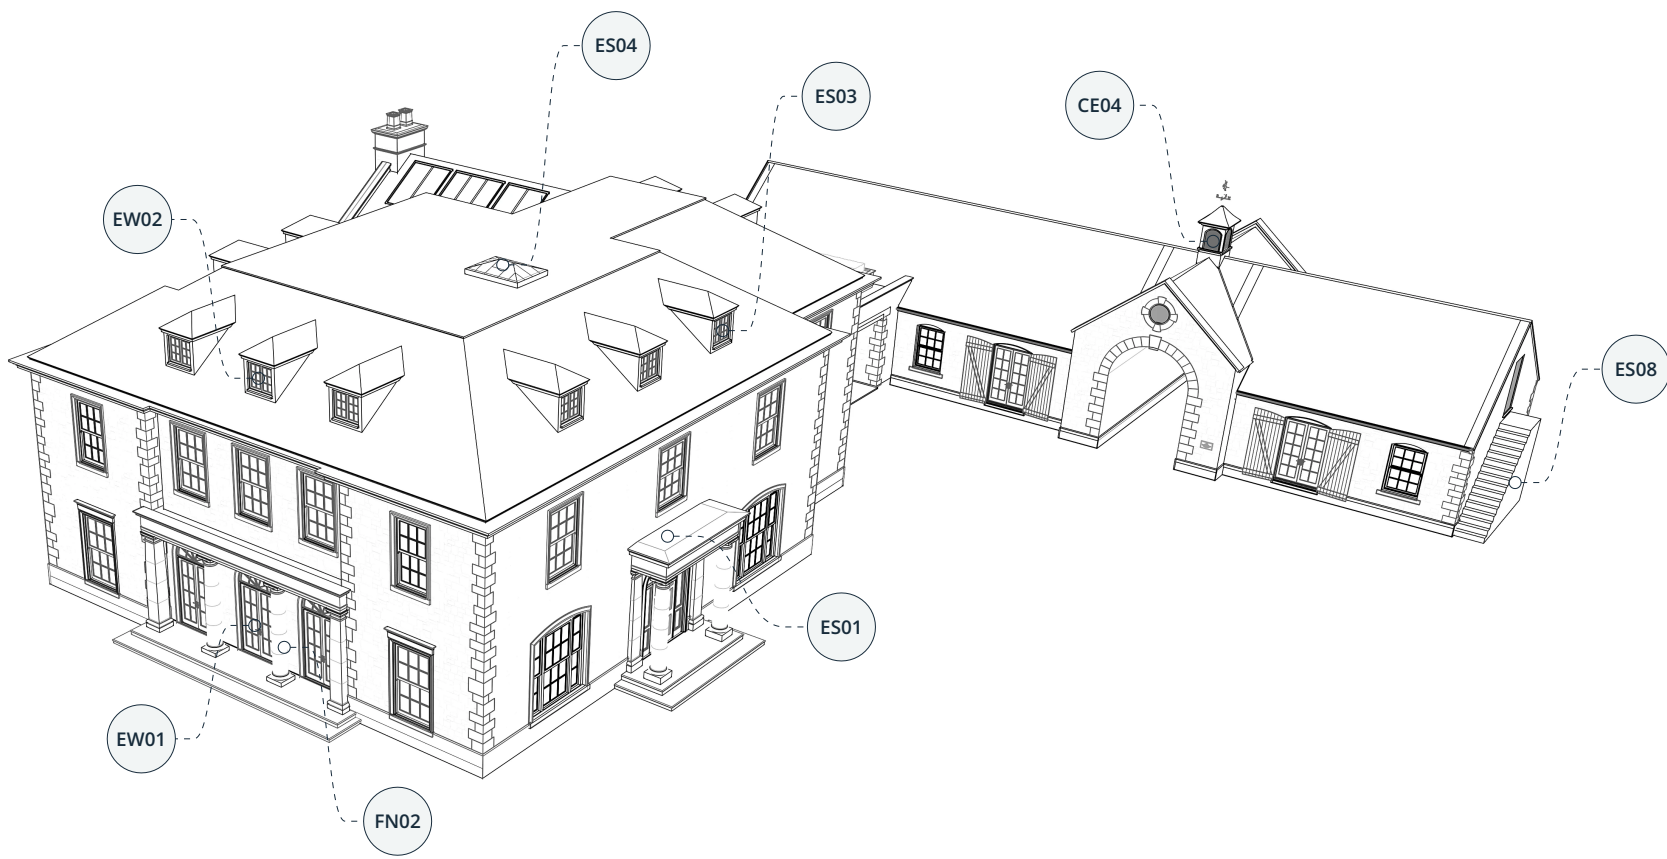

Design Proposal | Birds-eye View 03

NOTES

EN01 | Entrance Composition

Central entrance: six-panel painted timber door with narrow sidelights, on cut ashlar jambs standing on plinth blocks. A deep moulded entablature with projecting cornice sits above, and a semicircular radial fanlight above that, framed by concentric moulded archivolts.

EN02 | Cant Bay Windows

Canted bays flank the entrance, in cut ashlar throughout, with a moulded cornice and blocking course at the head. French doors to the centre face and sashes to the splayed returns, opening onto the terrace.

EN03 | First Floor And Dormers

First floor painted timber sashes in moulded surrounds, with two hipped dormers above within the roof slope.

EN04 | Orangery Link

Orangery between the house and the kitchen building: painted timber, glazed the full height of its bays, under a bespoke glazed lantern, applicant to consider a traditional manufacturer such as Vale Garden House who can provide the level of finish required for such a bespoke painted hardwood orangery structure..

EN05 | Kitchen Building Gable Openings

Kitchen building gable: two tall arched openings with radial fanlights in cut ashlar surrounds. Stone chimney stack against the gable.

EN06 | Kitchen apex rooflights

Kitchen building: glazed apex rooflights to both roof slopes at the ridge, set flush with the roof covering of FN03 in the manner of conservation rooflights. They light a vaulted ceiling with exposed roof timbers. Frame material, finish and product to be confirmed before a full application.

ES01 | Entrance Porch

Central entrance: a pair of Tuscan columns on plinth blocks carry a full entablature with a projecting moulded cornice. Beneath it a six-panel painted timber door with a semicircular radial fanlight, dressed in cut ashlar and approached over stone steps. The porch projects slightly from the wall plane.

ES03 | Roof And Dormers

Hipped roof with three hipped dormers lighting the second floor. Dormer cheek and roof finish to be confirmed before a full application.

ES04 | Ridge Lantern

Low hipped glazed lantern set astride the main ridge at the centre of the house. Frame material and finish to be confirmed before a full application.

ES05 | Colonnade Entrance

Single-storey colonnade entrance to the right of the main block: Tuscan columns flanking a glazed painted timber door, with flat ashlar lintels over the windows either side, beneath a flat roof with a moulded cornice. Leads through to the kitchen building and the coach house.

ES06 | Kitchen Building Gable

Kitchen building gable above the colonnade entrance: moulded raking cornice, with a circular opening set in cut ashlar with four projecting keyblocks. Stone chimney stack rises behind.

ES07 | Colonnade Balcony

Balcony over the colonnade entrance, reached down steps from the master bedroom suite. Parapet set back from the face below, with planting beds to the edges in place of a balustrade. The set-back keeps the balcony reading as the colonnade roof from ground level. Refer to the three-dimensional model on the project portal.

ES08 | Coach House External Stair

Indicative external staircase to the accommodation over the coach house, shown to establish the access only. Form, construction and finish to be confirmed before a full application.

ES09 | Crown roof form

Main house roof: crown form, a flat lead deck at the crown within pitched surrounds. The crown lowers the ridge within the landscape setting; the pitched surrounds keep it reading as a hipped roof from ground level. Deck extent, pitch and lead specification to be confirmed before a full application. Pitched roof covering as FN03.

EE01 | House Roof Beyond

The house is seen above the coach house range on this elevation: hipped roof with two hipped dormers and the moulded eaves cornice returning on this side.

EE02 | Lean-To Store

Single-storey lean-to store against the kitchen building, under a mono-pitch roof with eaves set below those of the kitchen building. Horizontal timber weatherboarding to the walls. Ancillary storage for garden furniture and pool equipment. Roof covering to be confirmed before a full application.

EW01 | Loggia Arcade

Three arched openings in a recessed bay at ground floor. Tuscan columns, with matching responds returned against the flanking walls, carry a full entablature with plain frieze and projecting cornice. French doors beneath radial fanlights to each arch. The arcade is recessed within the wall plane and does not project beyond the elevation.

EW02 | Flanking Windows And Dormers

Larger windows flank the arcade at both levels, with three hipped dormers above within the roof slope.

FN02 | Classical Order

All columns and pilasters are of the Tuscan order in cut ashlar: the entrance porch, the loggia arcade and the colonnade entrance.

FN03 | Roof Covering

Natural stone slate laid to diminishing courses to all pitched roofs. Stone slate type, and whether new or reclaimed, to be confirmed before a full application.

FN04 | Chimney Stack

Natural stone chimney stacks with moulded caps to the house, the kitchen building and the coach house.

FN05 | Rooflights

Conservation pattern rooflights set flush within the roof plane to the coach house. Kitchen building apex rooflights as EN06. Product to be confirmed before a full application.

CE01 | Coach House Range

Long single-storey range under a continuous pitched roof, with accommodation lit from within the roof slope.

CE02 | Carriage Arch

Central gabled bay carries a semicircular carriage arch turned in voussiors with a projecting keystone, on cut ashlar imposts with quoined jambs. The arch carries the pedestrian and service route through from the courtyard.

CE03 | Gable Oculus

Circular louvred oculus in the gable above the arch, set in a cut ashlar surround with four projecting keyblocks.

CE04 | Cupola

Cupola on the ridge above the gable: square base with an arched louvred opening and a moulded cornice, pyramidal roof, ball finial and weathervane. Material and finish to be confirmed before a full application.

GN01 | Drawing Scope

Drawings describe the proposed development for planning assessment. They are not construction drawings or a complete Building Regulations specification. Obtain coordinated construction details, structural calculations and Building Control approval before relevant work starts. Refer discrepancies to Noble Architecture before proceeding.

GN02 | Survey And Dimensions

Site information derived from a photogrammetric aerial survey of the holding, with purchased Ordnance Survey data to the site plans. No measured building survey of the existing dwelling has been carried out. Proposed buildings are derived from Noble Architecture's three-dimensional model. Do not scale from these drawings. Verify all dimensions on site.

GN03 | Pre-Application Status

Issued for pre-application advice. Materials, dimensions and levels are indicative at this stage and to be fixed before a planning application.

